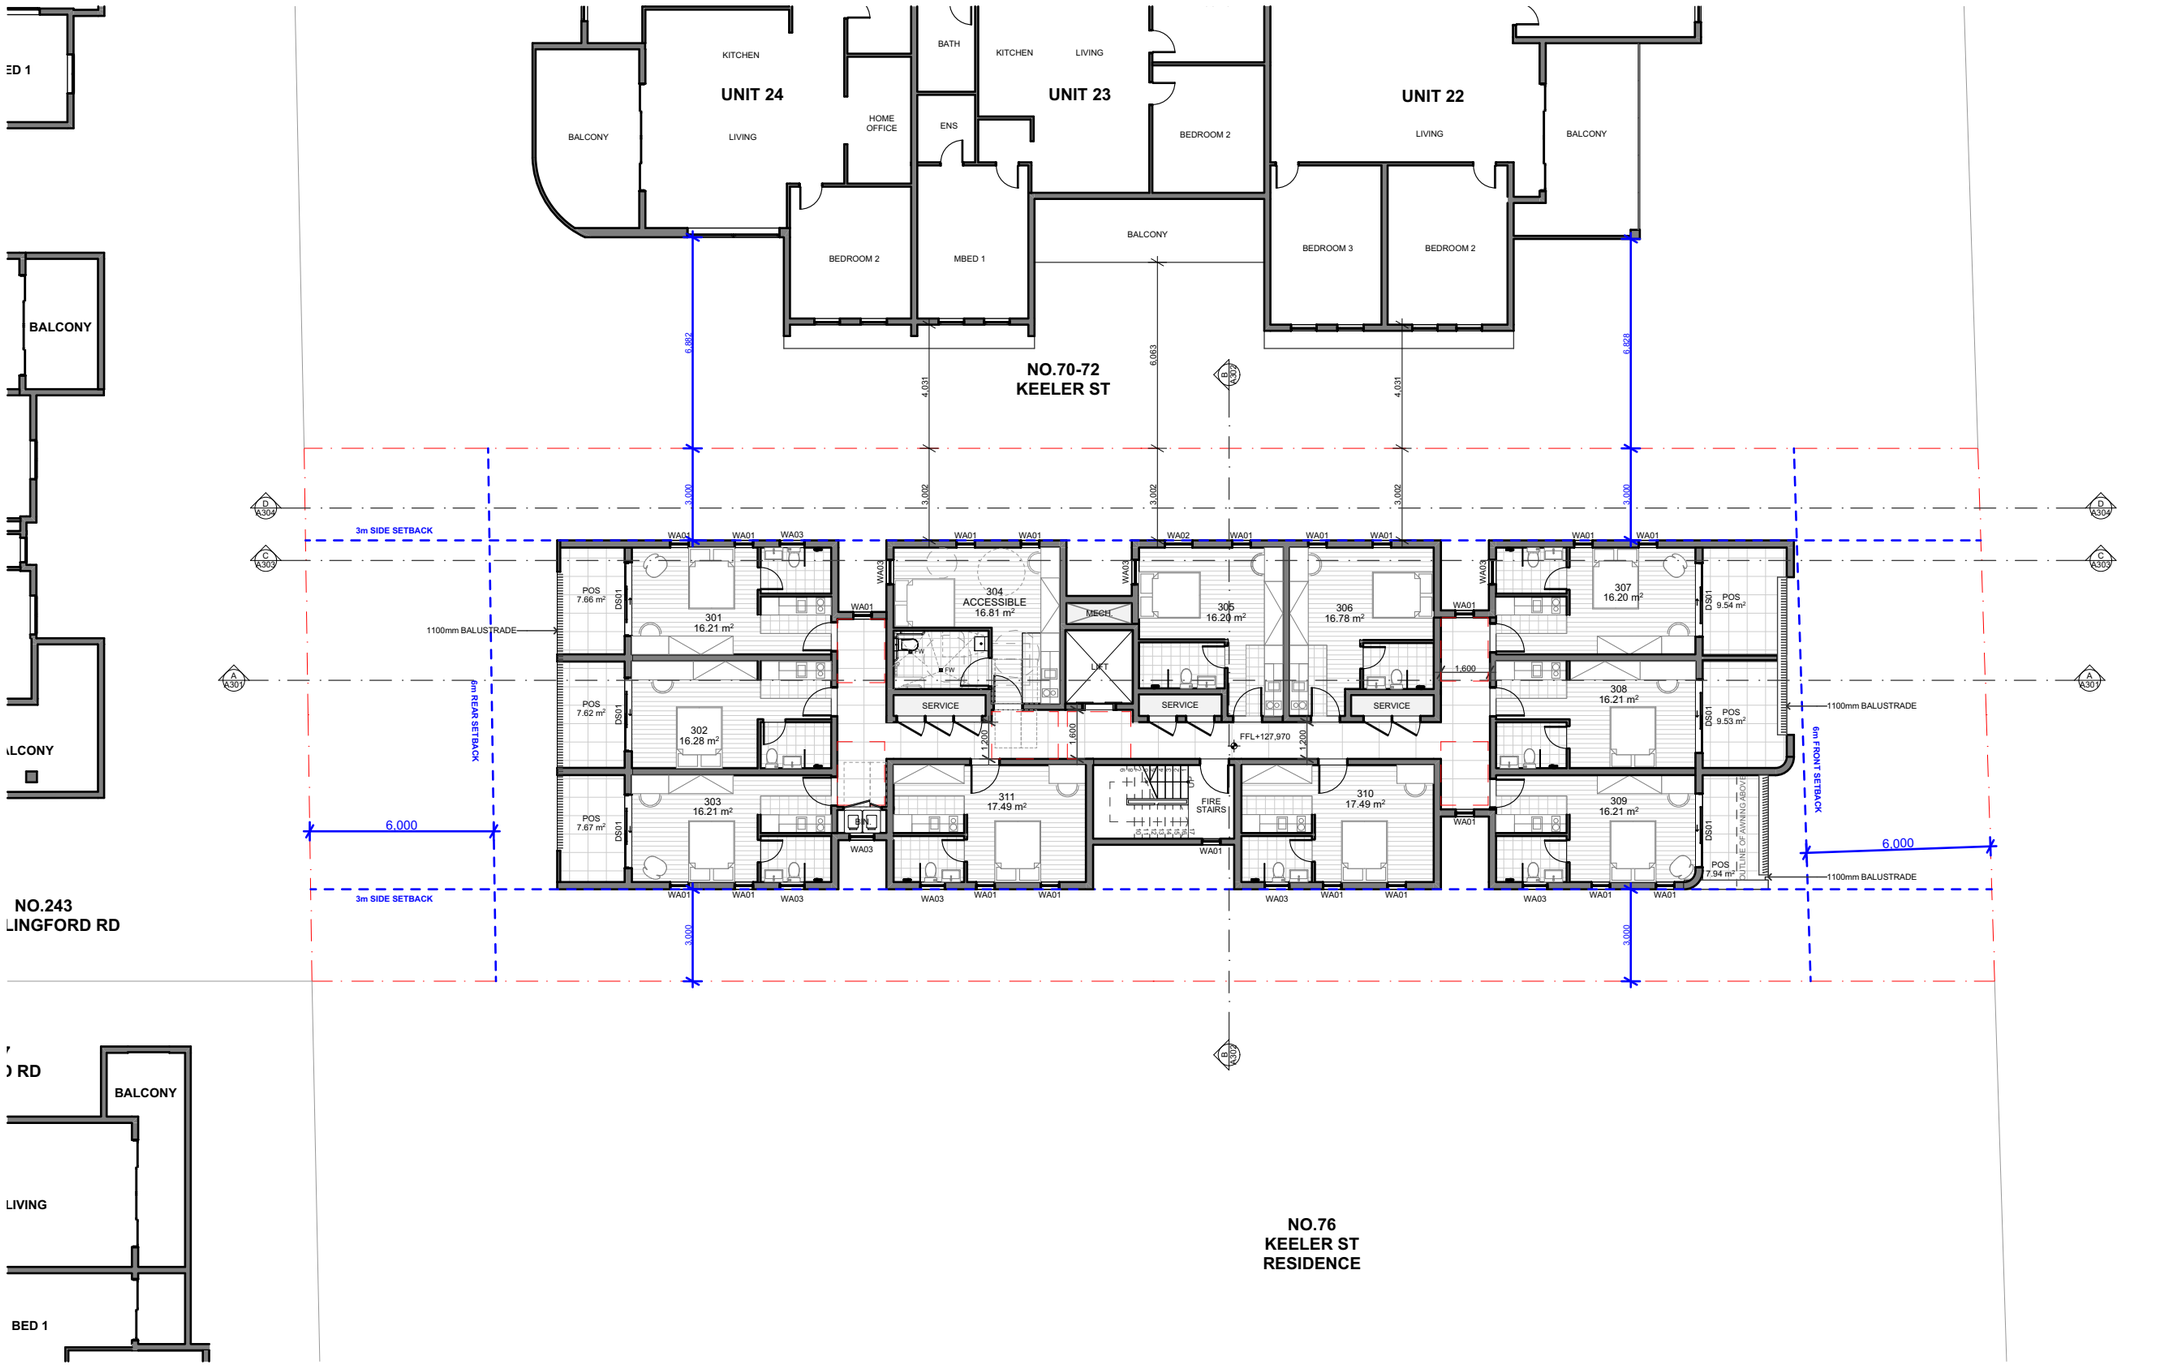

NOTE

The Builder shall check all dimensions and levels on site prior to construction. Notify any errors, discrepancies or omissions to the architect. Refer to written dimensions only. Do not scale drawings. Drawings shall not be used for construction purposes until issued for construction. This drawing reflects a design by Texco Design Pty Ltd and is to be used only for work when authorised in writing by Texco Design Pty Ltd.

All boundaries and contours are subject to survey drawing. All levels to Australian Height Data. It is the contractors responsibility to confirm all measurements on site and locations of any services prior to work on site.

All documents here within are subject to Australian Copyright Laws.

Project Partners

Refer to consultant documentation when directed

- Planning Consultant	- Think Planners
- Ecologist	- SIA Ecological
- BCA & Access	- BIA
- Arborist Consultant	- NSW Trees
- QS Consultant	- Property & Building Assessment
- Section J Consultant	- AENEC
- Civil Engineer	- JCO Consultants
- Stormwater Engineer	- JCO Consultants
- Landscape Designer	- Concept
- Traffic Engineer	- Genesis Traffic
- Land Surveyor	- RGM
- Geotechnical Engineer	- STANTEC
- Flood Engineer	- HYDRACOR

RevID	Transmittal Set Date	Approved by	Rev. Note
A	27/03/2024	T.Z	ISSUE FOR DA
B	16/01/2025	T.Z	ISSUE FOR S34
C	11/02/2025	T.Z	ISSUE FOR S34
D	03/03/2025		ISSUE FOR S34
E	13/03/2025	T.Z	ISSUE FOR S34
F	20/03/2025	T.Z	ISSUE FOR S34
G	19/09/2025		ISSUE FOR S34

Project Designer

TEXCO DESIGN
Nom Arch: NSW ARB 11348
E: office@texcodesign.com.au
P: +61 449 984 889

TRUE NORTH

Drawn | Checked	A.W I J.C |
Revision Date:	19/09/2025
Project NO.	2335
Project Status	S34
Client	MR BILLY CHEN
Site:	74 KEELER ST CARLINGFORD
Climate Zone	5
Wind Region	A

PAPER A3 1:200

DRAWING TITLE : PLANS LEVEL 3 PLAN

PROJECT NAME : 74 KEELER ST CARLINGFORD

REVISION NO. G

DRAWING NO. A105

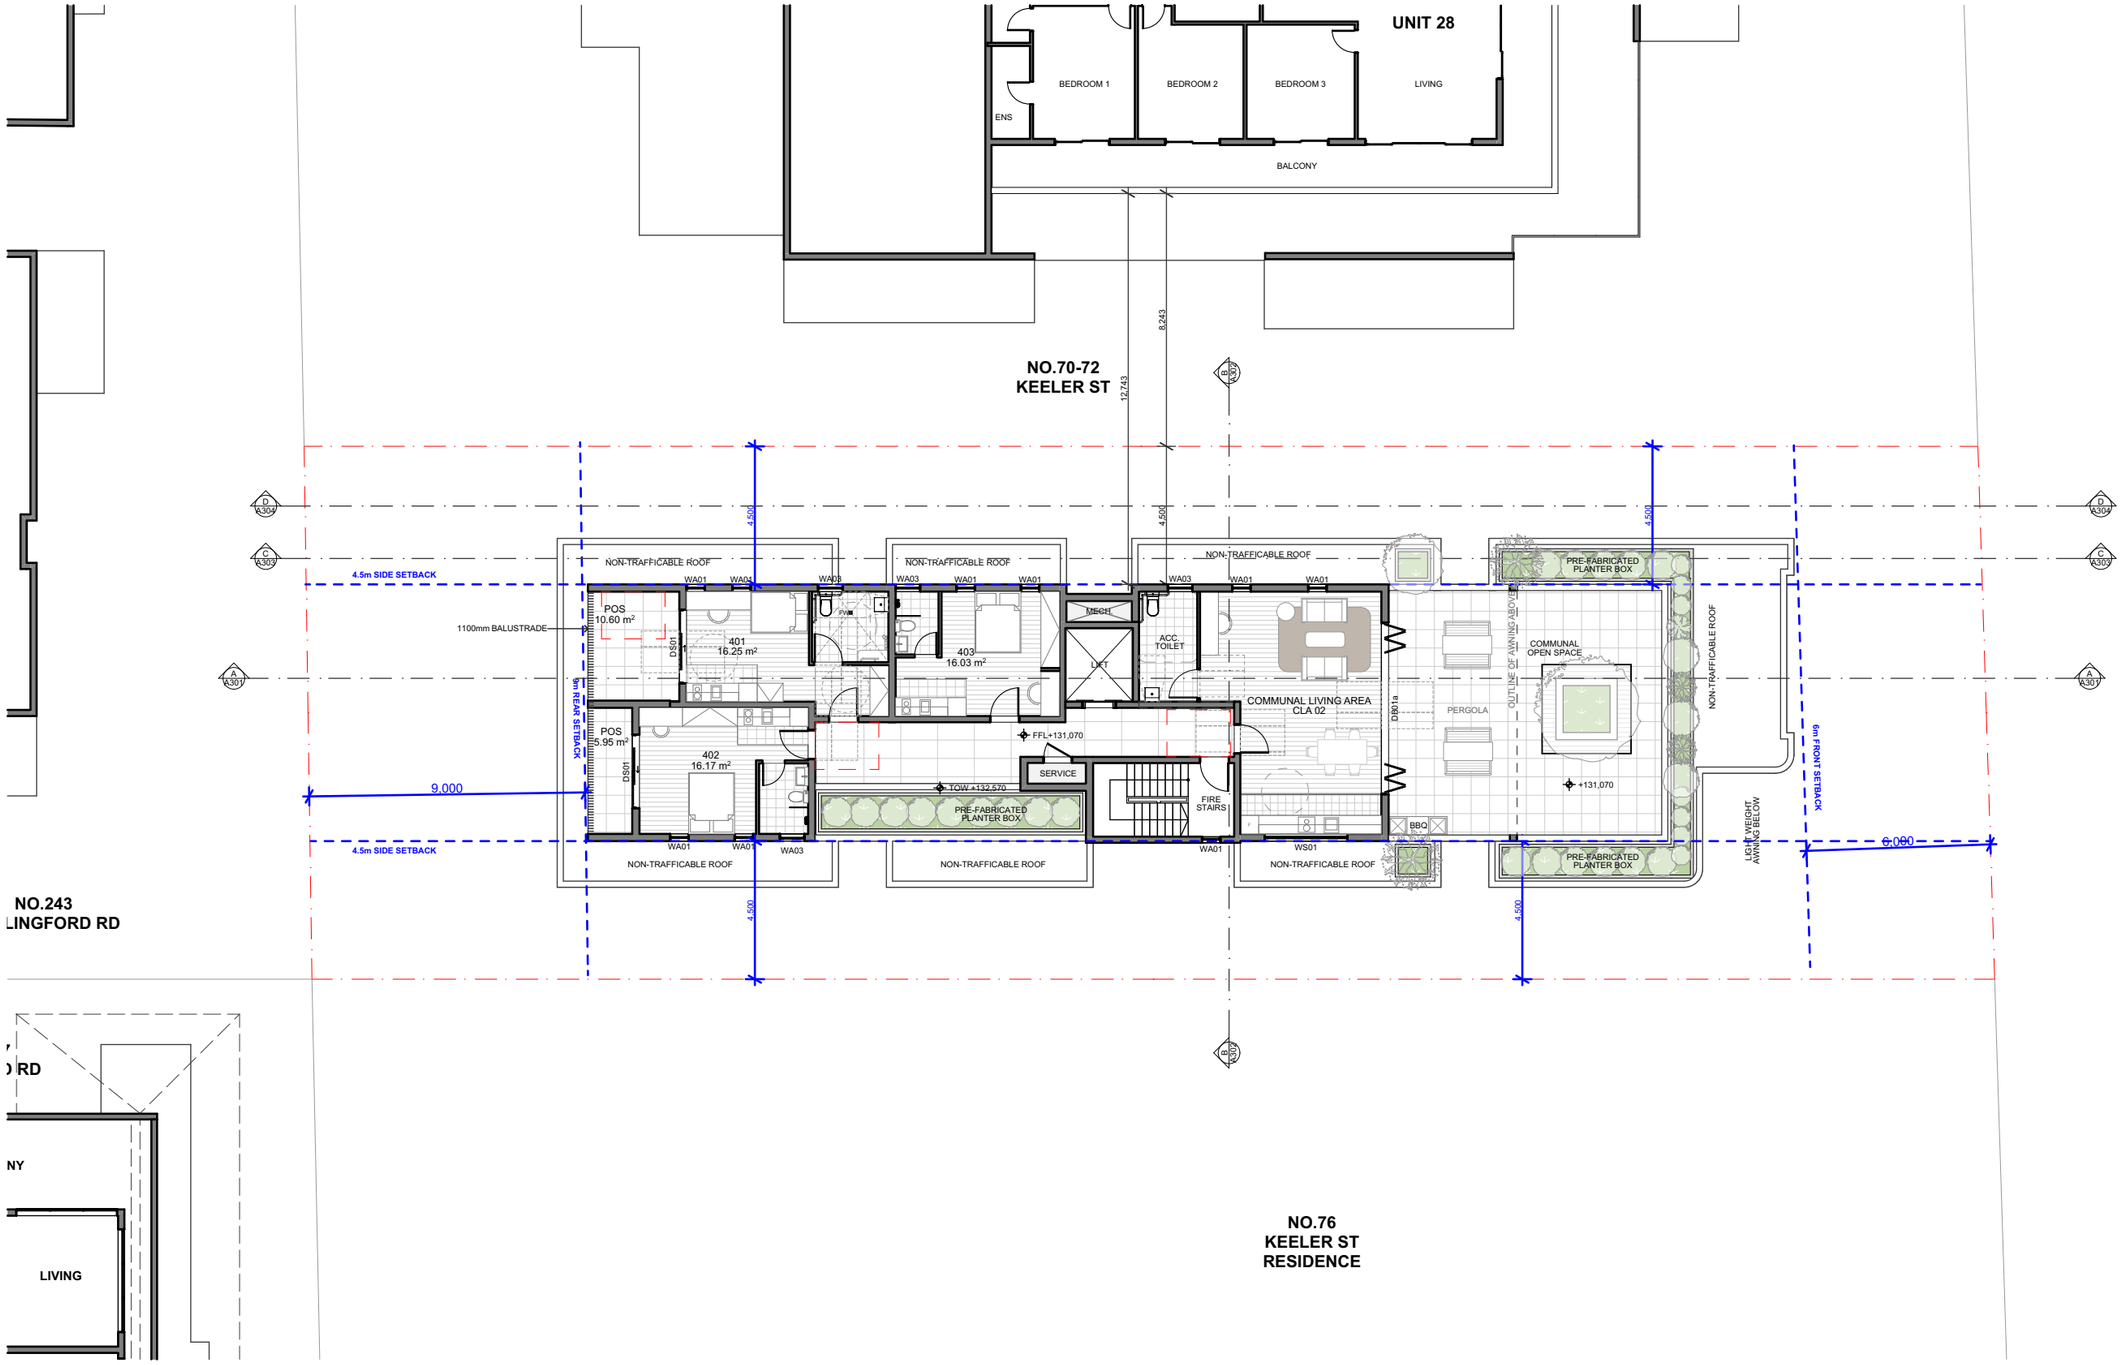

NOTE

The Builder shall check all dimensions and levels on site prior to construction. Notify any errors, discrepancies or omissions to the architect. Refer to written dimensions only. Do not scale drawings. Drawings shall not be used for construction purposes until issued for construction. This drawing reflects a design by Texco Design Pty Ltd and is to be used only for work when authorised in writing by Texco Design Pty Ltd.

All boundaries and contours are subject to survey drawing. All levels to Australian Height Data. It is the contractors responsibility to confirm all measurements on site and locations of any services prior to work on site.

All documents here within are subject to Australian Copyright Laws.

Project Partners

Refer to consultant documentation when directed

- Planning Consultant	- **Think Planners**
- Ecologist	- **SIA Ecological**
- BCA & Access	- **BIA**
- Arborist Consultant	- **NSW Trees**
- QS Consultant	- **Property & Building Assessment**
- Section J Consultant	- **AENEC**
- Civil Engineer	- **JCO Consultants**
- Stormwater Engineer	- **JCO Consultants**
- Landscape Designer	- **Concept**
- Traffic Engineer	- **Genesis Traffic**
- Land Surveyor	- **RGM**
- Geotechnical Engineer	- **STANTEC**
- Flood Engineer	- **HYDRACOR**

RevID	Transmittal Set Date	Approved by	Rev. Note
A	27/03/2024	T.Z	ISSUE FOR DA
B	16/01/2025	T.Z	ISSUE FOR S34
C	11/02/2025	T.Z	ISSUE FOR S34
D	03/03/2025		ISSUE FOR S34
E	13/03/2025	T.Z	ISSUE FOR S34
F	20/03/2025	T.Z	ISSUE FOR S34
G	19/09/2025		ISSUE FOR S34

Project Designer

TEXCO DESIGN
Nom Arch: NSW ARB 11348
E: office@texcodesign.com.au
P: +61 449 984 889

TRUE NORTH

Drawn | Checked	A.W I J.C |
Revision Date:	19/09/2025
Project NO.	2335
Project Status	S34
Client	MR BILLY CHEN
Site:	74 KEELER ST CARLINGFORD
Climate Zone	5
Wind Region	A

PAPER A3

1:200

DRAWING TITLE :

PLANS
LEVEL 4 PLAN

PROJECT NAME :

74 KEELER ST CARLINGFORD

REVISION NO. **G**

DRAWING NO. **A106**

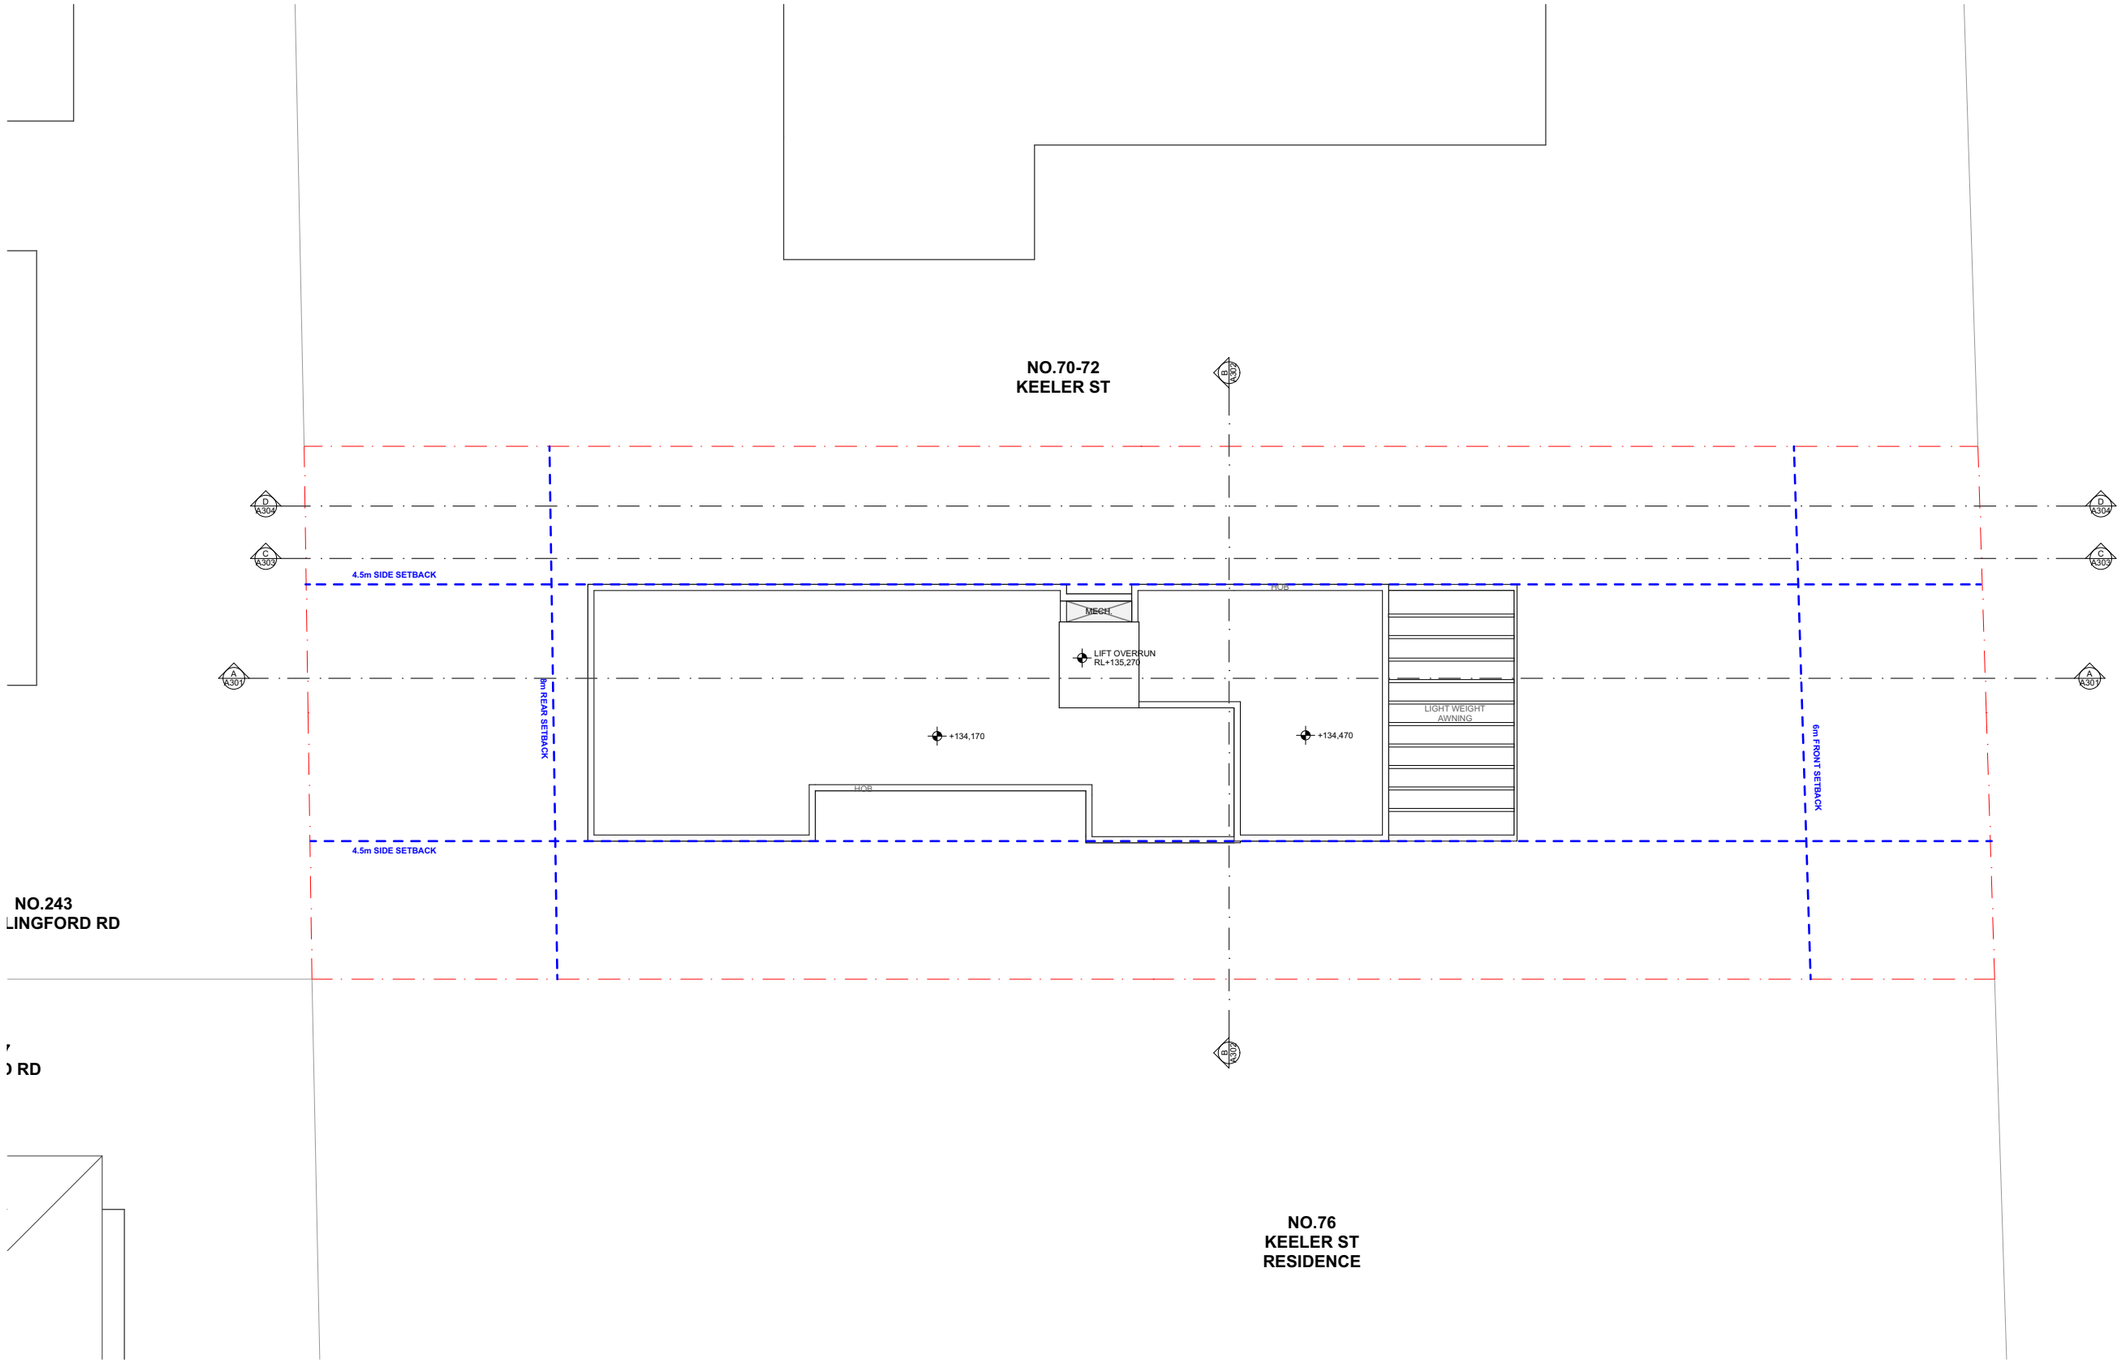

NOTE

The Builder shall check all dimensions and levels on site prior to construction. Notify any errors, discrepancies or omissions to the architect. Refer to written dimensions only. Do not scale drawings. Drawings shall not be used for construction purposes until issued for construction. This drawing reflects a design by Texco Design Pty Ltd and is to be used only for work when authorised in writing by Texco Design Pty Ltd.

All boundaries and contours are subject to survey drawing. All levels to Australian Height Data. It is the contractors responsibility to confirm all measurements on site and locations of any services prior to work on site.

All documents here within are subject to Australian Copyright Laws.

Project Partners

Refer to consultant documentation when directed

- Planning Consultant	- **Think Planners**
- Ecologist	- **BIA Ecological**
- BCA & Access	- **BIA**
- Arborist Consultant	- **NSW Trees**
- QS Consultant	- **Property & Building Assessment**
- Section J Consultant	- **AENEC**
- Civil Engineer	- **JCO Consultants**
- Stormwater Engineer	- **JCO Consultants**
- Landscape Designer	- **Conzept**
- Traffic Engineer	- **Genesis Traffic**
- Land Surveyor	- **RGM**
- Geotechnical Engineer	- **STANTEC**
- Flood Engineer	- **HYDRACOR**

RevID	Transmittal Set Date	Approved by	Rev. Note
A	27/03/2024	T.Z	ISSUE FOR DA
B	16/01/2025	T.Z	ISSUE FOR S34
C	11/02/2025	T.Z	ISSUE FOR S34
D	03/03/2025		ISSUE FOR S34
E	13/03/2025	T.Z	ISSUE FOR S34
F	20/03/2025	T.Z	ISSUE FOR S34
G	19/09/2025		ISSUE FOR S34

Project Designer

TEXCO DESIGN

Nom Arch: NSW ARB 11348

E: office@texcodesign.com.au P: +61 449 984 889

N

TRUE NORTH

Drawn | Checked	A.W | J.C |
Revision Date:	19/09/2025
Project NO.	2335
Project Status	S34
Client	MR BILLY CHEN
Site:	74 KEELER ST CARLINGFORD
Climate Zone	5
Wind Region	A

PAPER

A3

1:200

DRAWING TITLE :

PLANS
ROOF PLAN

PROJECT NAME :

74 KEELER ST CARLINGFORD

REVISION NO.

G

DRAWING NO.

A107

E-01 | -

SOUTH ELEVATION
1:200

E-02 | -

NORTH ELEVATION
1:200

NOTE

The Builder shall check all dimensions and levels on site prior to construction. Notify any errors, discrepancies or omissions to the architect. Refer to written dimensions only. Do not scale drawings. Drawings shall not be used for construction purposes until issued for construction. This drawing reflects a design by Texco Design Pty Ltd and is to be used only for work when authorised in writing by Texco Design Pty Ltd.

All boundaries and contours are subject to survey drawing. All levels to Australian Height Data. It is the contractors responsibility to confirm all measurements on site and locations of any services prior to work on site.

All documents here within are subject to Australian Copyright Laws.

Project Partners
Refer to consultant documentation when directed

- Planning Consultant	- **Think Planners**
- Ecologist	- **SIA Ecological**
- BCA & Access	- **BIA**
- Arborist Consultant	- **NSW Trees**
- QS Consultant	- **Property & Building Assessment**
- Section J Consultant	- **AEINEC**
- Civil Engineer	- **JCO Consultants**
- Stormwater Engineer	- **JCO Consultants**
- Landscape Designer	- **Conzept**
- Traffic Engineer	- **Genesis Traffic**
- Land Surveyor	- **RGM**
- Geotechnical Engineer	- **STANTEC**
- Flood Engineer	- **HYDRACOR**

RevID	Transmittal Set Date	Approved by	Rev. Note
A	27/03/2024	T.Z	ISSUE FOR DA
B	16/01/2025	T.Z	ISSUE FOR S34
C	11/02/2025	T.Z	ISSUE FOR S34
D	03/03/2025		ISSUE FOR S34
E	13/03/2025	T.Z	ISSUE FOR S34
F	20/03/2025	T.Z	ISSUE FOR S34
G	19/09/2025		ISSUE FOR S34

Project Designer

TEXCO DESIGN
Nom Arch: NSW ARB 11348
E: office@texcodesign.com.au
P: +61 449 984 889

TRUE NORTH

Drawn | Checked	A.W I J.C |
Revision Date:	19/09/2025
Project NO.	2335
Project Status	S34
Client	MR BILLY CHEN
Site:	74 KEELER ST CARLINGFORD
Climate Zone	5
Wind Region	A

PAPER
A3
1:200

DRAWING TITLE :
ELEVATION
NORTH & SOUTH ELEVATION

PROJECT NAME :
74 KEELER ST CARLINGFORD

REVISION NO.
G

DRAWING NO.
A201

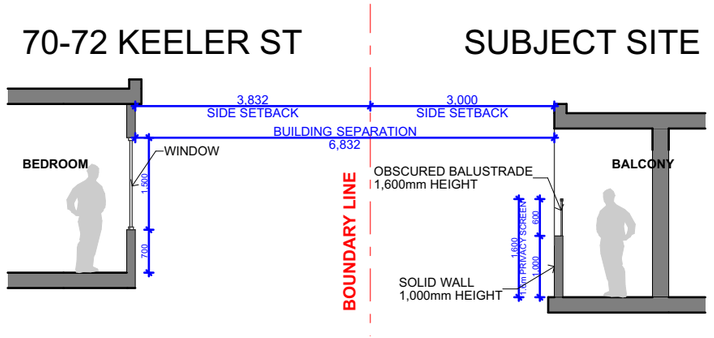

DS01 | -

SECTION DETAIL BUILDING SEPARATION

1:100

NOTE

The Builder shall check all dimensions and levels on site prior to construction. Notify any errors, discrepancies or omissions to the architect. Refer to written dimensions only. Do not scale drawings. Drawings shall not be used for construction purposes until issued for construction. This drawing reflects a design by Texco Design Pty Ltd and is to be used only for work when authorised in writing by Texco Design Pty Ltd.

All boundaries and contours are subject to survey drawing. All levels to Australian Height Data. It is the contractors responsibility to confirm all measurements on site and locations of any services prior to work on site.

All documents here within are subject to Australian Copyright Laws.

Project Partners

Refer to consultant documentation when directed

- Planning Consultant	- **Think Planners**
- Ecologist	- **SIA Ecological**
- BCA & Access	- **BIA**
- Arborist Consultant	- **NSW Trees**
- QS Consultant	- **Property & Building Assessment**
- Section J Consultant	- **JCDC**
- Civil Engineer	- **ACE Consultants**
- Stormwater Engineer	- **JCO Consultants**
- Landscape Designer	- **Concept**
- Traffic Engineer	- **Genesis Traffic**
- Land Surveyor	- **RGM**
- Geotechnical Engineer	- **STANTEC**
- Flood Engineer	- **HYDRACOR**

RevID	Transmittal Set Date	Approved by	Rev. Note
A	27/03/2024	T.Z	ISSUE FOR DA
B	16/01/2025	T.Z	ISSUE FOR S34
C	11/02/2025	T.Z	ISSUE FOR S34
D	03/03/2025		ISSUE FOR S34
E	13/03/2025	T.Z	ISSUE FOR S34
F	20/03/2025	T.Z	ISSUE FOR S34
G	19/09/2025		ISSUE FOR S34

Project Designer

TEXCO DESIGN

Nom Arch: NSW ARB 11348

E: office@texcodesign.com.au P: +61 449 984 889

TRUE NORTH

Drawn | Checked A.W I J.C |
Revision Date: 19/09/2025
Project NO. 2335
Project Status S34

Client MR BILLY CHEN
Site: 74 KEELER ST CARLINGFORD
Climate Zone 5
Wind Region A

PAPER A3

1:200, 1:100

DRAWING TITLE :

ELEVATION
EAST ELEVATION

PROJECT NAME :

74 KEELER ST CARLINGFORD

REVISION NO. G

DRAWING NO. A202

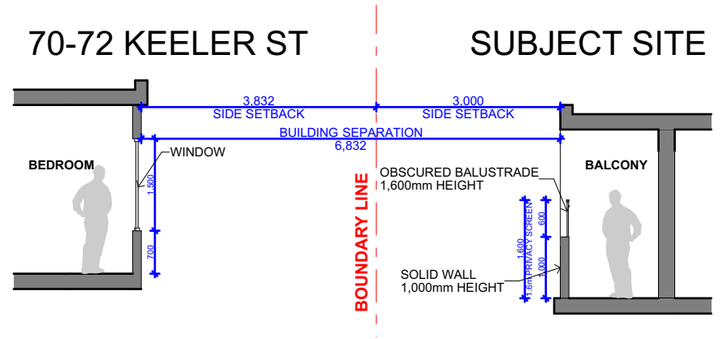

DS01 | -

SECTION DETAIL BUILDING SEPARATION

1:100

NOTE

The Builder shall check all dimensions and levels on site prior to construction. Notify any errors, discrepancies or omissions to the architect. Refer to written dimensions only. Do not scale drawings. Drawings shall not be used for construction purposes until issued for construction. This drawing reflects a design by Texco Design Pty Ltd and is to be used only for work when authorised in writing by Texco Design Pty Ltd.

All boundaries and contours are subject to survey drawing. All levels to Australian Height Data. It is the contractors responsibility to confirm all measurements on site and locations of any services prior to work on site.

All documents here within are subject to Australian Copyright Laws.

Project Partners

Refer to consultant documentation when directed

- Planning Consultant	- **Think Planners**
- Ecologist	- **SIA Ecological**
- BCA & Access	- **BIA**
- Arborist Consultant	- **NSW Trees**
- QS Consultant	- **Property & Building Assessment**
- Section J Consultant	- **JCDC**
- Civil Engineer	- **ADG Consultants**
- Stormwater Engineer	- **JCO Consultants**
- Landscape Designer	- **Concept**
- Traffic Engineer	- **Genesis Traffic**
- Land Surveyor	- **RGM**
- Geotechnical Engineer	- **STANTEC**
- Flood Engineer	- **HYDRACOR**

RevID	Transmittal Set Date	Approved by	Rev. Note
A	27/03/2024	T.Z	ISSUE FOR DA
B	16/01/2025	T.Z	ISSUE FOR S34
C	11/02/2025	T.Z	ISSUE FOR S34
D	03/03/2025		ISSUE FOR S34
E	13/03/2025	T.Z	ISSUE FOR S34
F	20/03/2025	T.Z	ISSUE FOR S34
G	19/09/2025		ISSUE FOR S34

Project Designer

TEXCO DESIGN

Nom Arch: NSW ARB 11348

E: office@texcodesign.com.au P: +61 449 984 889

TRUE NORTH

Drawn | Checked	A.W I J.C |
Revision Date:	19/09/2025
Project NO.	2335
Project Status	S34
Client	MR BILLY CHEN
Site:	74 KEELER ST CARLINGFORD
Climate Zone	5
Wind Region	A

PAPER A3

1:200, 1:100

DRAWING TITLE :

ELEVATION

WEST ELEVATION

PROJECT NAME :

74 KEELER ST CARLINGFORD

REVISION NO. **G**

DRAWING NO. **A203**

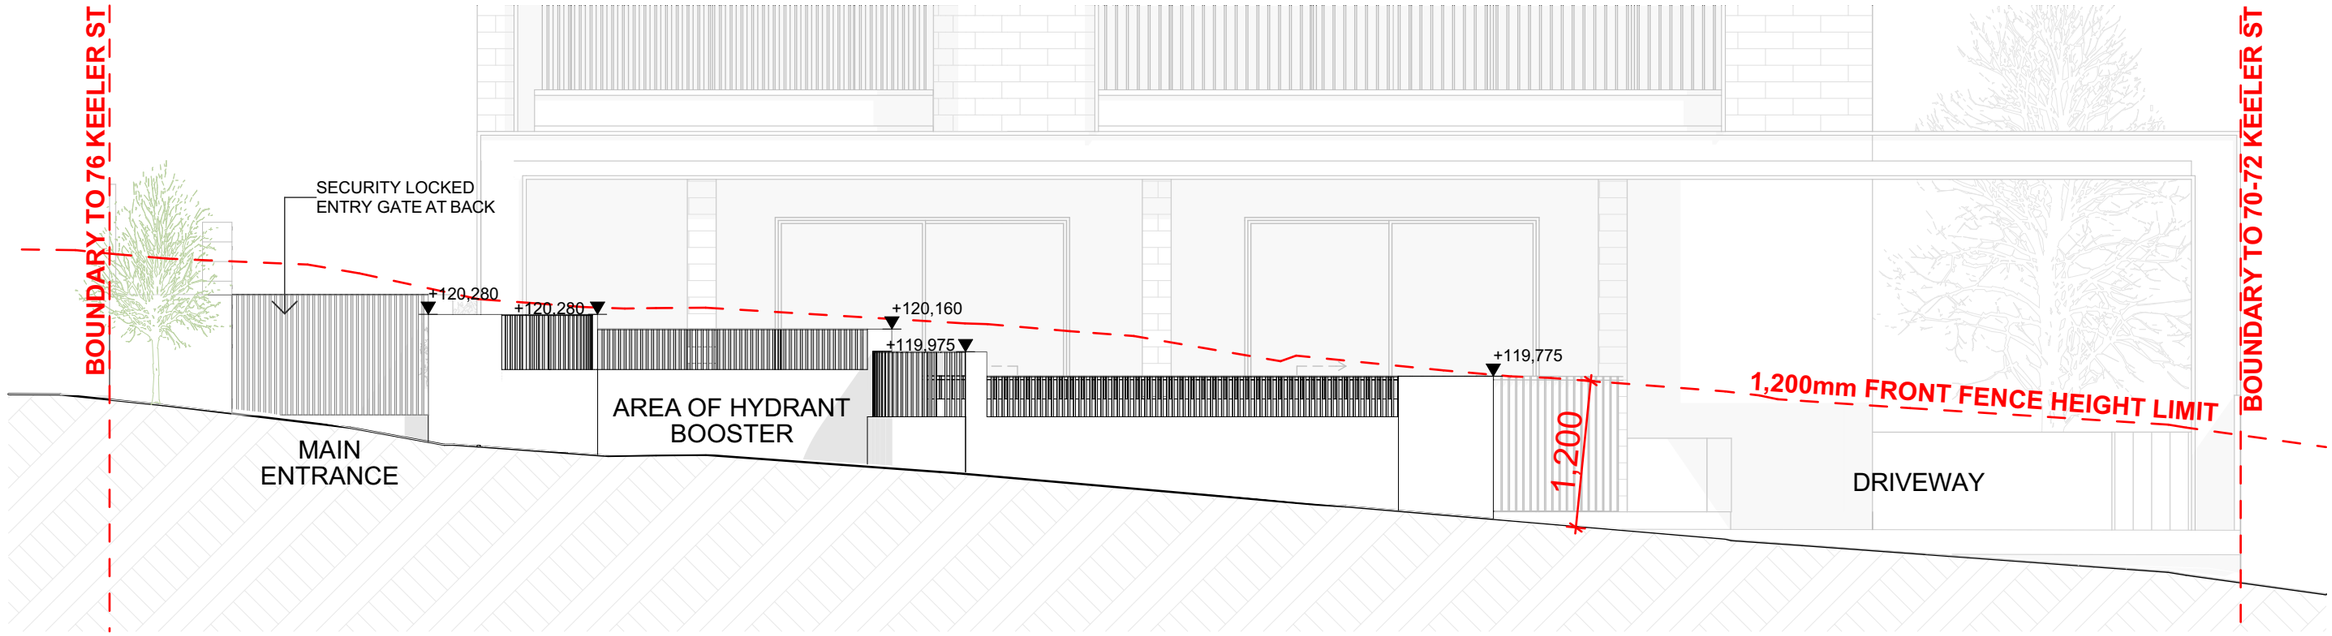

DCP PART 2.6 REQUIREMENT

ON SLOPING SITES, FRONT FENCES SHOULD VARY IN HEIGHT TO SUIT THE TOPOGRAPHY OF THE SITE UP TO A MAXIMUM HEIGHT OF 1.2 METRES.
FRONT FENCES SHOULD FORM A HORIZONTAL PLINTH WITH MINIMAL STEPPING.

NOTE

The Builder shall check all dimensions and levels on site prior to construction. Notify any errors, discrepancies or omissions to the architect. Refer to written dimensions only. Do not scale drawings. Drawings shall not be used for construction purposes until issued for construction. This drawing reflects a design by Texco Design Pty Ltd and is to be used only for work when authorised in writing by Texco Design Pty Ltd.

All boundaries and contours are subject to survey drawing. All levels to Australian Height Data. It is the contractors responsibility to confirm all measurements on site and locations of any services prior to work on site.

All documents here within are subject to Australian Copyright Laws.

Project Partners
Refer to consultant documentation when directed

- Planning Consultant	- **Think Planners**
- Ecologist	- **SIA Ecological**
- BCA & Access	- **BIA**
- Arborist Consultant	- **NSW Trees**
- QS Consultant	- **Property & Building Assessment**
- Section J Consultant	- **AENEC**
- Civil Engineer	- **JCO Consultants**
- Stormwater Engineer	- **JCO Consultants**
- Landscape Designer	- **Concept**
- Traffic Engineer	- **Genesis Traffic**
- Land Surveyor	- **RDM**
- Geotechnical Engineer	- **STANTEC**
- Flood Engineer	- **HYDRACOR**

RevID	Transmittal Set Date	Approved by	Rev. Note
B	16/01/2025	TZ	ISSUE FOR S34
C	11/02/2025	TZ	ISSUE FOR S34
D	03/03/2025		ISSUE FOR S34
E	13/03/2025	TZ	ISSUE FOR S34
F	20/03/2025	TZ	ISSUE FOR S34
G	19/09/2025		ISSUE FOR S34

Project Designer
TEXCO DESIGN
Nom Arch: NSW ARB 11348
E: office@texcodesign.com.au
P: +61 449 984 889

TRUE NORTH

Drawn | Checked A.W I J.C |
Revision Date: 19/09/2025
Project NO. 2335
Project Status S34

Client MR BILLY CHEN
Site: 74 KEELER ST CARLINGFORD
Climate Zone 5
Wind Region A

PAPER
A3
1:50

DRAWING TITLE :
ELEVATION
FRONT FENCE ELEVATION

PROJECT NAME :
74 KEELER ST CARLINGFORD

REVISION NO.
G

DRAWING NO.
A204

NOTE

The Builder shall check all dimensions and levels on site prior to construction. Notify any errors, discrepancies or omissions to the architect. Refer to written dimensions only. Do not scale drawings. Drawings shall not be used for construction purposes until issued for construction. This drawing reflects a design by Texco Design Pty Ltd and is to be used only for work when authorised in writing by Texco Design Pty Ltd.

All boundaries and contours are subject to survey drawing. All levels to Australian Height Data. It is the contractors responsibility to confirm all measurements on site and locations of any services prior to work on site.

All documents here within are subject to Australian Copyright Laws.

Project Partners

Refer to consultant documentation when directed

- Planning Consultant	- **Think Planners**
- Ecologist	- **SIA Ecological**
- BCA & Access	- **BIA**
- Arborist Consultant	- **NSW Trees**
- QS Consultant	- **Property & Building Assessment**
- Section J Consultant	- **AENEC**
- Civil Engineer	- **JCO Consultants**
- Stormwater Engineer	- **JCO Consultants**
- Landscape Designer	- **Conzept**
- Traffic Engineer	- **Genesis Traffic**
- Land Surveyor	- **RGM**
- Geotechnical Engineer	- **STANTEC**
- Flood Engineer	- **HYDRACOR**

RevID	Transmittal Set Date	Approved by	Rev. Note
A	27/03/2024	T.Z	ISSUE FOR DA
B	16/01/2025	T.Z	ISSUE FOR S34
C	11/02/2025	T.Z	ISSUE FOR S34
D	03/03/2025		ISSUE FOR S34
E	13/03/2025	T.Z	ISSUE FOR S34
F	20/03/2025	T.Z	ISSUE FOR S34
G	19/09/2025		ISSUE FOR S34

Project Designer

TEXCO DESIGN

Nom Arch: NSW ARB 11348

E: office@texcodesign.com.au P: +61 449 984 889

N

TRUE NORTH

Drawn | Checked	A.W I J.C |
Revision Date:	19/09/2025
Project NO.	2335
Project Status	S34
Client	MR BILLY CHEN
Site:	74 KEELER ST CARLINGFORD
Climate Zone	5
Wind Region	A

PAPER

A3

1:200

DRAWING TITLE :

SECTION

SECTION A

PROJECT NAME :

74 KEELER ST CARLINGFORD

REVISION NO.

G

DRAWING NO.

A301

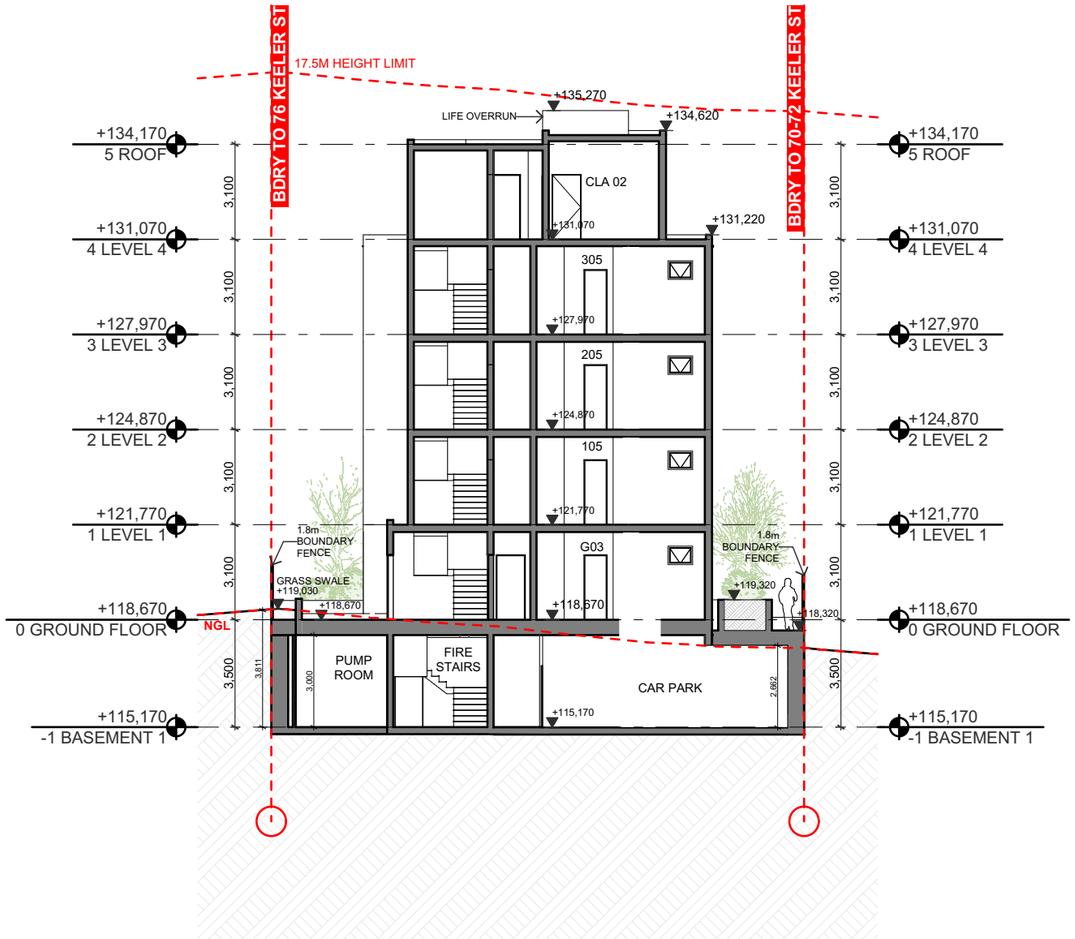

NOTE

The Builder shall check all dimensions and levels on site prior to construction. Notify any errors, discrepancies or omissions to the architect. Refer to written dimensions only. Do not scale drawings. Drawings shall not be used for construction purposes until issued for construction. This drawing reflects a design by Texco Design Pty Ltd and is to be used only for work when authorised in writing by Texco Design Pty Ltd.

All boundaries and contours are subject to survey drawing. All levels to Australian Height Data. It is the contractors responsibility to confirm all measurements on site and locations of any services prior to work on site.

All documents here within are subject to Australian Copyright Laws.

Project Partners

Refer to consultant documentation when directed

- Planning Consultant	- **Think Planners**
- Ecologist	- **SIA Ecological**
- BCA & Access	- **BIA**
- Arborist Consultant	- **NSW Trees**
- QS Consultant	- **Property & Building Assessment**
- Section J Consultant	- **AENEC**
- Civil Engineer	- **JCO Consultants**
- Stormwater Engineer	- **JCO Consultants**
- Landscape Designer	- **Concept**
- Traffic Engineer	- **Genesis Traffic**
- Land Surveyor	- **RGM**
- Geotechnical Engineer	- **STANTEC**
- Flood Engineer	- **HYDRACOR**

RevID	Transmittal Set Date	Approved by	Rev. Note
A	27/03/2024	T.Z	ISSUE FOR DA
B	16/01/2025	T.Z	ISSUE FOR S34
C	11/02/2025	T.Z	ISSUE FOR S34
D	03/03/2025		ISSUE FOR S34
E	13/03/2025	T.Z	ISSUE FOR S34
F	20/03/2025	T.Z	ISSUE FOR S34
G	19/09/2025		ISSUE FOR S34

Project Designer

TEXCO DESIGN
Nom Arch: NSW ARB 11348
E: office@texcodesign.com.au
P: +61 449 984 889

TRUE NORTH

Drawn | Checked	A.W I J.C |
Revision Date:	19/09/2025
Project NO.	2335
Project Status	S34
Client	MR BILLY CHEN
Site:	74 KEELER ST CARLINGFORD
Climate Zone	5
Wind Region	A

PAPER A3 1:200

DRAWING TITLE : SECTION
SECTION B

PROJECT NAME :
74 KEELER ST CARLINGFORD

REVISION NO. **G**

DRAWING NO. **A302**

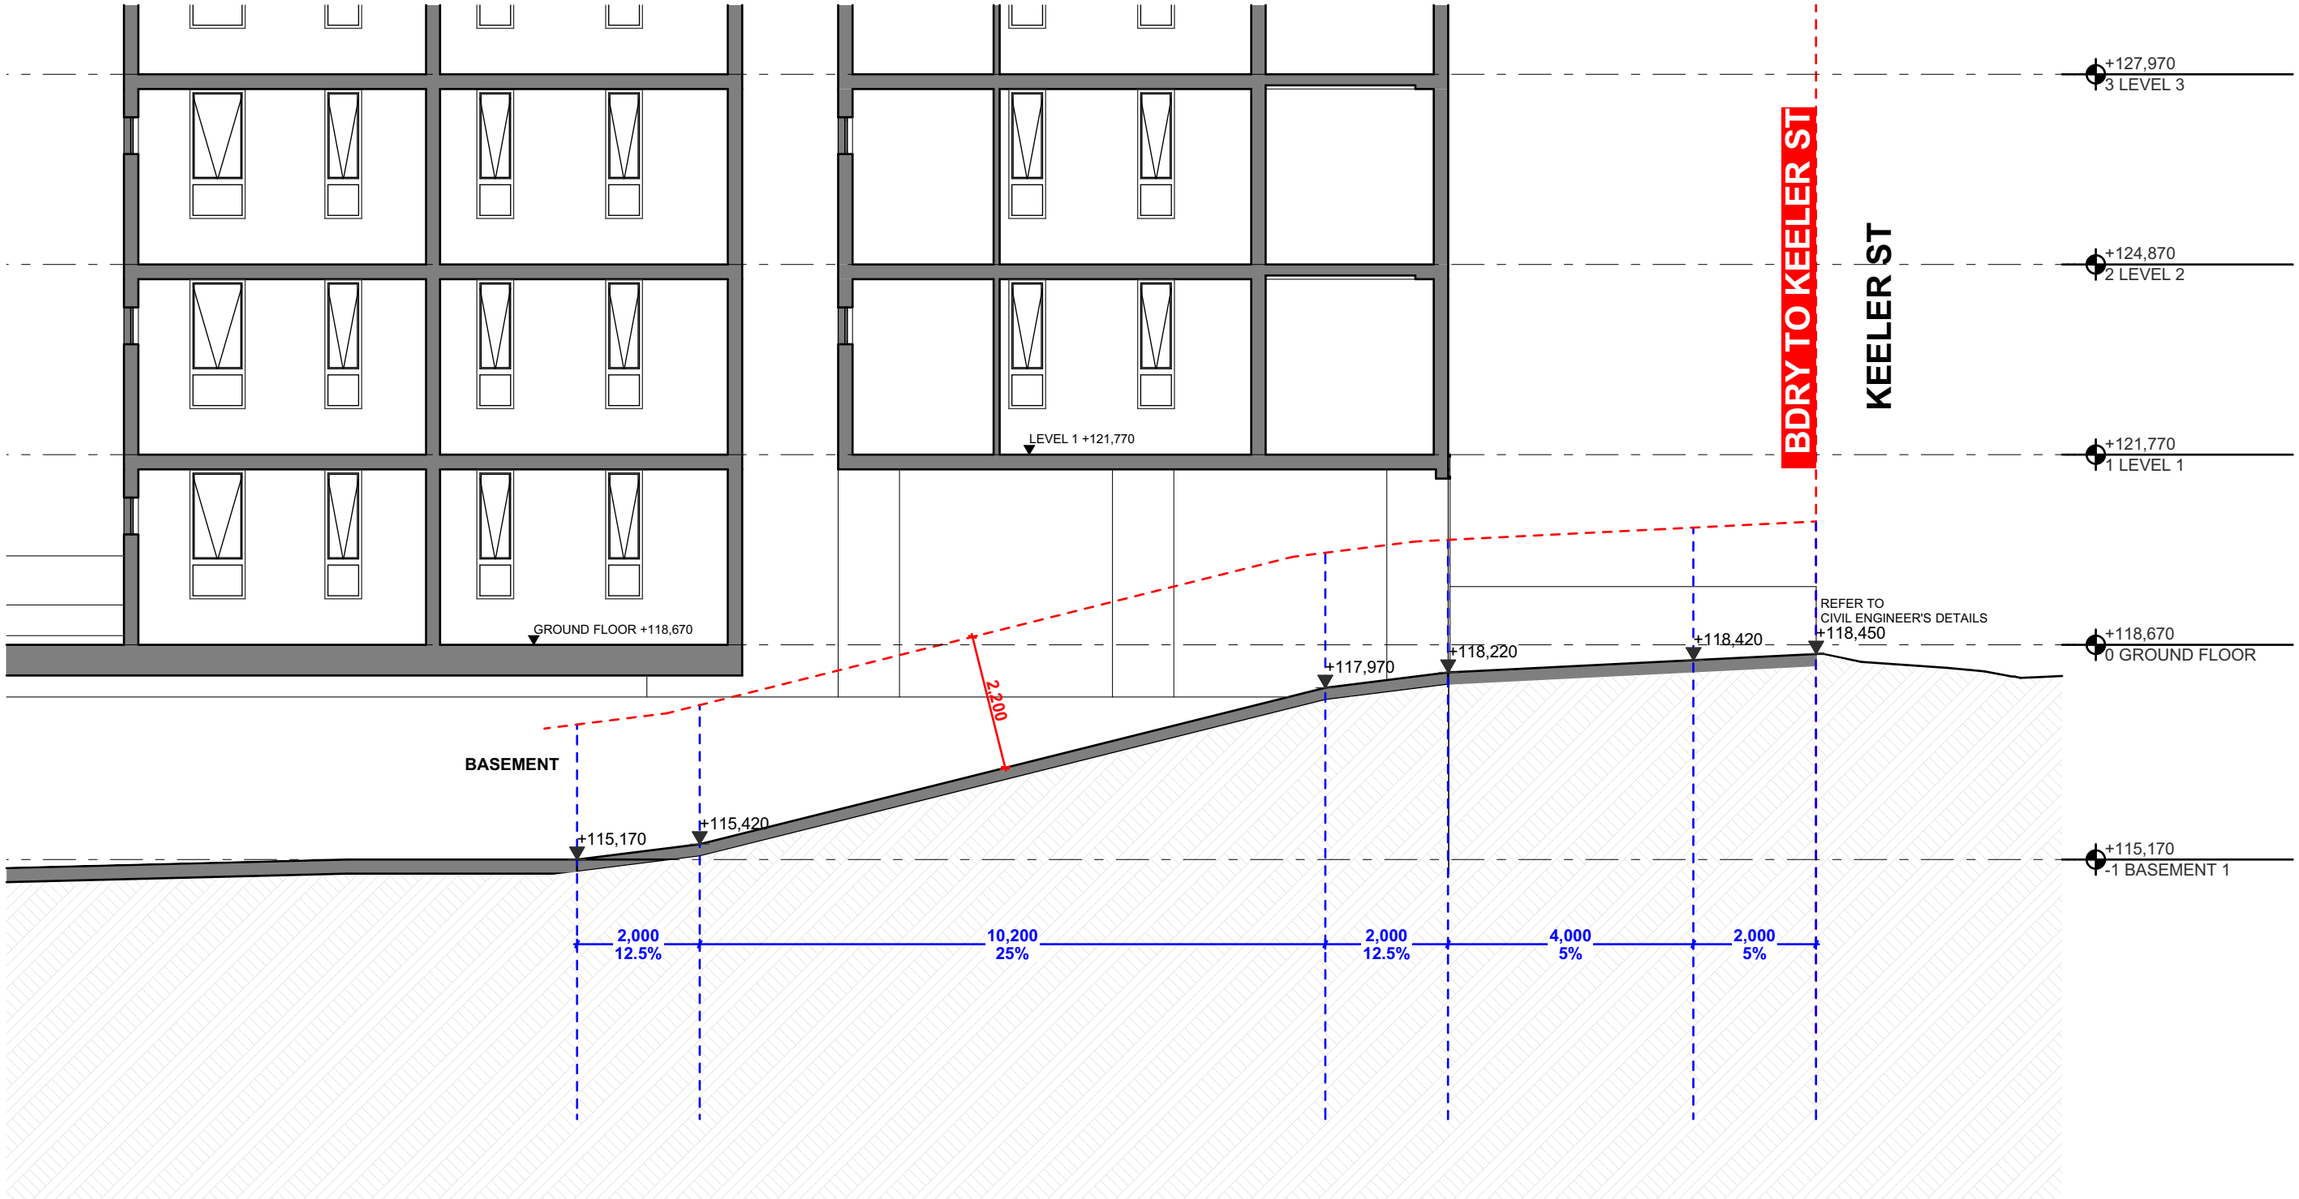

NOTE

The Builder shall check all dimensions and levels on site prior to construction. Notify any errors, discrepancies or omissions to the architect. Refer to written dimensions only. Do not scale drawings. Drawings shall not be used for construction purposes until issued for construction. This drawing reflects a design by Texco Design Pty Ltd and is to be used only for work when authorised in writing by Texco Design Pty Ltd.

All boundaries and contours are subject to survey drawing. All levels to Australian Height Data. It is the contractors responsibility to confirm all measurements on site and locations of any services prior to work on site.

All documents here within are subject to Australian Copyright Laws.

Project Partners

Refer to consultant documentation when directed

- Planning Consultant	- **Think Planners**
- Ecologist	- **SIA Ecological**
- BCA & Access	- **BIA**
- Arborist Consultant	- **NSW Trees**
- QS Consultant	- **Property & Building Assessment**
- Section J Consultant	- **AENEC**
- Civil Engineer	- **JCO Consultants**
- Stormwater Engineer	- **JCO Consultants**
- Landscape Designer	- **Concept**
- Traffic Engineer	- **Genesis Traffic**
- Land Surveyor	- **RGM**
- Geotechnical Engineer	- **STANTEC**
- Flood Engineer	- **HYDRACOR**

RevID	Transmittal Set Date	Approved by	Rev. Note
A	27/03/2024	T.Z	ISSUE FOR DA
B	16/01/2025	T.Z	ISSUE FOR S34
C	11/02/2025	T.Z	ISSUE FOR S34
D	03/03/2025		ISSUE FOR S34
E	13/03/2025	T.Z	ISSUE FOR S34
F	20/03/2025	T.Z	ISSUE FOR S34
G	19/09/2025		ISSUE FOR S34

Project Designer

TEXCO DESIGN
Nom Arch: NSW ARB 11348
E: office@texcodesign.com.au
P: +61 449 984 889

TRUE NORTH

Drawn | Checked	A.W | J.C |
Revision Date:	19/09/2025
Project NO.	2335
Project Status	S34
Client	MR BILLY CHEN
Site:	74 KEELER ST CARLINGFORD
Climate Zone	5
Wind Region	A

PAPER

A3

1:100

DRAWING TITLE :

SECTION
SECTION C (RAMP SECTION)

PROJECT NAME :

74 KEELER ST CARLINGFORD

REVISION NO.

G

DRAWING NO.

A303

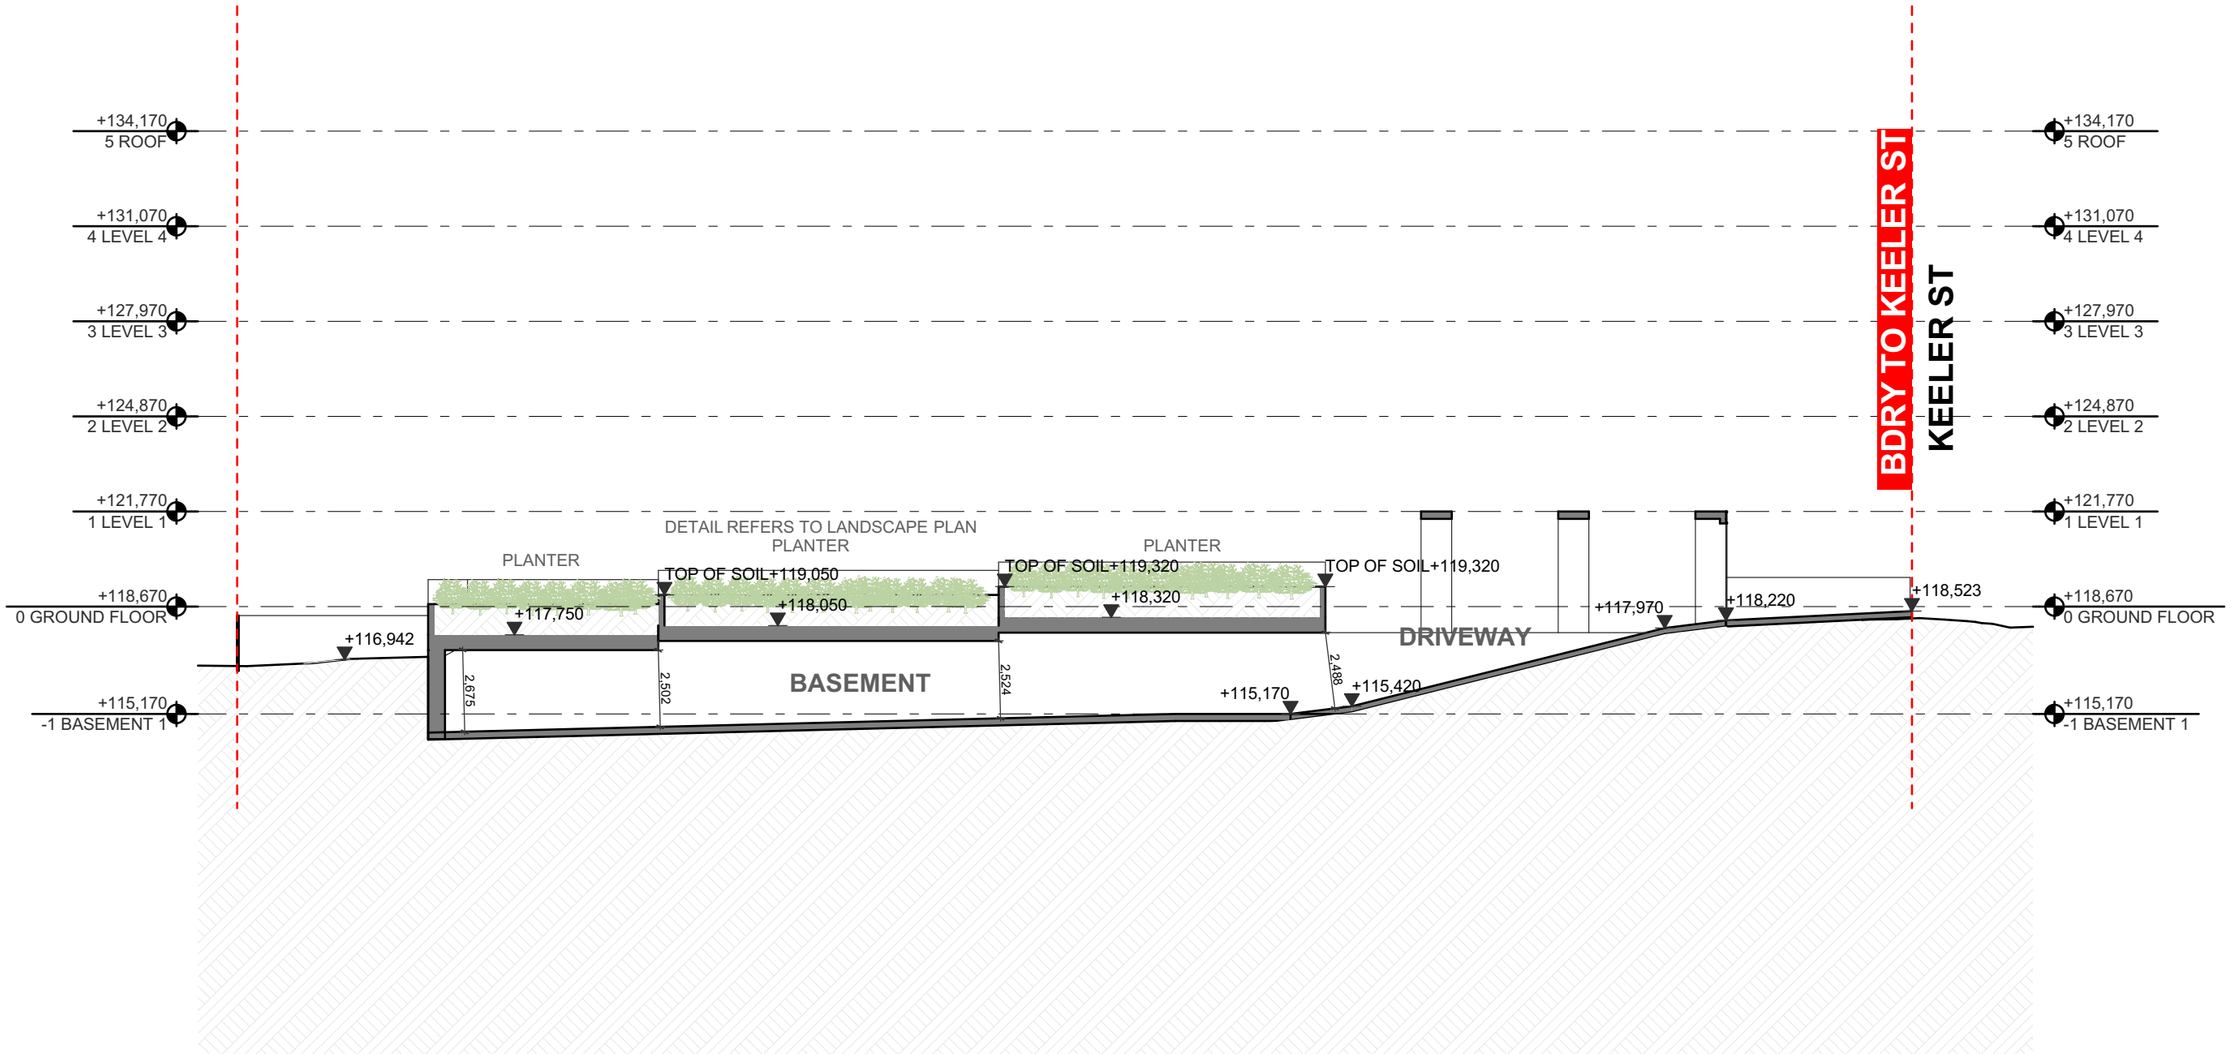

NOTE

The Builder shall check all dimensions and levels on site prior to construction. Notify any errors, discrepancies or omissions to the architect. Refer to written dimensions only. Do not scale drawings. Drawings shall not be used for construction purposes until issued for construction. This drawing reflects a design by Texco Design Pty Ltd and is to be used only for work when authorised in writing by Texco Design Pty Ltd.

All boundaries and contours are subject to survey drawing. All levels to Australian Height Data. It is the contractors responsibility to confirm all measurements on site and locations of any services prior to work on site.

All documents here within are subject to Australian Copyright Laws.

Project Partners

Refer to consultant documentation when directed

- Planning Consultant	- **Think Planners**
- Ecologist	- **SIA Ecological**
- BCA & Access	- **BIA**
- Arborist Consultant	- **NSW Trees**
- QS Consultant	- **Property & Building Assessment**
- Section J Consultant	- **AENEC**
- Civil Engineer	- **JCO Consultants**
- Stormwater Engineer	- **JCO Consultants**
- Landscape Designer	- **Concept**
- Traffic Engineer	- **Genesis Traffic**
- Land Surveyor	- **RGM**
- Geotechnical Engineer	- **STANTEC**
- Flood Engineer	- **HYDRACOR**

RevID	Transmittal Set Date	Approved by	Rev. Note
C	11/02/2025	T.Z	ISSUE FOR S34
D	03/03/2025		ISSUE FOR S34
E	13/03/2025	T.Z	ISSUE FOR S34
F	20/03/2025	T.Z	ISSUE FOR S34
G	19/09/2025		ISSUE FOR S34

Project Designer

TEXCO DESIGN

Nom Arch: NSW ARB 11348

E: office@texcodesign.com.au P: +61 449 984 889

N

TRUE NORTH

Drawn | Checked	A.W I J.C |
Revision Date:	19/09/2025
Project NO.	2335
Project Status	S34
Client	MR BILLY CHEN
Site:	74 KEELER ST CARLINGFORD
Climate Zone	5
Wind Region	A

PAPER

A3

1:200

DRAWING TITLE :

SECTION

SECTION D (SIDE SECTION DETAIL)

PROJECT NAME :

74 KEELER ST CARLINGFORD

REVISION NO.

G

DRAWING NO.

A304

MATERIAL SCHEDULE

1 BRICK
AUSTRAL - EVERYDAY LIFE
ESCAPE OR SIMILAR LOOK

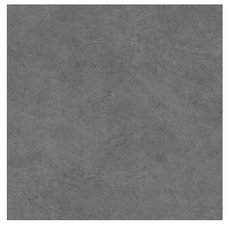

2 PAINT FINISH
POLISHED CONCRETE
LOOK OR SIMILAR

3 PAINT FINISH
DULUX
NATURAL WHITE

4 PAINT FINISH
DULUX
MONUMENT OR SIMILAR

5 VERTICAL BLADE
ALUMINIUM BALUSTRADE

6 ALUMINIUM FRAMED
WINDOWS & DOORS
POWDER COATED BLACK
OR SIMILAR

7 PRE-FABRICATED
PLANTER BOX

SOUTH ELEVATION
1:250

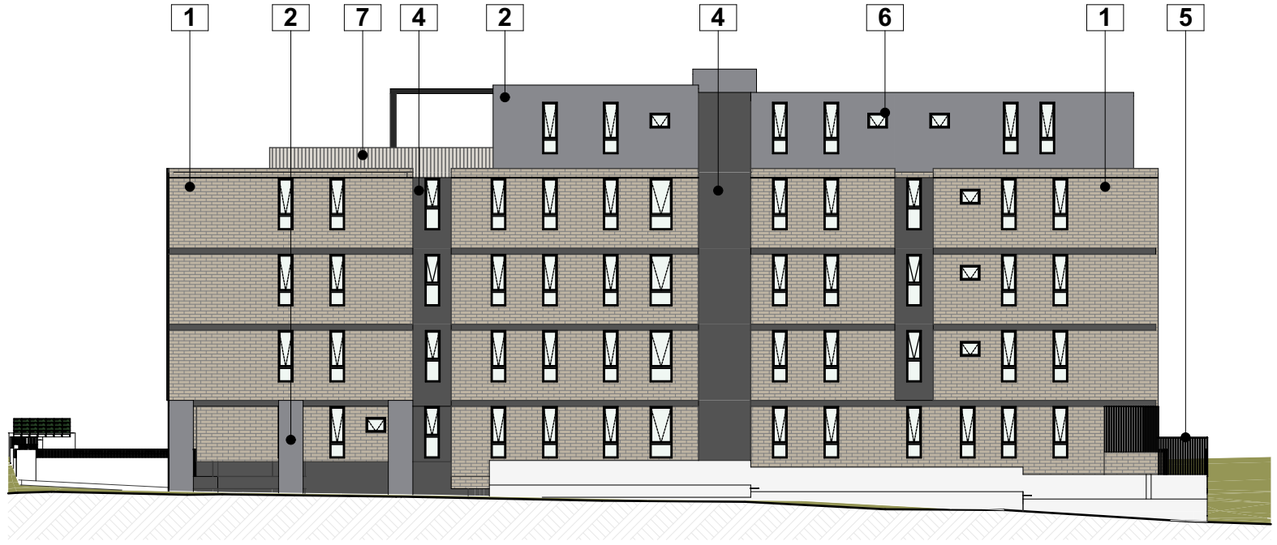

EAST ELEVATION
1:250

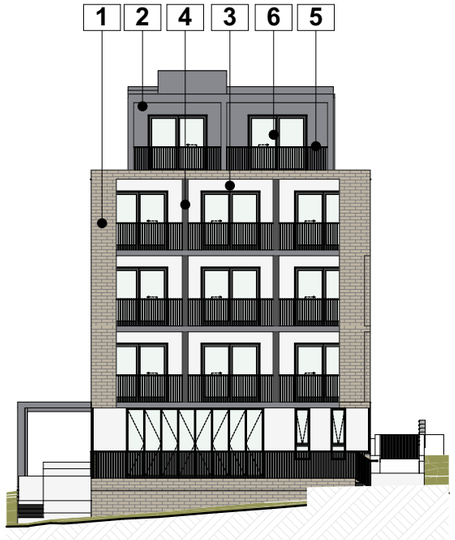

NORTH ELEVATION
1:250

WEST ELEVATION
1:250

NOTE
The Builder shall check all dimensions and levels on site prior to construction. Notify any errors, discrepancies or omissions to the architect. Refer to written dimensions only. Do not scale drawings. Drawings shall not be used for construction purposes until issued for construction. This drawing reflects a design by Texco Design Pty Ltd and is to be used only for work when authorised in writing by Texco Design Pty Ltd.

All boundaries and contours are subject to survey drawing. All levels to Australian Height Data. It is the contractors responsibility to confirm all measurements on site and locations of any services prior to work on site.

All documents here within are subject to Australian Copyright Laws.

Project Partners
Refer to consultant documentation when directed

- Planning Consultant	- **Think Planners**
- Ecologist	- **SIA Ecological**
- BCA & Access	- **BIA**
- Arborist Consultant	- **NSW Trees**
- QS Consultant	- **Property & Building Assessment**
- Section J Consultant	- **AEINEC**
- Civil Engineer	- **JCO Consultants**
- Stormwater Engineer	- **JCO Consultants**
- Landscape Designer	- **Concept**
- Traffic Engineer	- **Genesis Traffic**
- Land Surveyor	- **RGM**
- Geotechnical Engineer	- **STANTEC**
- Flood Engineer	- **HYDRACOR**

RevID	Transmittal Set Date	Approved by	Rev. Note
A	27/03/2024	T.Z	ISSUE FOR DA
B	16/01/2025	T.Z	ISSUE FOR S34
C	11/02/2025	T.Z	ISSUE FOR S34
D	3/03/2025		ISSUE FOR S34
E	13/03/2025	T.Z	ISSUE FOR S34
F	20/03/2025	T.Z	ISSUE FOR S34

Project Designer
TEXCO DESIGN
Nom Arch: NSW ARB 11348
E: office@texcodesign.com.au
P: +61 449 984 889

TRUE NORTH

Drawn | Checked	A.W I J.C |
Revision Date:	20/03/2025
Project NO.	2335
Project Status	S34
Client	MR BILLY CHEN
Site:	74 KEELER ST CARLINGFORD
Climate Zone	5
Wind Region	A

PAPER A3 **1:250**

DRAWING TITLE :
SCHEDULE
MATERIAL SCHEDULE

PROJECT NAME :
74 KEELER ST CARLINGFORD

REVISION NO. **F**

DRAWING NO. **A401**

DOOR LIST					
ID	DB01	DB01a	DE01	DF01	DS01
TYPE	GLAZED BI-FOLD DOOR	GLAZED BI-FOLD DOOR	GLAZED FRONT DOOR WITH SIDELIGHT	EGRESS DOOR	GLAZED SLIDING DOOR
NOMINAL W x H	5,600×2,860	5,600×3,200	1,400×2,400	920×2,100	2,400×2,400
PLAN		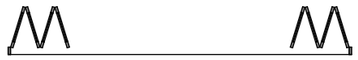	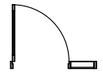		
ELEVATION	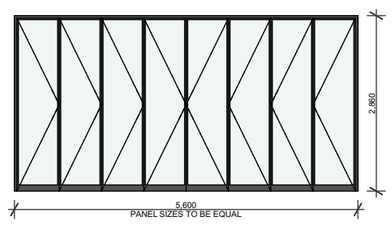	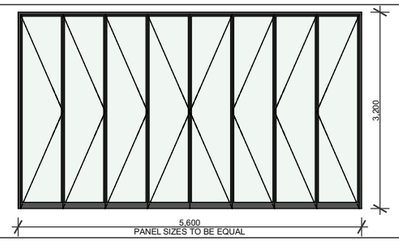	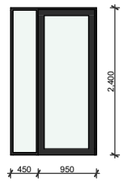	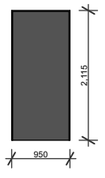	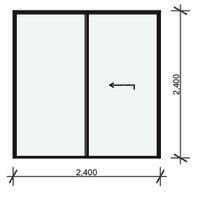
QUANTITY	1	1	1	1	22
MATERIAL / FRAME COLOUR	ALUMINIUM, POWDERCOATED BLACK OR SIMILAR	ALUMINIUM, POWDERCOATED BLACK OR SIMILAR	ALUMINIUM, POWDERCOATED BLACK OR SIMILAR	ALUMINIUM, POWDERCOATED BLACK OR SIMILAR	ALUMINIUM, POWDERCOATED BLACK OR SIMILAR

NOTE

The Builder shall check all dimensions and levels on site prior to construction. Notify any errors, discrepancies or omissions to the architect. Refer to written dimensions only. Do not scale drawings. Drawings shall not be used for construction purposes until issued for construction. This drawing reflects a design by Texco Design Pty Ltd and is to be used only for work when authorised in writing by Texco Design Pty Ltd.

All boundaries and contours are subject to survey drawing. All levels to Australian Height Data. It is the contractors responsibility to confirm all measurements on site and locations of any services prior to work on site.

All documents here within are subject to Australian Copyright Laws.

Project Partners

Refer to consultant documentation when directed

- Planning Consultant	- **Think Planners**
- Ecologist	- **SIA Ecological**
- BCA & Access	- **BIA**
- Arborist Consultant	- **NSW Trees**
- QS Consultant	- **Property & Building Assessment**
- Section J Consultant	- **AENEC**
- Civil Engineer	- **JCO Consultants**
- Stormwater Engineer	- **JCO Consultants**
- Landscape Designer	- **Conzept**
- Traffic Engineer	- **Genesis Traffic**
- Land Surveyor	- **RGM**
- Geotechnical Engineer	- **STANTEC**
- Flood Engineer	- **HYDRACOR**

RevID	Transmittal Set Date	Approved by	Rev. Note
A	27/03/2024	T.Z	ISSUE FOR DA
B	16/01/2025	T.Z	ISSUE FOR S34
C	11/02/2025	T.Z	ISSUE FOR S34
D	3/03/2025		ISSUE FOR S34
E	13/03/2025	T.Z	ISSUE FOR S34
F	20/03/2025	T.Z	ISSUE FOR S34

Project Designer

TEXCO DESIGN

Nom Arch: NSW ARB 11348

E: office@texcodesign.com.au P: +61 449 984 889

TRUE NORTH

Drawn | Checked A.W I J.C |
Revision Date: 20/03/2025
Project NO. 2335
Project Status S34

Client MR BILLY CHEN
Site: 74 KEELER ST CARLINGFORD
Climate Zone 5
Wind Region A

PAPER

A3

DRAWING TITLE :

SCHEDULE
DOORS SCHEDULE

PROJECT NAME :

74 KEELER ST CARLINGFORD

REVISION NO.

F

DRAWING NO.

A402

WINDOW LIST				
ID	WA01	WA02	WA03	WS01
TYPE	AWNING WINDOW	AWNING WINDOW	HIGH LIGHT AWNING WINDOW	SPLASH BACK WINDOW
NOMINAL W x H	600×2,100	900×2,100	800×600	2,700×600
NOMINAL SILL HEIGHT	750	750	1,800	1,200
PLAN				
ELEVATION	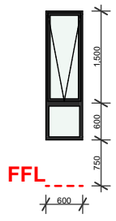	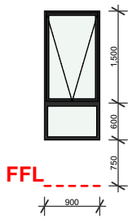	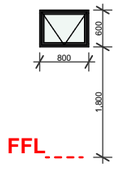	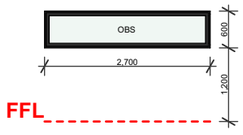
QUANTITY	92	4	39	2
MATERIAL / FRAME COLOUR	ALUMINIUM, POWDER-COATED BLACK OR SIMILAR	ALUMINIUM, POWDER-COATED BLACK OR SIMILAR	ALUMINIUM, POWDER-COATED BLACK OR SIMILAR	ALUMINIUM, POWDER-COATED BLACK OR SIMILAR

NOTE

The Builder shall check all dimensions and levels on site prior to construction. Notify any errors, discrepancies or omissions to the architect. Refer to written dimensions only. Do not scale drawings. Drawings shall not be used for construction purposes until issued for construction. This drawing reflects a design by Texco Design Pty Ltd and is to be used only for work when authorised in writing by Texco Design Pty Ltd.

All boundaries and contours are subject to survey drawing. All levels to Australian Height Data. It is the contractors responsibility to confirm all measurements on site and locations of any services prior to work on site.

All documents here within are subject to Australian Copyright Laws.

Project Partners

Refer to consultant documentation when directed

- Planning Consultant	- **Think Planners**
- Ecologist	- **SIA Ecological**
- BCA & Access	- **BIA**
- Arborist Consultant	- **NSW Trees**
- QS Consultant	- **Property & Building Assessment**
- Section J Consultant	- **AENEC**
- Civil Engineer	- **JCO Consultants**
- Stormwater Engineer	- **JCO Consultants**
- Landscape Designer	- **Conzept**
- Traffic Engineer	- **Genesis Traffic**
- Land Surveyor	- **RGM**
- Geotechnical Engineer	- **STANTEC**
- Flood Engineer	- **HYDRACOR**

RevID	Transmittal Set Date	Approved by	Rev. Note
A	27/03/2024	T.Z	ISSUE FOR DA
B	16/01/2025	T.Z	ISSUE FOR S34
C	11/02/2025	T.Z	ISSUE FOR S34
D	3/03/2025		ISSUE FOR S34
E	13/03/2025	T.Z	ISSUE FOR S34
F	20/03/2025	T.Z	ISSUE FOR S34

Project Designer

TEXCO DESIGN

Nom Arch: NSW ARB 11348

E: office@texcodesign.com.au P: +61 449 984 889

TRUE NORTH

Drawn | Checked A.W I J.C |
Revision Date: 20/03/2025
Project NO. 2335
Project Status S34

Client MR BILLY CHEN
Site: 74 KEELER ST CARLINGFORD
Climate Zone 5
Wind Region A

PAPER

A3

DRAWING TITLE :

SCHEDULE
WINDOWS SCHEDULE

PROJECT NAME :

74 KEELER ST CARLINGFORD

REVISION NO.

F

DRAWING NO.

A403

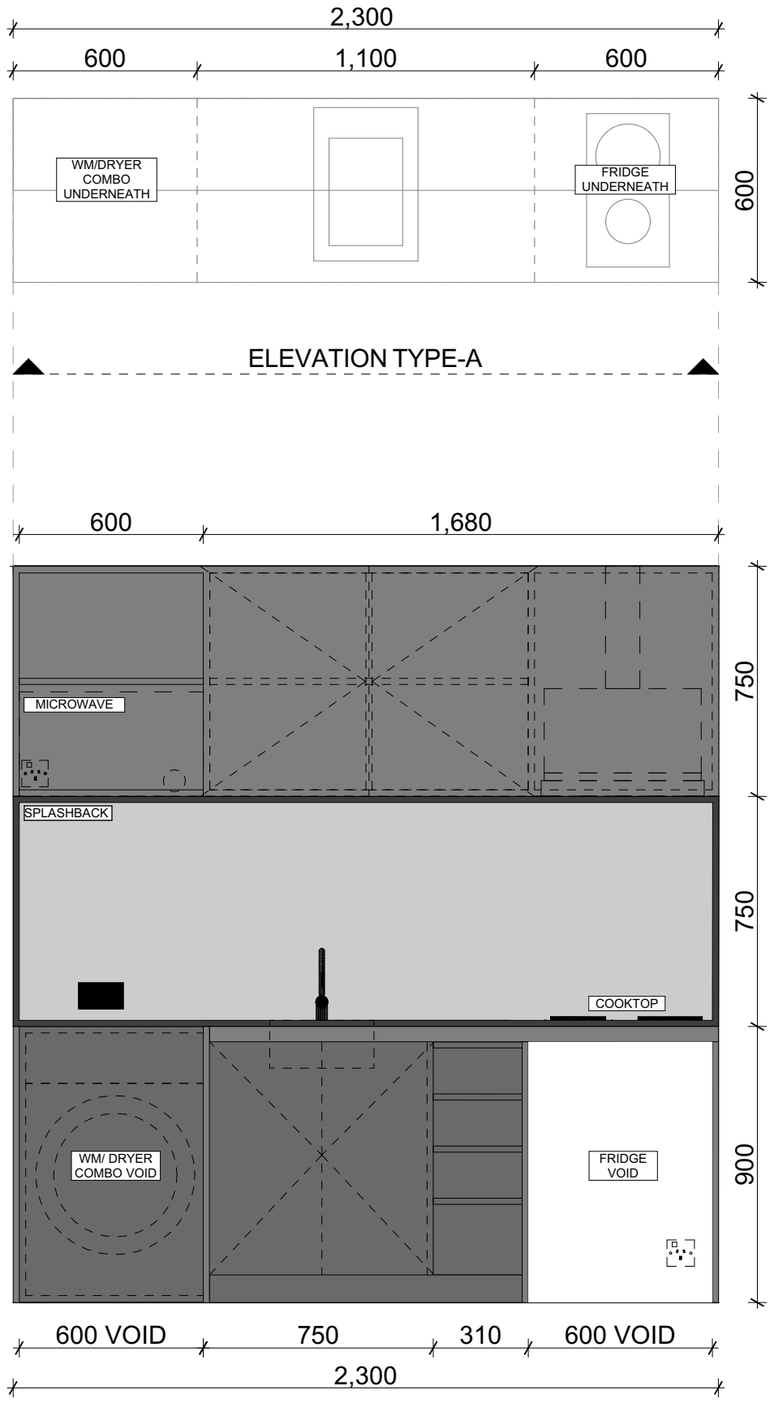

NOTE

The Builder shall check all dimensions and levels on site prior to construction. Notify any errors, discrepancies or omissions to the architect. Refer to written dimensions only. Do not scale drawings. Drawings shall not be used for construction purposes until issued for construction. This drawing reflects a design by Texco Design Pty Ltd and is to be used only for work when authorised in writing by Texco Design Pty Ltd.

All boundaries and contours are subject to survey drawing. All levels to Australian Height Data. It is the contractors responsibility to confirm all measurements on site and locations of any services prior to work on site.

All documents here within are subject to Australian Copyright Laws.

Project Partners
Refer to consultant documentation when directed

- Planning Consultant	- **Think Planners**
- Ecologist	- **SIA Ecological**
- BCA & Access	- **BIA**
- Arborist Consultant	- **NSW Trees**
- QS Consultant	- **Property & Building Assessment**
- Section J Consultant	- **AENEC**
- Civil Engineer	- **JCO Consultants**
- Stormwater Engineer	- **JCO Consultants**
- Landscape Designer	- **Concept**
- Traffic Engineer	- **Genesis Traffic**
- Land Surveyor	- **RGM**
- Geotechnical Engineer	- **STANTEC**
- Flood Engineer	- **HYDRACOR**

RevID	Transmittal Set Date	Approved by	Rev. Note
A	27/03/2024	T.Z	ISSUE FOR DA
B	16/01/2025	T.Z	ISSUE FOR S34
C	11/02/2025	T.Z	ISSUE FOR S34
D	3/03/2025		ISSUE FOR S34
E	13/03/2025	T.Z	ISSUE FOR S34
F	20/03/2025	T.Z	ISSUE FOR S34

Project Designer
TEXCO DESIGN
Nom Arch: NSW ARB 11348
E: office@texcodesign.com.au
P: +61 449 984 889

TRUE NORTH

Drawn | Checked	A.W I J.C |
Revision Date:	20/03/2025
Project NO.	2335
Project Status	S34
Client	MR BILLY CHEN
Site:	74 KEELER ST CARLINGFORD
Climate Zone	5
Wind Region	A

PAPER A3 1:20

DRAWING TITLE :
SCHEDULE
TYPICAL KITCHEN DETAILS

PROJECT NAME :
74 KEELER ST CARLINGFORD

REVISION NO. **F**

DRAWING NO. **A404**