SUBSET ID & NAME	DRAWING NO.	DESCRIPTION
A0 GENERAL	A000	COVER PAGE
A0 GENERAL	A001	SECTION J COMMITMENTS
A0 GENERAL	A002	SURVEY
A0 GENERAL	A003	DEMOLITION PLAN
A0 GENERAL	A004	SITE PLAN
A0 GENERAL	A005	SITE ANALYSIS
A0 GENERAL	A006	STREETSCAPE ANALYSIS
A0 GENERAL	A007	GFA CALCULATION
A0 GENERAL	A008	UNIT SCHEDULE
A0 GENERAL	A009	COMMUNAL LIVING AREA CALCULATION
A0 GENERAL	A010	COMMUNAL OPEN SPACE CALCULATION
A0 GENERAL	A011	LANDSCAPE & DEEP SOIL CALCULATION
A0 GENERAL	A012	SUN EYE DIAGRAM - 21ST JUNE
A0 GENERAL	A013	SHADOW DIAGRAM - 21ST JUNE
A0 GENERAL	A014	EVACUATION DIAGRAM
A0 GENERAL	A015	HEIGHT LIMIT DIAGRAM
A1 PLANS	A101	BASEMENT PLAN
A1 PLANS	A102	GROUND FLOOR PLAN
A1 PLANS	A103	LEVEL 1 PLAN
A1 PLANS	A104	LEVEL 2 PLAN
A1 PLANS	A105	LEVEL 3 PLAN
A1 PLANS	A106	LEVEL 4 PLAN
A1 PLANS	A107	ROOF PLAN
A2 ELEVATION	A201	NORTH & SOUTH ELEVATION
A2 ELEVATION	A202	EAST ELEVATION
A2 ELEVATION	A203	WEST ELEVATION
A2 ELEVATION	A204	FRONT FENCE ELEVATION
A3 SECTION	A301	SECTION A
A3 SECTION	A302	SECTION B
A3 SECTION	A303	SECTION C (RAMP SECTION)
A3 SECTION	A304	SECTION D (SIDE SECTION DETAIL)
A4 SCHEDULE	A401	MATERIAL SCHEDULE
A4 SCHEDULE	A402	DOORS SCHEDULE
A4 SCHEDULE	A403	WINDOWS SCHEDULE
A4 SCHEDULE	A404	TYPICAL KITCHEN DETAILS



74 KEELER ST CARLINGFORD
CO-LIVING HOUSING - S34

ROOM MIX:
43 DOUBLE ROOMS
1 SINGLE ROOM
2 COMMUNAL LIVING AREA

SITE AREA: 950.7m²
PROPOSED FSR: 1.43: 1
PROPOSED GFA: 1,359.31 m²

3 DOCUMENTATION & REQUIREMENTS

The following NCC 2022 Section J summary must be incorporated into the Construction Certificate documentation. Refer to the relevant section of the report for more detail.

- **Summary of J4**
  - Roof System Type: For all concrete roof surfaces add insulation with minimum insulation rating of R3.33. **NOTE: In climate zones 1, 2, 3, 4, 5, 6 and 7, the solar absorptance of the upper surface must not be more than 0.45 – you must ensure that the colour chosen meets this requirement.**
  - For all external walls R2.70 insulation is to be installed.
  - For glazing specifications refer to the Façade report at average U-value and SHGC tables for each orientation. Note that Method 2 was used to calculate. U-value to be installed shall be 4.19 or lower and the SHGC to be 0.35 or lower; (see relevant façade report).
  - For concrete slab on ground, above carpark and exposed subfloors that are located below conditioned spaces add insulation with minimum rating of R1.69.
- **Summary of J5**
  Refer to relevant section for required information
- **Summary of J6**
  Refer to relevant section for required information
- **Summary of J7**
  - Design illumination power load for basement level is 10895 Watts. Maximum system illumination power load allowance is 12182 Watts.
- **Summary of J8**
  Refer to relevant section for required information
- **Summary of J9**
  Refer to relevant section for required information

WHEN CONSTRUCTION IS COMPETED

The section above provides the documentation of Section J requirements which apply to the proposal development. Attention is drawn to the need to provide documentation during construction that each requirement has been assessed and attained.

This should include when applicable:

- Certificates from specific suppliers and contractors such as insulation ratings installed, U-Value and SHGC of glazed components installed, etc
- Site inspections records if required by PCA.
  It is imperative that the information in this report to be forwarded to the person in charge of this project, to ensure that all work is carried out in accordance with each and every item that has been documented in this report.

Australian Energy Efficiency Consulting
W: www.aenec.com.au
P: 02 9994 8906
E: info@aenec.com.au

AENEC

NOTE
The Builder shall check all dimensions and levels on site prior to construction. Notify any errors, discrepancies or omissions to the architect. Refer to written dimensions only. Do not scale drawings. Drawings shall not be used for construction purposes until issued for construction. This drawing reflects a design by Texco Design Pty Ltd and is to be used only for work when authorised in writing by Texco Design Pty Ltd.

All boundaries and contours are subject to survey drawing. All levels to Australian Height Data. It is the contractors responsibility to confirm all measurements on site and locations of any services prior to work on site.

All documents here within are subject to Australian Copyright Laws.

Project Partners
Refer to consultant documentation when directed

- Planning Consultant	- **Think Planners**
- Ecologist	- **SIA Ecological**
- BCA & Access	- **BIA**
- Arborist Consultant	- **NSW Trees**
- QS Consultant	- **Property & Building Assessment**
- Section J Consultant	- **AENEC**
- Civil Engineer	- **JCO Consultants**
- Stormwater Engineer	- **JCO Consultants**
- Landscape Designer	- **Conzept**
- Traffic Engineer	- **Genesis Traffic**
- Land Surveyor	- **RGM**
- Geotechnical Engineer	- **STANTEC**
- Flood Engineer	- **HYDRACOR**

RevID	Transmittal Set Date	Approved by	Rev. Note
A	27/03/2024	T.Z	ISSUE FOR DA
B	16/01/2025	T.Z	ISSUE FOR S34
C	11/02/2025	T.Z	ISSUE FOR S34
D	3/03/2025		ISSUE FOR S34
E	13/03/2025	T.Z	ISSUE FOR S34
F	20/03/2025	T.Z	ISSUE FOR S34

Project Designer
TEXCO DESIGN
Nom Arch: NSW ARB 11348
E: office@texcodesign.com.au P: +61 449 984 889

TRUE NORTH

Drawn | Checked A.W I J.C |
Revision Date: 20/03/2025
Project NO. 2335
Project Status S34

Client MR BILLY CHEN
Site: 74 KEELER ST CARLINGFORD
Climate Zone 5
Wind Region A

PAPER
A3

DRAWING TITLE :
GENERAL
SECTION J COMMITMENTS

PROJECT NAME :
74 KEELER ST CARLINGFORD

REVISION NO.
F

DRAWING NO.
A001

www.dialbeforeyoudig.com.au
DIAL 1100 BEFORE YOU DIG

LOT DIAGRAM

NOT TO SCALE

KEELER ST.

LEGEND

- WATER METER
- BENCH MARK
- COMMS PIT

ST : STEPS
GM : GAS METER
GV : GAS MAIN VALVE
KO : KERB OUTLET
PP : POWER POLE
BKW : BRICK WALL
HV : HIGH VOLTAGE
WS : WINDOW SILL
WT : TOP OF WINDOW
RRL : RIDGELINE RL
PB : PLANTER BOX
SMH : SEWER MANHOLE
RDW : RENDERED WALL
RDP : RENDERED PILLAR
TOW : TOP OF WALL RL
TOF : TOP OF FENCE RL
GUT : TOP OF GUTTER RL

AWN : TOP OF AWNING RL
PPT : TOP OF PARAPET RL
MPF : METAL PANEL FENCE
TBK : TOP CONC. BARRIER KERB
CBO : CONC. BEAM OVER GF & RAMP

POWER LINE —E—E—
HV POWER LINE —E—
SEWER LINE —S—
(APPROX LOCATION)


D:0.3 (DIAMETER)
S:10 (SPREAD)
H:14 (HEIGHT)

SHRUBS

SP 92382

TABLE OF TREE REFERENCE NUMBERS

#	H	S	D	#	H	S	D	#	H	S	D	#	H	S	D
T358	7	6	0.2	T543	5	4	0.2	T794	5	6	0.2	T894	3	2	0.2
T534	4	4	0.1	T544	5	4	0.2	T886	6	6	0.2	T895	8	10	0.5
T535	5	4	0.2	T545	5	4	0.2	T887	5	6	0.2	T896	8	10	0.5
T536	5	4	0.2	T711	8	4	0.2	T888	5	10	0.3	T897	4	4	0.1
T537	5	4	0.2	T712	8	4	0.2	T889	5	4	0.2	T898	4	4	0.1
T538	6	6	0.2	T713	8	4	0.2	T890	8	12	0.8	T941	7	8	0.3
T539	8	4	0.3	T714	8	4	0.2	T891	5	4	0.2	T942	8	10	0.4
T540	10	8	0.5	T715	12	12	0.6	T892	6	8	0.4	T943	8	10	0.4
T541	10	8	0.5	T793	5	6	0.2	T893	4	4	0.2	T944	6	4	0.3
T542	5	4	0.2												

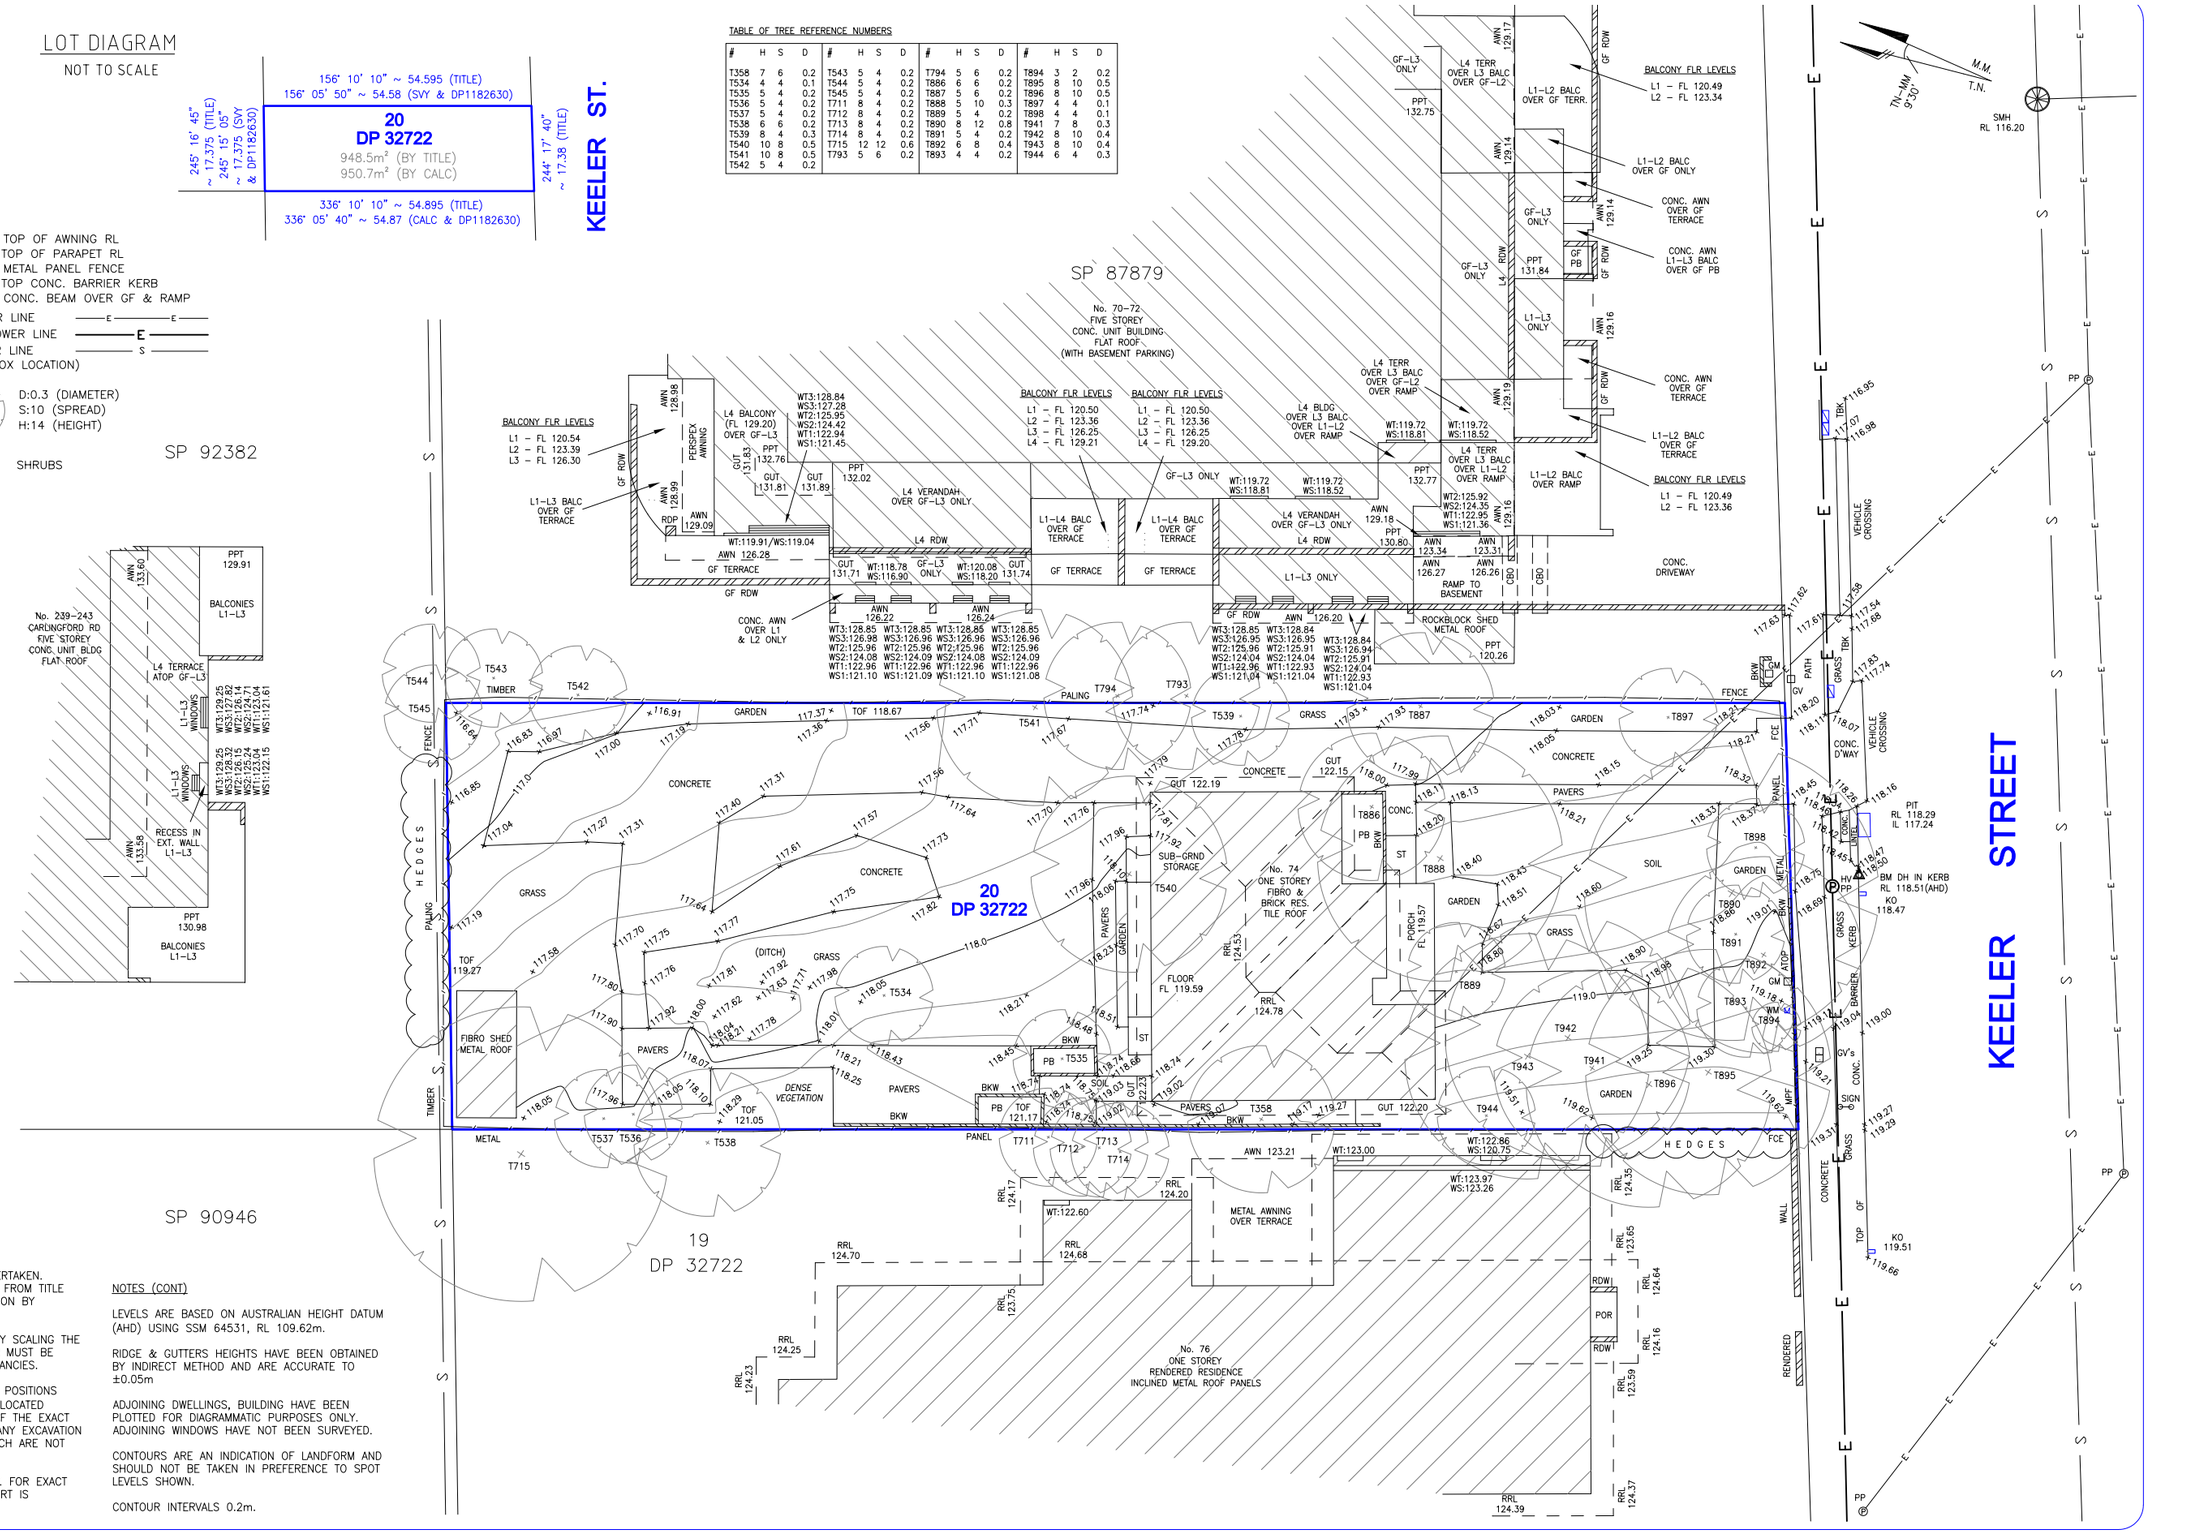

NOTES

NO BOUNDARY SURVEY HAS BEEN UNDERTAKEN. BEARINGS, DIMENSIONS AND AREAS ARE FROM TITLE ONLY AND ARE SUBJECT TO CONFIRMATION BY BOUNDARY SURVEY.

DIMENSIONS SHALL NOT BE OBTAINED BY SCALING THE DETAIL FROM THE DRAWING. SURVEYOR MUST BE CONTACTED IF THERE ARE ANY DISCREPANCIES.

SERVICES SHOWN ARE INDICATIVE ONLY. POSITIONS ARE BASED ON SURFACE INDICATOR(S) LOCATED DURING FIELD SURVEY. CONFIRMATION OF THE EXACT POSITION SHOULD BE MADE PRIOR TO ANY EXCAVATION WORK. OTHER SERVICES MAY EXIST WHICH ARE NOT SHOWN.

SEWER LINE SHOWN IS INDICATIVE ONLY. FOR EXACT LOCATION, A SERVICE PROTECTION REPORT IS REQUIRED.

NOTES (CONT)

LEVELS ARE BASED ON AUSTRALIAN HEIGHT DATUM (AHD) USING SSM 64531, RL 109.62m.

RIDGE & GUTTERS HEIGHTS HAVE BEEN OBTAINED BY INDIRECT METHOD AND ARE ACCURATE TO ±0.05m

ADJOINING DWELLINGS, BUILDING HAVE BEEN PLOTTED FOR DIAGRAMMATIC PURPOSES ONLY. ADJOINING WINDOWS HAVE NOT BEEN SURVEYED.

CONTOURS ARE AN INDICATION OF LANDFORM AND SHOULD NOT BE TAKEN IN PREFERENCE TO SPOT LEVELS SHOWN.

CONTOUR INTERVALS 0.2m.

A	28.12.23		INITIAL ISSUE

× COPYRIGHT ×
THE CONCEPTS AND INFORMATION CONTAINED IN THIS DOCUMENT ARE THE COPYRIGHT OF RGM PROPERTY SURVEYS USE OR DUPLICATION OF THIS DOCUMENT IN PART OR IN FULL WITHOUT THE WRITTEN PERMISSION OF RGM PROPERTY SURVEYS CONSTITUTES AN INFRINGEMENT OF COPYRIGHT.

× DRAWING STATUS ×
UNLESS THERE IS AN APPROVED SIGNATURE IN THE BOX PROVIDED THIS PLAN IS NOT VERIFIED AND IS NOT FOR CONSTRUCTION.

× CAUTION ×
THE INFORMATION SHOWN ON THIS PLAN MAY BE INSUFFICIENT FOR SOME TYPES OF DETAILED DESIGN. RGM PROPERTY SURVEYS SHOULD BE CONSULTED AS TO THE SUITABILITY OF THE INFORMATION SHOWN HEREIN PRIOR TO

RGM property surveys
ABN 37 145 495 825

SCALE	1 : 125 @ A1	COORDINATE SYSTEM	ASSUMED
LOCAL GOV'T AREA	CITY OF PARRAMATTA	SURVEY K.G.	DRAWN K.B.
		DATE OF SURVEY 21.12.23	CHECKED R.M.
HUY THAI – REGISTERED SURVEYOR 8258		HEIGHT ORIGIN AHD	APPROVED H.T.

CLIENT
FIRST CIVIL

PROJECT TITLE
74 KEELER STREET, CARLINGFORD

DRAWING TITLE
PLAN SHOWING LEVELS & DETAIL OVER LOT 20 IN DP 32722


CAD REF
C:\231616.dwg

DRAWING NO
231616/001

SHEET 1 OF 1

JOB NAME
74 KEELER

REV
A

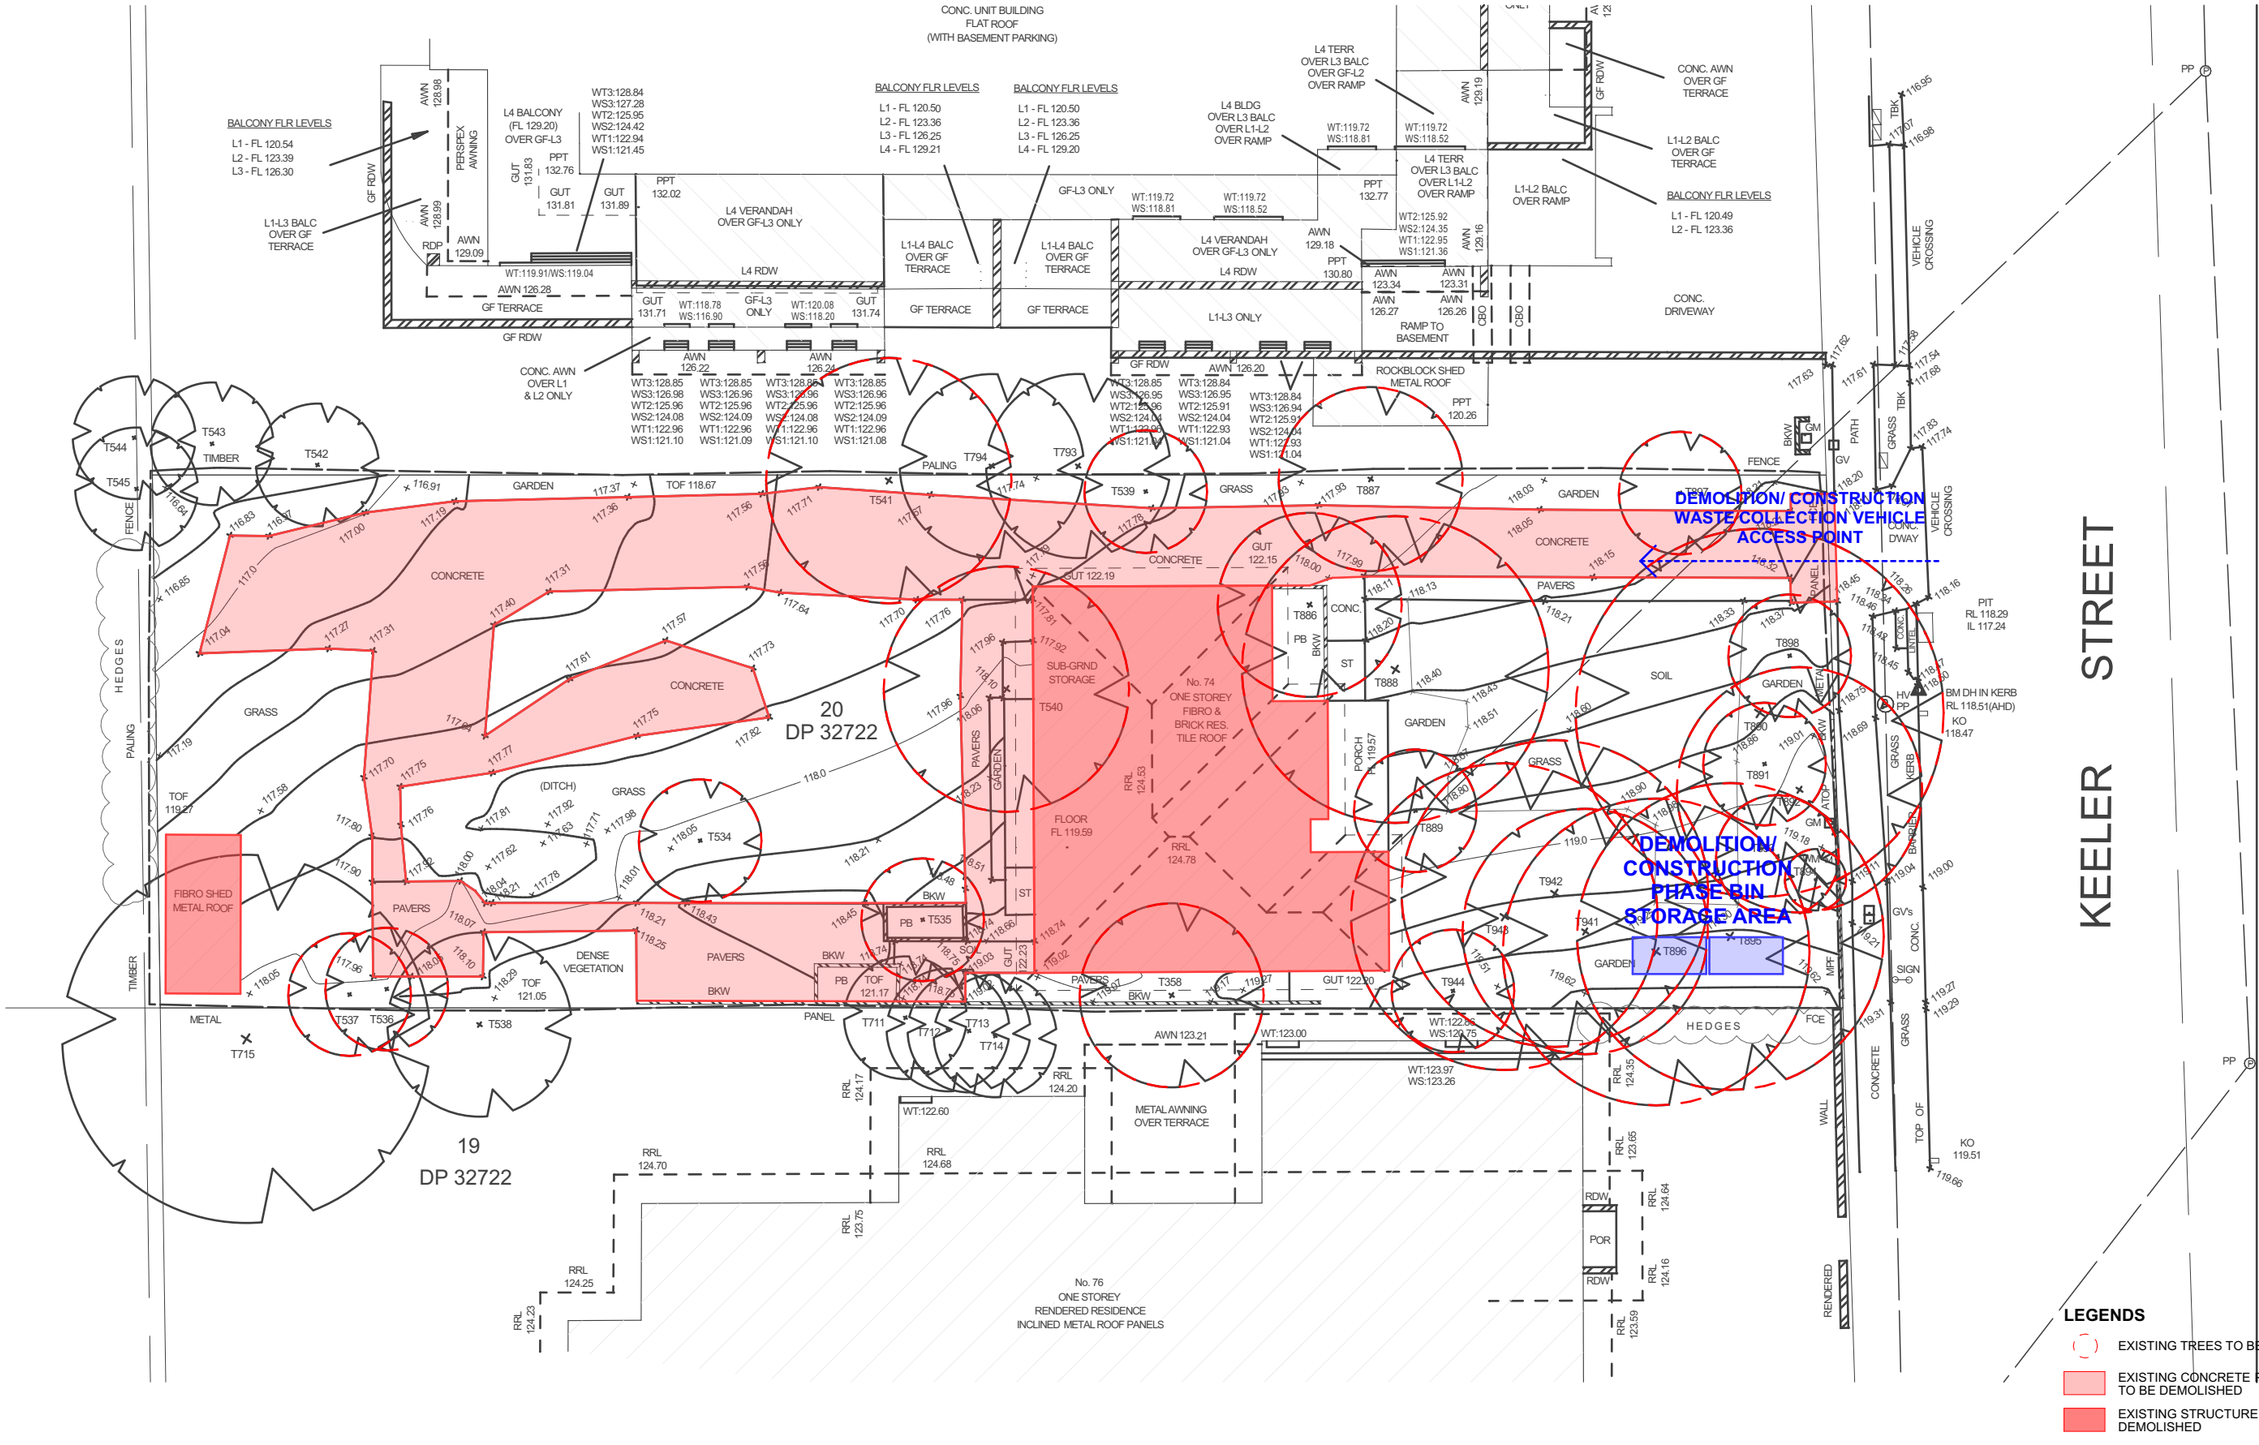

NOTE

The Builder shall check all dimensions and levels on site prior to construction. Notify any errors, discrepancies or omissions to the architect. Refer to written dimensions only. Do not scale drawings. Drawings shall not be used for construction purposes until issued for construction. This drawing reflects a design by Texco Design Pty Ltd and is to be used only for work when authorised in writing by Texco Design Pty Ltd.

All boundaries and contours are subject to survey drawing. All levels to Australian Height Data. It is the contractors responsibility to confirm all measurements on site and locations of any services prior to work on site.

All documents here within are subject to Australian Copyright Laws.

Project Partners

Refer to consultant documentation when directed

- Planning Consultant	- Think Planners
- Ecologist	- SIA Ecological
- BCA & Access	- SIA
- Arborist Consultant	- NSW Trees
- QS Consultant	- Property & Building Assessment
- Section J Consultant	- AENEC
- Civil Engineer	- JCO Consultants
- Stormwater Engineer	- JCO Consultants
- Landscape Designer	- Concept
- Traffic Engineer	- Genesis Traffic
- Land Surveyor	- RDM
- Geotechnical Engineer	- STANTEC
- Flood Engineer	- HYDRACOR

RevID	Transmittal Set Date	Approved by	Rev. Note
A	27/03/2024	T.Z	ISSUE FOR DA
B	16/01/2025	T.Z	ISSUE FOR S34
C	11/02/2025	T.Z	ISSUE FOR S34
D	3/03/2025		ISSUE FOR S34
E	13/03/2025	T.Z	ISSUE FOR S34
F	20/03/2025	T.Z	ISSUE FOR S34

Project Designer

TEXCO DESIGN

E: office@texcodesign.com.au

Nom Arch: NSW ARB 11348

P: +61 449 984 889

TRUE NORTH

Drawn | Checked	A.W I J.C |
Revision Date:	20/03/2025
Project NO.	2335
Project Status	S34
Client	MR BILLY CHEN
Site:	74 KEELER ST CARLINGFORD
Climate Zone	5
Wind Region	A

PAPER

A3

1:200

DRAWING TITLE :

GENERAL

DEMOLITION PLAN

PROJECT NAME :


74 KEELER ST CARLINGFORD

REVISION NO.


F

DRAWING NO.


A003

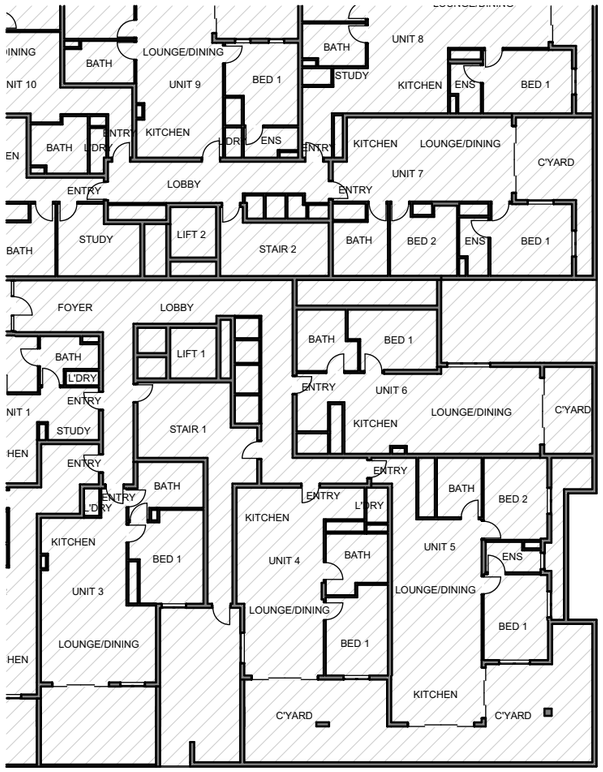


NO.243
CARLINGFORD RD

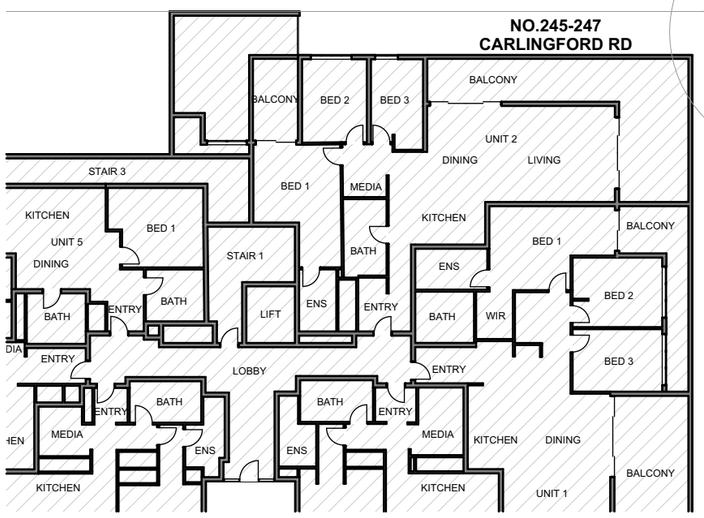

NO.245-247
CARLINGFORD RD

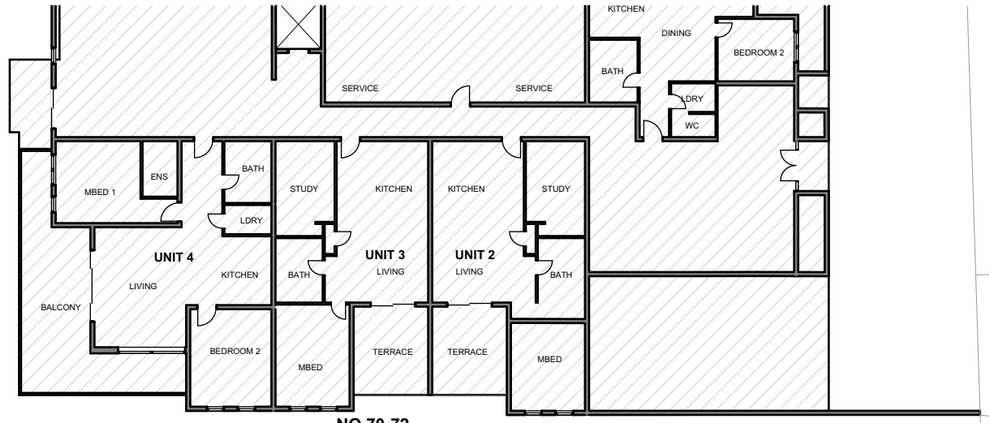

NO.70-72
KEELER ST

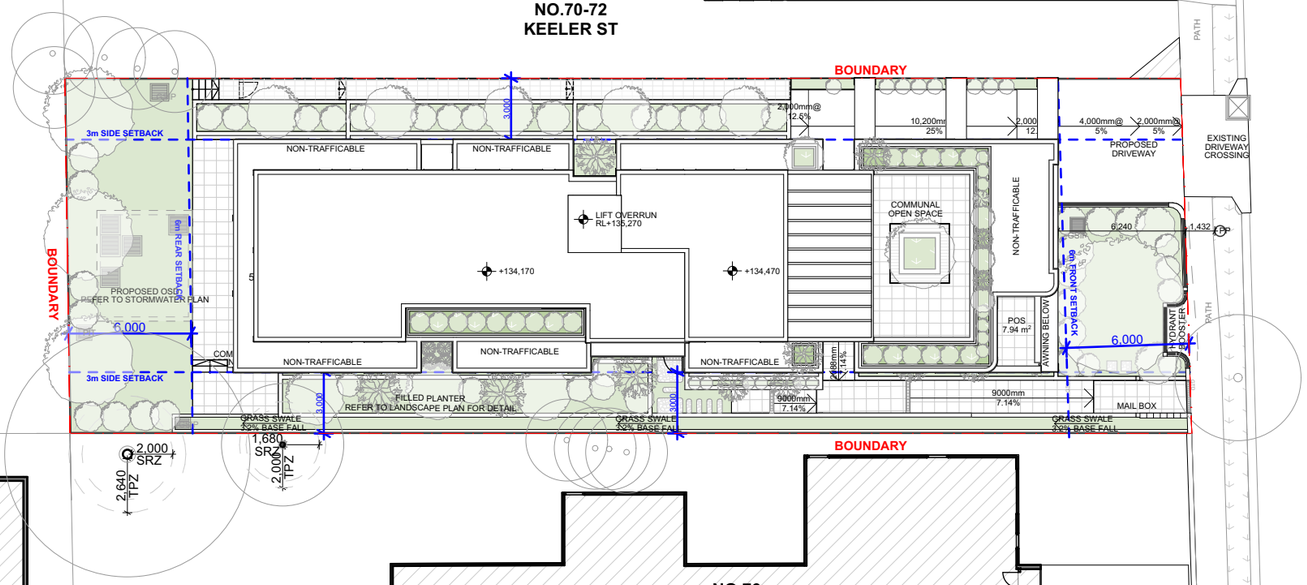

KEELER STREET

NO.76
KEELER ST
RESIDENCE

NO.78
KEELER ST
RESIDENCE

NOTE
The Builder shall check all dimensions and levels on site prior to construction. Notify any errors, discrepancies or omissions to the architect. Refer to written dimensions only. Do not scale drawings. Drawings shall not be used for construction purposes until issued for construction. This drawing reflects a design by Texco Design Pty Ltd and is to be used only for work when authorised in writing by Texco Design Pty Ltd.

All boundaries and contours are subject to survey drawing. All levels to Australian Height Data. It is the contractors responsibility to confirm all measurements on site and locations of any services prior to work on site.

All documents here within are subject to Australian Copyright Laws.

Project Partners
Refer to consultant documentation when directed

- Planning Consultant	- **Think Planners**
- Ecologist	- **SIA Ecological**
- BCA & Access	- **BIA**
- Arborist Consultant	- **NSW Trees**
- QS Consultant	- **Property & Building Assessment**
- Section J Consultant	- **AENEC**
- Civil Engineer	- **JCO Consultants**
- Stormwater Engineer	- **JCO Consultants**
- Landscape Designer	- **Concept**
- Traffic Engineer	- **Genesis Traffic**
- Land Surveyor	- **RGM**
- Geotechnical Engineer	- **STANTEC**
- Flood Engineer	- **HYDRACOR**

RevID	Transmittal Set Date	Approved by	Rev. Note
A	27/03/2024	T.Z	ISSUE FOR DA
B	16/01/2025	T.Z	ISSUE FOR S34
C	11/02/2025	T.Z	ISSUE FOR S34
D	3/03/2025		ISSUE FOR S34
E	13/03/2025	T.Z	ISSUE FOR S34
F	20/03/2025	T.Z	ISSUE FOR S34

Project Designer
TEXCO DESIGN
Nom Arch: NSW ARB 11348
E: office@texcodesign.com.au
P: +61 449 984 889

TRUE NORTH

Drawn | Checked	A.W I J.C |
Revision Date:	20/03/2025
Project NO.	2335
Project Status	S34
Client	MR BILLY CHEN
Site:	74 KEELER ST CARLINGFORD
Climate Zone	5
Wind Region	A

PAPER A3 1:300

DRAWING TITLE :
GENERAL
SITE PLAN

PROJECT NAME :
74 KEELER ST CARLINGFORD

REVISION NO. **F**

DRAWING NO. **A004**



NOTE

The Builder shall check all dimensions and levels on site prior to construction. Notify any errors, discrepancies or omissions to the architect. Refer to written dimensions only. Do not scale drawings. Drawings shall not be used for construction purposes until issued for construction. This drawing reflects a design by Texco Design Pty Ltd and is to be used only for work when authorised in writing by Texco Design Pty Ltd.

All boundaries and contours are subject to survey drawing. All levels to Australian Height Data. It is the contractors responsibility to confirm all measurements on site and locations of any services prior to work on site.

All documents here within are subject to Australian Copyright Laws.

Project Partners

Refer to consultant documentation when directed

- Planning Consultant	- **Think Planners**
- Ecologist	- **SIA Ecological**
- BCA & Access	- **BIA**
- Arborist Consultant	- **NSW Trees**
- QS Consultant	- **Property & Building Assessment**
- Section J Consultant	- **AENEC**
- Civil Engineer	- **JCO Consultants**
- Stormwater Engineer	- **JCO Consultants**
- Landscape Designer	- **Concept**
- Traffic Engineer	- **Genesis Traffic**
- Land Surveyor	- **RGM**
- Geotechnical Engineer	- **STANTEC**
- Flood Engineer	- **HYDRACOR**

RevID	Transmittal Set Date	Approved by	Rev. Note
A	27/03/2024	T.Z	ISSUE FOR DA
B	16/01/2025	T.Z	ISSUE FOR S34
C	11/02/2025	T.Z	ISSUE FOR S34
D	3/03/2025		ISSUE FOR S34
E	13/03/2025	T.Z	ISSUE FOR S34
F	20/03/2025	T.Z	ISSUE FOR S34

Project Designer

TEXCO DESIGN

Nom Arch: NSW ARB 11348

E: office@texcodesign.com.au P: +61 449 984 889

N

TRUE NORTH

Drawn | Checked	A.W I J.C |
Revision Date:	20/03/2025
Project NO.	2335
Project Status	S34
Client	MR BILLY CHEN
Site:	74 KEELER ST CARLINGFORD
Climate Zone	5
Wind Region	A

PAPER A3

DRAWING TITLE :

GENERAL

SITE ANALYSIS

PROJECT NAME :

74 KEELER ST CARLINGFORD

REVISION NO. **F**

DRAWING NO. **A005**



NOTE

The Builder shall check all dimensions and levels on site prior to construction. Notify any errors, discrepancies or omissions to the architect. Refer to written dimensions only. Do not scale drawings. Drawings shall not be used for construction purposes until issued for construction. This drawing reflects a design by Texco Design Pty Ltd and is to be used only for work when authorised in writing by Texco Design Pty Ltd.

All boundaries and contours are subject to survey drawing. All levels to Australian Height Data. It is the contractors responsibility to confirm all measurements on site and locations of any services prior to work on site.

All documents here within are subject to Australian Copyright Laws.

Project Partners

Refer to consultant documentation when directed

- Planning Consultant	- **Think Planners**
- Ecologist	- **SIA Ecological**
- BCA & Access	- **BIA**
- Arborist Consultant	- **NSW Trees**
- QS Consultant	- **Property & Building Assessment**
- Section J Consultant	- **AENEC**
- Civil Engineer	- **JCO Consultants**
- Stormwater Engineer	- **JCO Consultants**
- Landscape Designer	- **Concept**
- Traffic Engineer	- **Genesis Traffic**
- Land Surveyor	- **RGM**
- Geotechnical Engineer	- **STANTEC**
- Flood Engineer	- **HYDRACOR**

RevID	Transmittal Set Date	Approved by	Rev. Note
A	27/03/2024	T.Z	ISSUE FOR DA
B	16/01/2025	T.Z	ISSUE FOR S34
C	11/02/2025	T.Z	ISSUE FOR S34
D	3/03/2025		ISSUE FOR S34
E	13/03/2025	T.Z	ISSUE FOR S34
F	20/03/2025	T.Z	ISSUE FOR S34

Project Designer

TEXCO DESIGN

Nom Arch: NSW ARB 11348

E: office@texcodesign.com.au P: +61 449 984 889

N

TRUE NORTH

Drawn | Checked	A.W I J.C |
Revision Date:	20/03/2025
Project NO.	2335
Project Status	S34
Client	MR BILLY CHEN
Site:	74 KEELER ST CARLINGFORD
Climate Zone	5
Wind Region	A

PAPER

A3

1:200

DRAWING TITLE :

GENERAL

STREETSCAPE ANALYSIS

PROJECT NAME :


74 KEELER ST CARLINGFORD


REVISION NO.

F


DRAWING NO.

A006

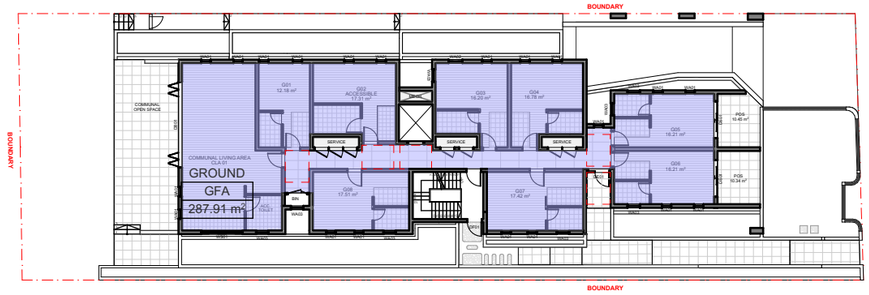

BOUNDARY
BOUNDARY
BOUNDARY
COMMUNAL OPEN SPACE
COMMUNAL LIVING AREA
GROUND
GFA
287.91 m²
G01 12.18 m²
G02 ACCESSIBLE 17.3 m²
G03 14.20 m²
G04 16.78 m²
G05 16.21 m²
G06 16.21 m²
G07 17.33 m²
G08 17.42 m²
SERVICE
SERVICE
SERVICE

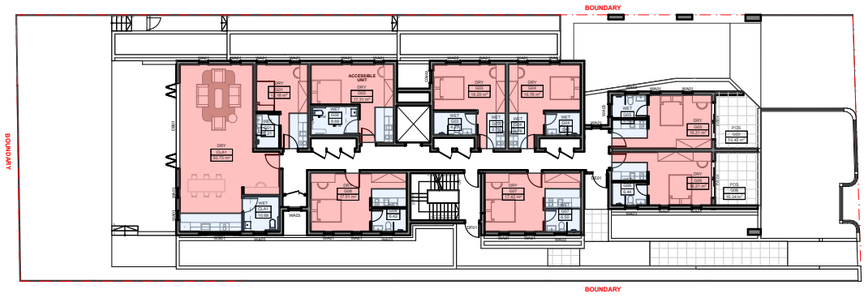


GROUND FLOOR
1:400

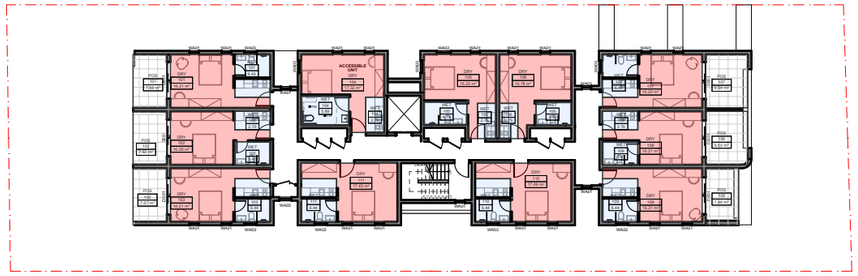


LEVEL 1
1:400

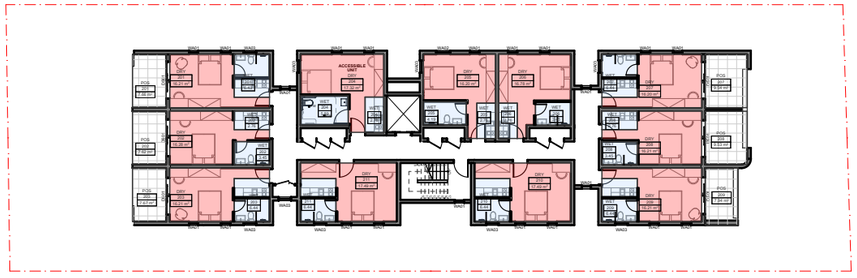

LEVEL 2
1:400

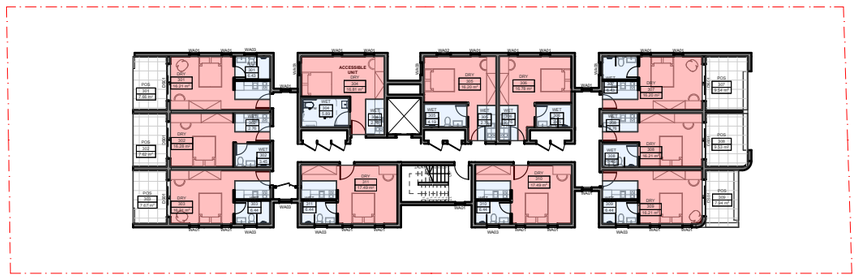

LEVEL 3
1:400

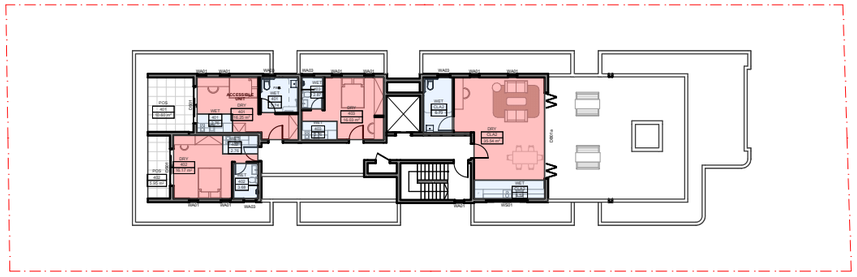

LEVEL 4
1:400

STOREY	GROUND FLOOR																	
UNIT No.	CLA1	CLA1	G01	G01	G02	G02	G03	G03	G04	G04	G05	G05	G06	G06	G07	G07	G08	G08
DRY/WET AREA	DRY	WET	DRY	WET	DRY	WET	DRY	WET	DRY	WET	DRY	WET	DRY	WET	DRY	WET	DRY	WET
REQUIRED AREA	MIN DRY ARAE: SINGLE ROOM 12SQM, DOUBLE ROOM 16SQM																	
PROVIDED AREA	50.75	10.68	12.18	6.21	17.31	8.66	16.20	7.01	16.78	6.21	16.21	6.44	16.21	6.44	17.42	6.50	17.51	6.42
GROSS AREA	**61.43**		**18.39**		**25.97**		**23.21**		**22.99**		**22.65**		**22.65**		**23.92**		**23.93**	
POS AREA	—		—		—		—		—		10.34		7.66		—		—	
					ACCESSIBLE UNIT													

STOREY	LEVEL 1																					
UNIT No.	101	101	102	102	103	103	104	104	105	105	106	106	107	107	108	108	109	109	110	110	111	111
DRY/WET AREA	DRY	WET	DRY	WET	DRY	WET	DRY	WET	DRY	WET	DRY	WET	DRY	WET	DRY	WET	DRY	WET	DRY	WET	DRY	WET
REQUIRED AREA	MIN DRY ARAE: SINGLE ROOM 12SQM, DOUBLE ROOM 16SQM																					
PROVIDED AREA	16.21	6.43	16.28	6.21	16.21	6.44	17.32	8.65	16.20	6.95	16.78	6.21	16.20	6.44	16.21	6.21	16.21	6.44	17.49	6.44	17.49	6.44
GROSS AREA	**22.64**		**22.49**		**22.65**		**25.97**		**23.15**		**22.99**		**22.64**		**22.42**		**22.65**		**23.93**		**23.93**	
POS AREA	7.62		7.67		9.54		—		—		—		9.53		7.94		7.66		—		—	
							ACCESSIBLE UNIT															

STOREY	LEVEL 2																					
UNIT No.	201	201	202	202	203	203	204	204	205	205	206	206	207	207	208	208	209	209	210	210	211	211
DRY/WET AREA	DRY	WET	DRY	WET	DRY	WET	DRY	WET	DRY	WET	DRY	WET	DRY	WET	DRY	WET	DRY	WET	DRY	WET	DRY	WET
REQUIRED AREA	MIN DRY ARAE: SINGLE ROOM 12SQM, DOUBLE ROOM 16SQM																					
PROVIDED AREA	16.21	6.43	16.28	6.21	16.21	6.44	17.32	8.65	16.20	6.95	16.78	6.21	16.20	6.44	16.21	6.21	16.21	6.44	17.49	6.44	17.49	6.44
GROSS AREA	**22.64**		**22.49**		**22.65**		**25.97**		**23.15**		**22.99**		**22.64**		**22.42**		**22.65**		**23.93**		**23.93**	
POS AREA	7.62		7.67		9.54		—		—		—		9.53		7.94		7.66		—		—	
							ACCESSIBLE UNIT															

STOREY	LEVEL 3																					
UNIT No.	301	301	302	302	303	303	304	304	305	305	306	306	307	307	308	308	309	309	310	310	311	311
DRY/WET AREA	DRY	WET	DRY	WET	DRY	WET	DRY	WET	DRY	WET	DRY	WET	DRY	WET	DRY	WET	DRY	WET	DRY	WET	DRY	WET
REQUIRED AREA	MIN DRY ARAE: SINGLE ROOM 12SQM, DOUBLE ROOM 16SQM																					
PROVIDED AREA	16.21	6.43	16.28	6.21	16.21	6.44	16.81	8.65	16.20	6.95	16.78	6.21	16.20	6.43	16.21	6.21	16.21	6.44	17.49	6.44	17.49	6.44
GROSS AREA	**22.64**		**22.49**		**22.65**		**25.46**		**23.15**		**22.99**		**22.63**		**22.42**		**22.65**		**23.93**		**23.93**	
POS AREA	7.62		7.67		9.54		—		—		—		9.53		7.94		10.60		—		—	
							ACCESSIBLE UNIT															

STOREY	LEVEL 4							
UNIT No.	401	401	402	402	403	403	CLA2	CLA2
DRY/WET AREA	DRY	WET	DRY	WET	DRY	WET	DRY	WET
REQUIRED AREA	MIN DRY ARAE: SINGLE ROOM 12SQM, DOUBLE ROOM 16SQM							
PROVIDED AREA	16.25	8.50	16.17	6.44	16.03	5.63	35.54	12.31
GROSS AREA	**24.75**		**22.61**		**21.66**		**47.85**	
POS AREA	10.60		5.95		—		—	
	ACCESSIBLE UNIT							

LEGENDS

LIVING AREA

WET AREA

POS AREA

NOTE

The Builder shall check all dimensions and levels on site prior to construction. Notify any errors, discrepancies or omissions to the architect. Refer to written dimensions only. Do not scale drawings. Drawings shall not be used for construction purposes until issued for construction. This drawing reflects a design by Texco Design Pty Ltd and is to be used only for work when authorised in writing by Texco Design Pty Ltd.

All boundaries and contours are subject to survey drawing. All levels to Australian Height Data. It is the contractors responsibility to confirm all measurements on site and locations of any services prior to work on site.

All documents here within are subject to Australian Copyright Laws.

Project Partners

Refer to consultant documentation when directed

- Planning Consultant	- **Think Planners**
- Ecologist	- **SIA Ecological**
- BCA & Access	- **BIA**
- Arborist Consultant	- **NSW Trees**
- QS Consultant	- **Property & Building Assessment**
- Section J Consultant	- **AENEC**
- Civil Engineer	- **JCO Consultants**
- Stormwater Engineer	- **JCO Consultants**
- Landscape Designer	- **Concept**
- Traffic Engineer	- **Genesis Traffic**
- Land Surveyor	- **RGM**
- Geotechnical Engineer	- **STANTEC**
- Flood Engineer	- **HYDRACOR**

RevID	Transmittal Set Date	Approved by	Rev. Note
A	27/03/2024	T.Z	ISSUE FOR DA
B	16/01/2025	T.Z	ISSUE FOR S34
C	11/02/2025	T.Z	ISSUE FOR S34
D	3/03/2025		ISSUE FOR S34
E	13/03/2025	T.Z	ISSUE FOR S34
F	20/03/2025	T.Z	ISSUE FOR S34

Project Designer

TEXCO DESIGN
Nom Arch: NSW ARB 11348
E: office@texcodesign.com.au
P: +61 449 984 889

TRUE NORTH

Drawn | Checked	A.W I J.C |
Revision Date:	20/03/2025
Project NO.	2335
Project Status	S34
Client	MR BILLY CHEN
Site:	74 KEELER ST CARLINGFORD
Climate Zone	5
Wind Region	A


PAPER
A3
1:400

DRAWING TITLE :
GENERAL
UNIT SCHEDULE


PROJECT NAME :
74 KEELER ST CARLINGFORD

REVISION NO.
F

DRAWING NO.
A008

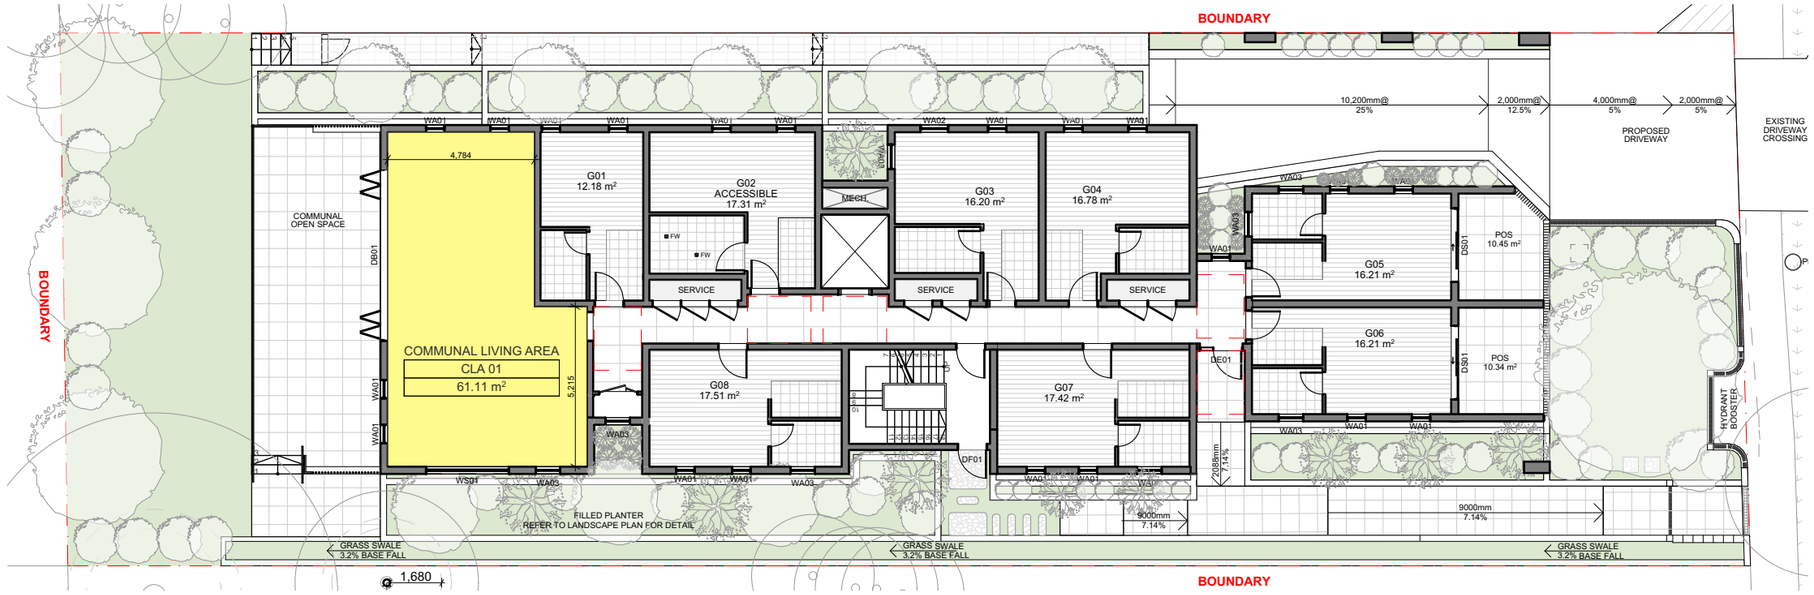

COMMUNAL LIVING AREA - GROUND FLOOR
1:200

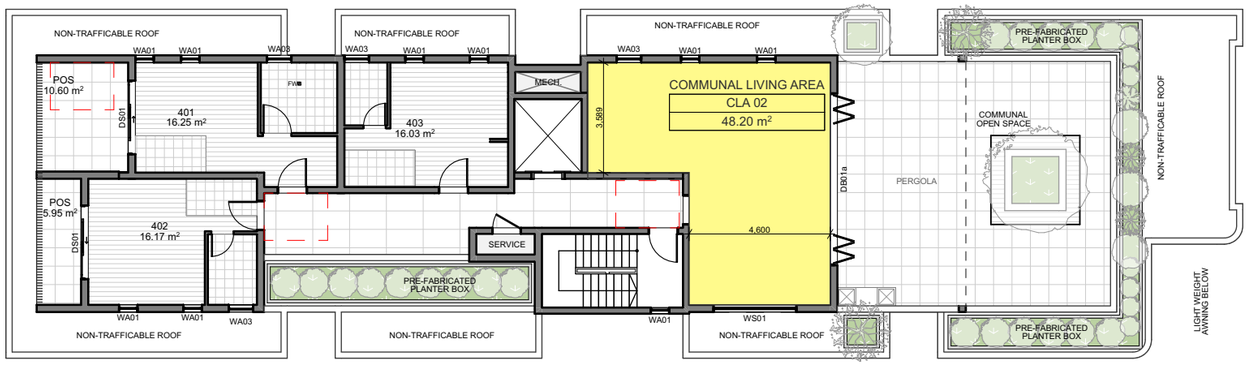

COMMUNAL LIVING AREA - LEVEL 4
1:200

SITE AREA: 950.7 SQM

REQUIRED COMMUNAL LIVING AREA (C.L.A.)
AT LEAST 30m² FOR 6 PRIVATE ROOMS,
PLUS AT LEAST 2m² FOR EACH PRIVATE ROOMS IN
EXCESS OF 6 PRIVATE ROOMS
(MINIMUM DIMENSIONS OF 3M)

REQUIRED C.L.A.:106 m²

PROPOSED DOUBLE ROOMS: 43
PROPOSED SINGLE ROOMS: 1
PROPOSED C.L.A.: 2
PROPOSED C.L.A.: 109.31 SQM

COMMUNAL LIVING AREA

NOTE
The Builder shall check all dimensions and levels on site prior to construction. Notify any errors, discrepancies or omissions to the architect. Refer to written dimensions only. Do not scale drawings. Drawings shall not be used for construction purposes until issued for construction. This drawing reflects a design by Texco Design Pty Ltd and is to be used only for work when authorised in writing by Texco Design Pty Ltd.

All boundaries and contours are subject to survey drawing. All levels to Australian Height Data. It is the contractors responsibility to confirm all measurements on site and locations of any services prior to work on site.

All documents here within are subject to Australian Copyright Laws.

Project Partners
Refer to consultant documentation when directed

- Planning Consultant	- **Think Planners**
- Ecologist	- **SIA Ecological**
- BCA & Access	- **BIA**
- Arborist Consultant	- **NSW Trees**
- QS Consultant	- **Property & Building Assessment**
- Section J Consultant	- **AENEC**
- Civil Engineer	- **JCO Consultants**
- Stormwater Engineer	- **JCO Consultants**
- Landscape Designer	- **Concept**
- Traffic Engineer	- **Genesis Traffic**
- Land Surveyor	- **RGM**
- Geotechnical Engineer	- **STANTEC**
- Flood Engineer	- **HYDRACOR**

RevID	Transmittal Set Date	Approved by	Rev. Note
A	27/03/2024	T.Z	ISSUE FOR DA
B	16/01/2025	T.Z	ISSUE FOR S34
C	11/02/2025	T.Z	ISSUE FOR S34
D	3/03/2025		ISSUE FOR S34
E	13/03/2025	T.Z	ISSUE FOR S34
F	20/03/2025	T.Z	ISSUE FOR S34

Project Designer
TEXCO DESIGN
Nom Arch: NSW ARB 11348
E: office@texcodesign.com.au
P: +61 449 984 889

TRUE NORTH

Drawn | Checked A.W I J.C |
Revision Date: 20/03/2025
Project NO. 2335
Project Status S34

Client MR BILLY CHEN
Site: 74 KEELER ST CARLINGFORD
Climate Zone 5
Wind Region A


PAPER
A3
1:200

DRAWING TITLE :
GENERAL
COMMUNAL LIVING AREA CALCULATION


PROJECT NAME :
74 KEELER ST CARLINGFORD

REVISION NO.
F

DRAWING NO.
A009

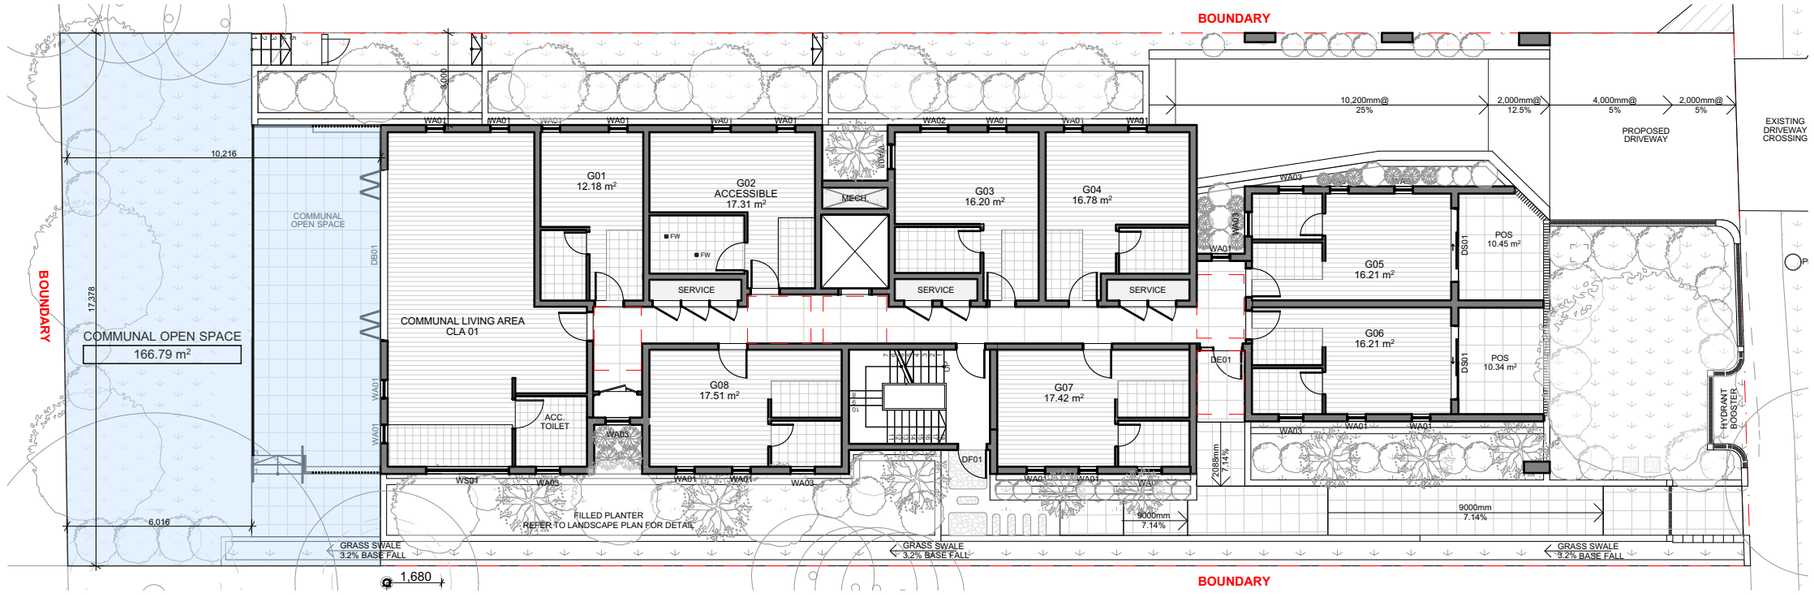

COMMUNAL OPEN SPACE - GROUND FLOOR
1:200

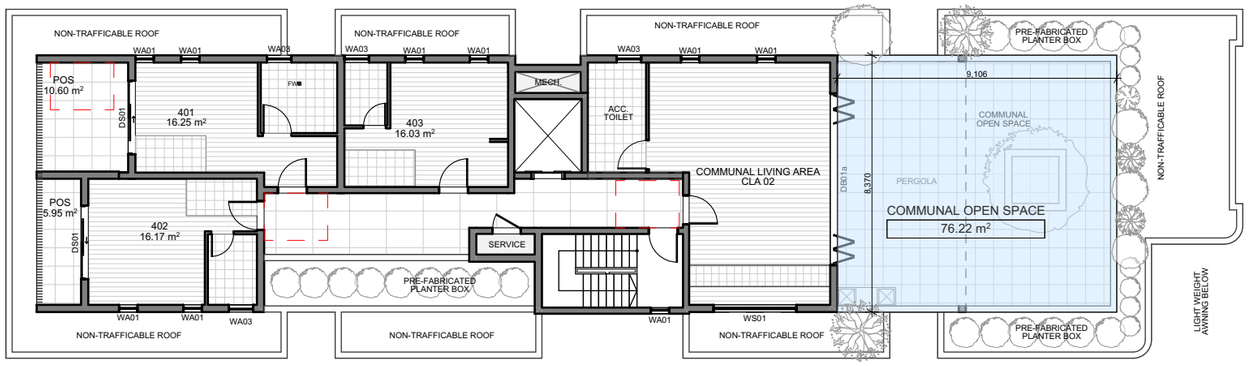

COMMUNAL OPEN SPACE - LEVEL 4
1:200

SITE AREA: 950.7m²

REQUIRED AT LEAST 20% OF THE SITE AREA = 190.14m² (MINIMUM 3M WIDTH)

PROPOSED C.O.S.: 243.01 m²
(25.6% OF SITE AREA)

COMMUNAL OPEN SPACE

NOTE
The Builder shall check all dimensions and levels on site prior to construction. Notify any errors, discrepancies or omissions to the architect. Refer to written dimensions only. Do not scale drawings. Drawings shall not be used for construction purposes until issued for construction. This drawing reflects a design by Texco Design Pty Ltd and is to be used only for work when authorised in writing by Texco Design Pty Ltd.

All boundaries and contours are subject to survey drawing. All levels to Australian Height Data. It is the contractors responsibility to confirm all measurements on site and locations of any services prior to work on site.

All documents here within are subject to Australian Copyright Laws.

Project Partners
Refer to consultant documentation when directed

- Planning Consultant	- **Think Planners**
- Ecologist	- **SIA Ecological**
- BCA & Access	- **BIA**
- Arborist Consultant	- **NSW Trees**
- QS Consultant	- **Property & Building Assessment**
- Section J Consultant	- **AENEC**
- Civil Engineer	- **JCO Consultants**
- Stormwater Engineer	- **JCO Consultants**
- Landscape Designer	- **Concept**
- Traffic Engineer	- **Genesis Traffic**
- Land Surveyor	- **RGM**
- Geotechnical Engineer	- **STANTEC**
- Flood Engineer	- **HYDRACOR**

RevID	Transmittal Set Date	Approved by	Rev. Note
A	27/03/2024	T.Z	ISSUE FOR DA
B	16/01/2025	T.Z	ISSUE FOR S34
C	11/02/2025	T.Z	ISSUE FOR S34
D	3/03/2025		ISSUE FOR S34
E	13/03/2025	T.Z	ISSUE FOR S34
F	20/03/2025	T.Z	ISSUE FOR S34

Project Designer
TEXCO DESIGN
Nom Arch: NSW ARB 11348
E: office@texcodesign.com.au
P: +61 449 984 889

TRUE NORTH

Drawn | Checked	A.W | J.C |
Revision Date:	20/03/2025
Project NO.	2335
Project Status	S34
Client	MR BILLY CHEN
Site:	74 KEELER ST CARLINGFORD
Climate Zone	5
Wind Region	A


PAPER
A3
1:200

DRAWING TITLE :
GENERAL
COMMUNAL OPEN SPACE CALCULATION

PROJECT NAME :
74 KEELER ST CARLINGFORD

REVISION NO.
F

DRAWING NO.
A010

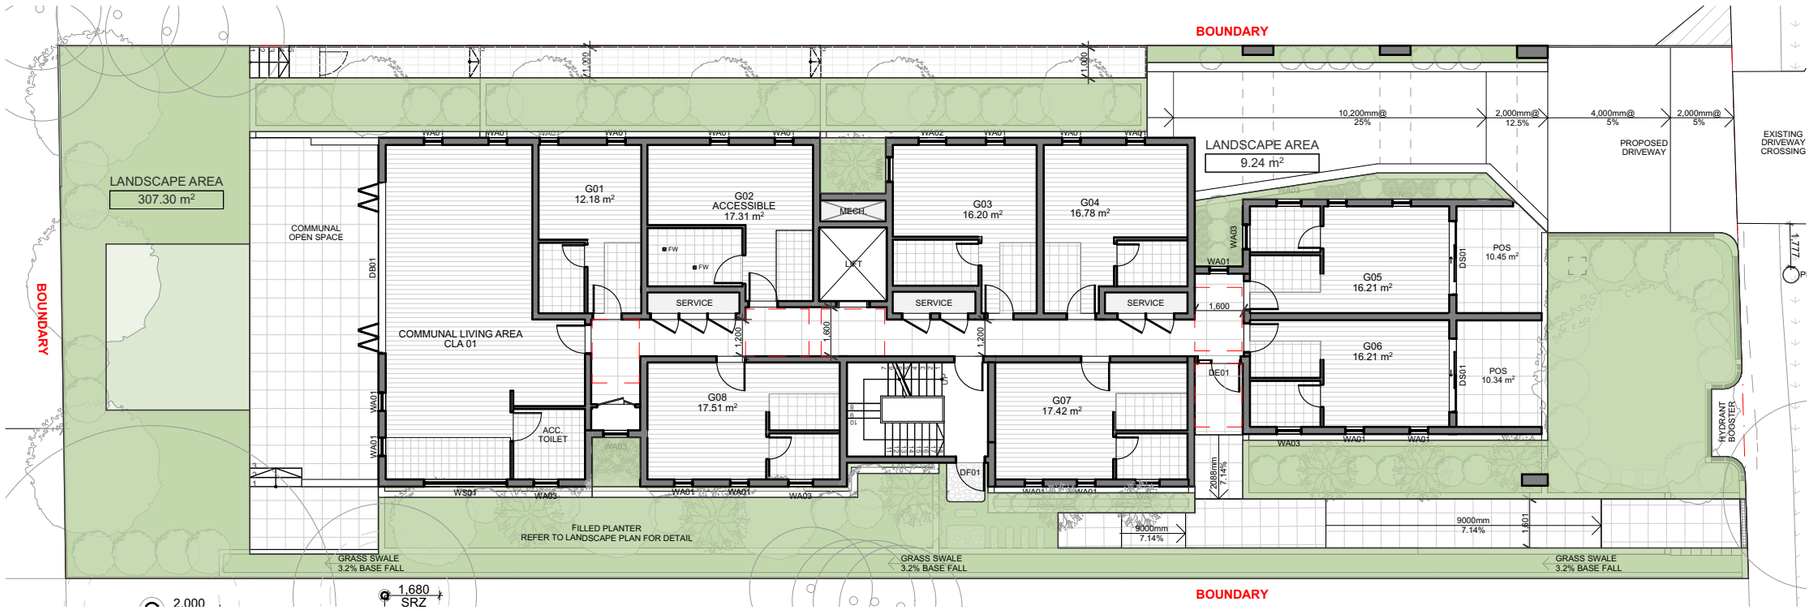


LANDSCAPE AREA - GROUND FLOOR
1:200

SITE AREA: 950.7m²

PROPOSED LANDSCAPE AREA: 316.54 m²
(33.3% OF SITE AREA)

LANDSCAPE AREA

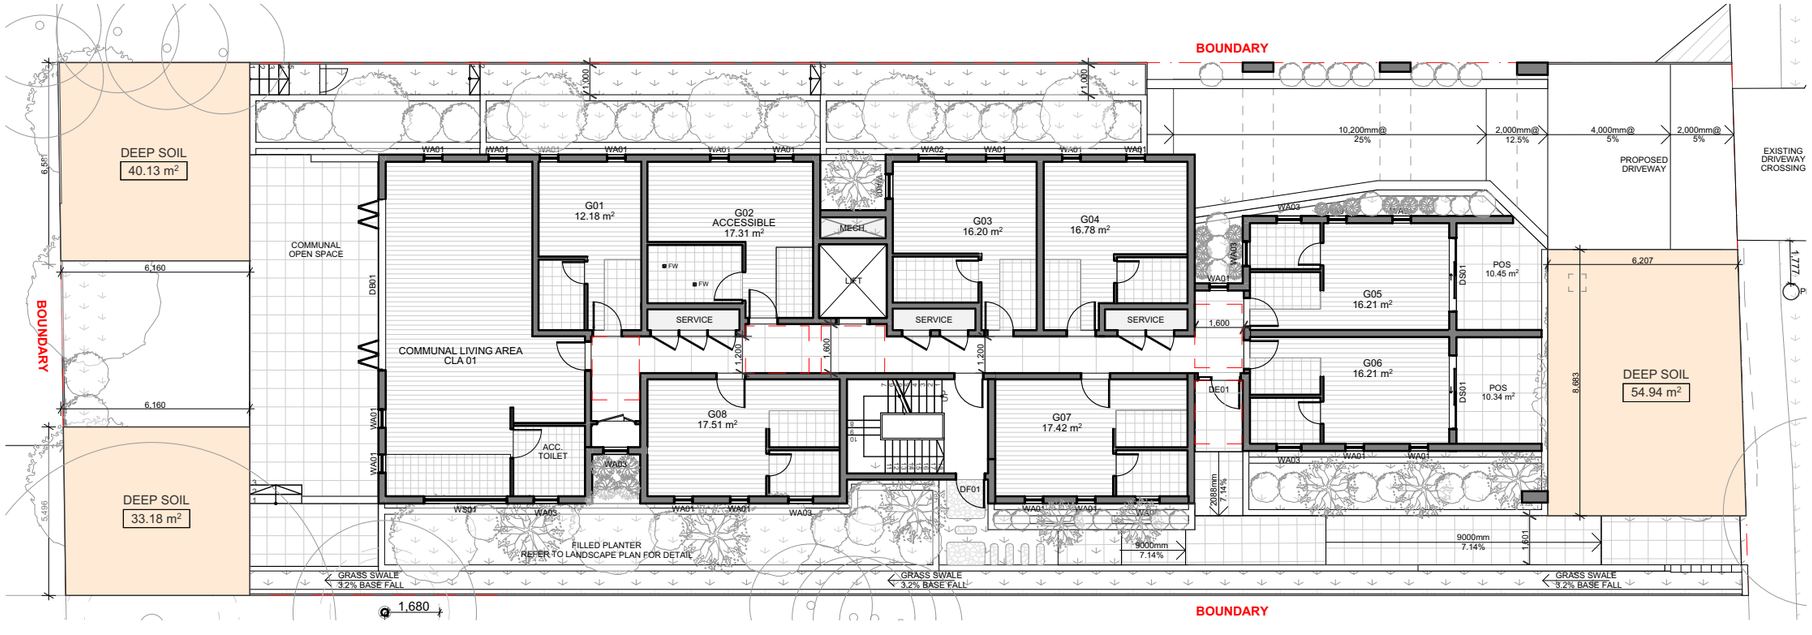

DEEP SOIL AREA - GROUND FLOOR
1:200

SITE AREA: 950.7m²

REQUIRED DEEP SOIL AREA
(MINIMUM 7% OF PLOT AREA): 66.549m²
MIN 3m WIDTH

PROPOSED DEEP SOIL AREA: 128.25 m²
(13.49% OF SITE AREA)

DEEP SOIL AREA

NOTE
The Builder shall check all dimensions and levels on site prior to construction. Notify any errors, discrepancies or omissions to the architect. Refer to written dimensions only. Do not scale drawings. Drawings shall not be used for construction purposes until issued for construction. This drawing reflects a design by Texco Design Pty Ltd and is to be used only for work when authorised in writing by Texco Design Pty Ltd.

All boundaries and contours are subject to survey drawing. All levels to Australian Height Data. It is the contractors responsibility to confirm all measurements on site and locations of any services prior to work on site.

All documents here within are subject to Australian Copyright Laws.

Project Partners
Refer to consultant documentation when directed

- Planning Consultant	- **Think Planners**
- Ecologist	- **SIA Ecological**
- BCA & Access	- **BIA**
- Arborist Consultant	- **NSW Trees**
- QS Consultant	- **Property & Building Assessment**
- Section J Consultant	- **AENEC**
- Civil Engineer	- **JCO Consultants**
- Stormwater Engineer	- **JCO Consultants**
- Landscape Designer	- **Concept**
- Traffic Engineer	- **Genesis Traffic**
- Land Surveyor	- **RDM**
- Geotechnical Engineer	- **STANTEC**
- Flood Engineer	- **HYDRACOR**

RevID	Transmittal Set Date	Approved by	Rev. Note
A	27/03/2024	T.Z	ISSUE FOR DA
B	16/01/2025	T.Z	ISSUE FOR S34
C	11/02/2025	T.Z	ISSUE FOR S34
D	3/03/2025		ISSUE FOR S34
E	13/03/2025	T.Z	ISSUE FOR S34
F	20/03/2025	T.Z	ISSUE FOR S34

Project Designer
TEXCO DESIGN
Nom Arch: NSW ARB 11348
E: office@texcodesign.com.au
P: +61 449 984 889

TRUE NORTH

Drawn | Checked	A.W I J.C |
Revision Date:	20/03/2025
Project NO.	2335
Project Status	S34
Client	MR BILLY CHEN
Site:	74 KEELER ST CARLINGFORD
Climate Zone	5
Wind Region	A


PAPER A3 1:200

DRAWING TITLE : GENERAL
LANDSCAPE & DEEP SOIL CALCULATION


PROJECT NAME :
74 KEELER ST CARLINGFORD

REVISION NO. **F**


DRAWING NO. **A011**

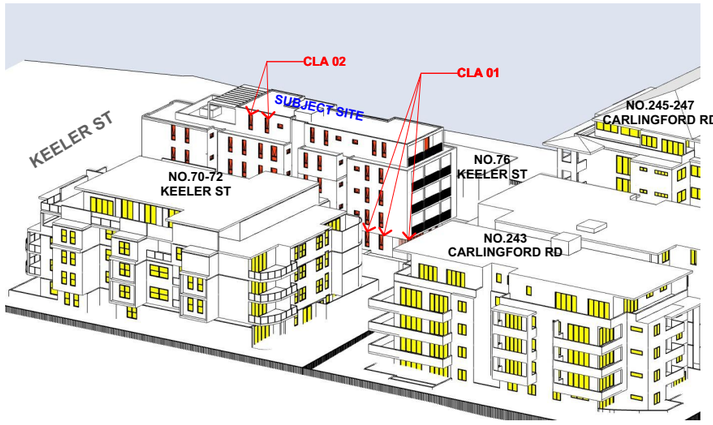


21 JUNE 9AM

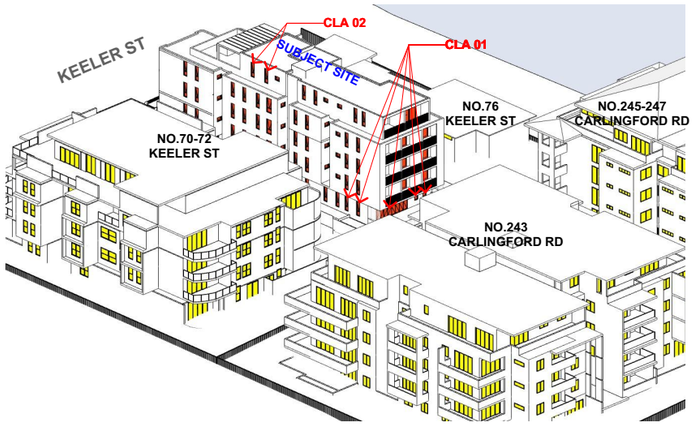


21 JUNE 10AM

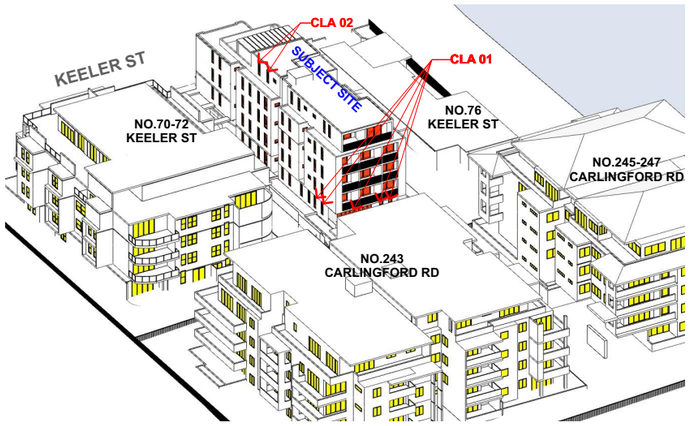


21 JUNE 11AM

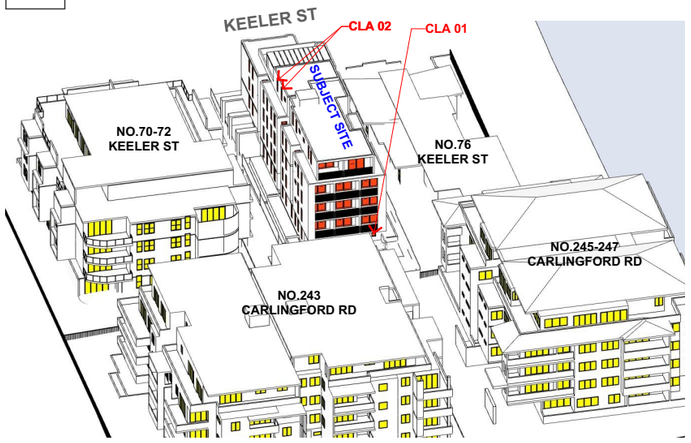


21 JUNE 12PM

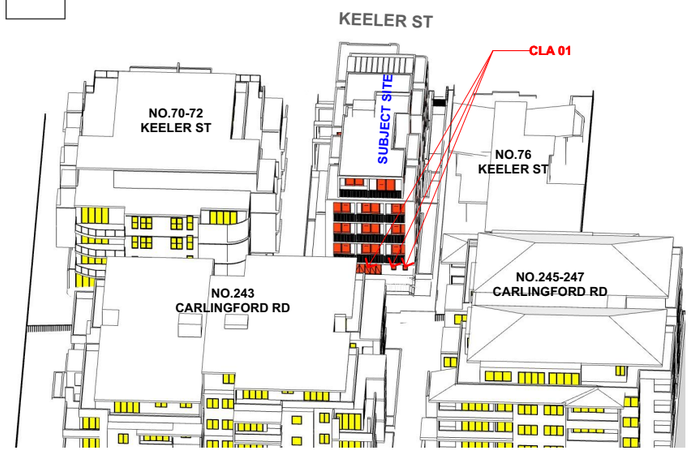

21 JUNE 1PM

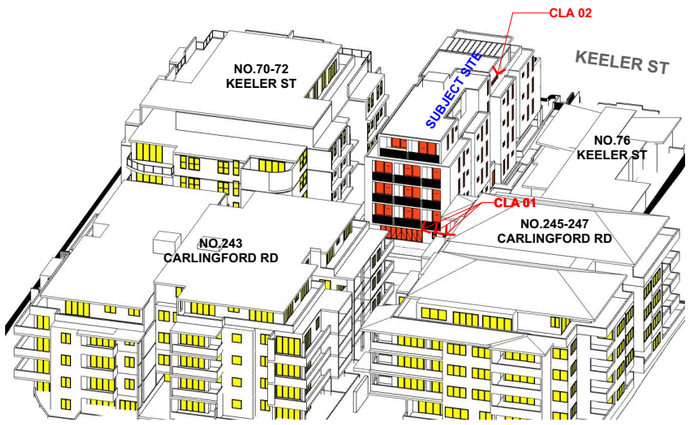

21 JUNE 2PM

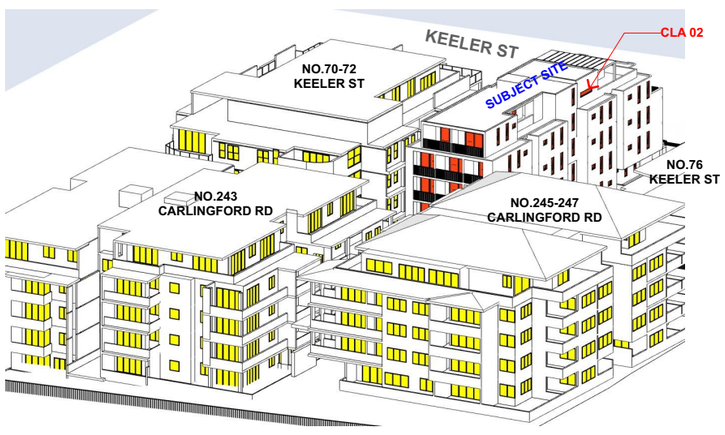

21 JUNE 3PM

LEGEND

OPENINGS OF THE PROPOSED DEVELOPMENT

OPENINGS OF THE NEIGHBOURING BUILDING

SEPP REQUIREMENT:
At least **3** hours of direct solar access will be provided between 9am and 3pm at mid-winter in at least 1 communal living area.

COMMUNAL LIVING AREA	9am - 10am	10am - 11am	11am - 12pm	12pm - 1pm	1pm - 2pm	2pm - 3pm	TOTAL
CLA 01 (GROUND FLOOR)	1hr	1hr	1hr	1hr	1hr	0hr	5hrs
CLA 02 (LEVEL 4)	1hr	1hr	1hr	0hr	0hr	1hr	4hrs

COMPLIES

NOTE
The Builder shall check all dimensions and levels on site prior to construction. Notify any errors, discrepancies or omissions to the architect. Refer to written dimensions only. Do not scale drawings. Drawings shall not be used for construction purposes until issued for construction. This drawing reflects a design by Texco Design Pty Ltd and is to be used only for work when authorised in writing by Texco Design Pty Ltd.

All boundaries and contours are subject to survey drawing. All levels to Australian Height Data. It is the contractors responsibility to confirm all measurements on site and locations of any services prior to work on site.

All documents here within are subject to Australian Copyright Laws.

Project Partners
Refer to consultant documentation when directed

- Planning Consultant	- **Think Planners**
- Ecologist	- **SIA Ecological**
- BCA & Access	- **BIA**
- Arborist Consultant	- **NSW Trees**
- QS Consultant	- **Property & Building Assessment**
- Section J Consultant	- **AENEC**
- Civil Engineer	- **JCO Consultants**
- Stormwater Engineer	- **JCO Consultants**
- Landscape Designer	- **Conzept**
- Traffic Engineer	- **Genesis Traffic**
- Land Surveyor	- **RGM**
- Geotechnical Engineer	- **STANTEC**
- Flood Engineer	- **HYDRACOR**

RevID	Transmittal Set Date	Approved by	Rev. Note
A	27/03/2024	T.Z	ISSUE FOR DA
B	16/01/2025	T.Z	ISSUE FOR S34
C	11/02/2025	T.Z	ISSUE FOR S34
D	3/03/2025		ISSUE FOR S34
E	13/03/2025	T.Z	ISSUE FOR S34
F	20/03/2025	T.Z	ISSUE FOR S34

Project Designer
TEXCO DESIGN
Nom Arch: NSW ARB 11348
E: office@texcodesign.com.au
P: +61 449 984 889

TRUE NORTH

Drawn | Checked	A.W I J.C |
Revision Date:	20/03/2025
Project NO.	2335
Project Status	S34
Client	MR BILLY CHEN
Site:	74 KEELER ST CARLINGFORD
Climate Zone	5
Wind Region	A


PAPER
A3

DRAWING TITLE :
GENERAL
SUN EYE DIAGRAM - 21ST JUNE


PROJECT NAME :
74 KEELER ST CARLINGFORD

REVISION NO.
F


DRAWING NO.
A012

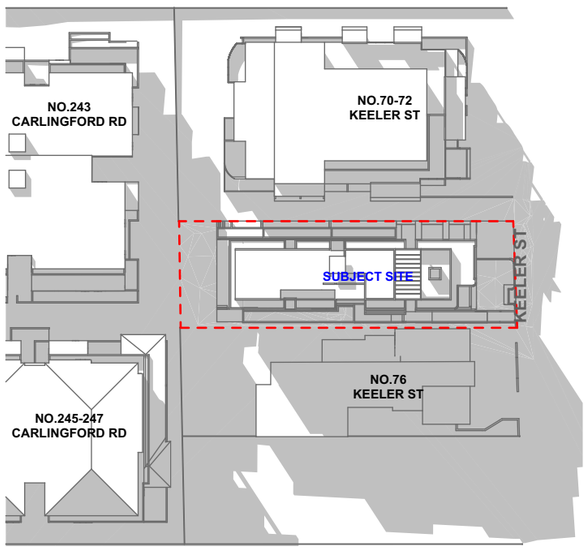


01 - SHADOW PLAN 21 JUNE at 9AM

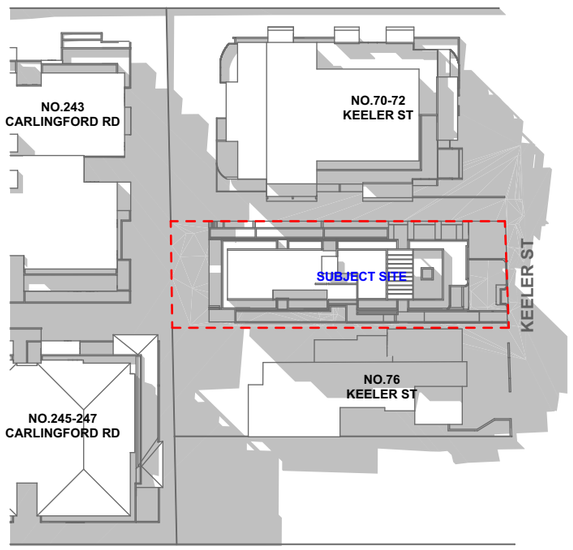


02 - SHADOW PLAN 21 JUNE at 10AM

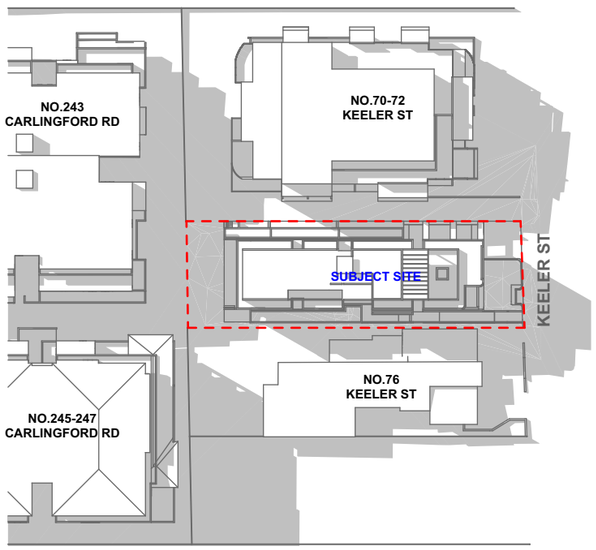


03 - SHADOW PLAN 21 JUNE at 11AM

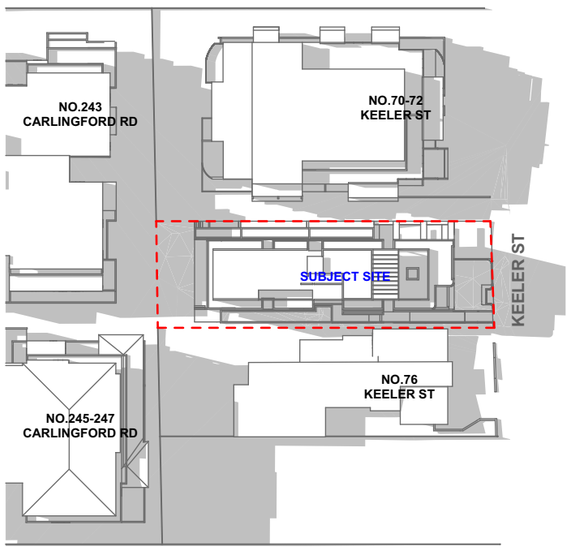


04 - SHADOW PLAN 21 JUNE at 12PM

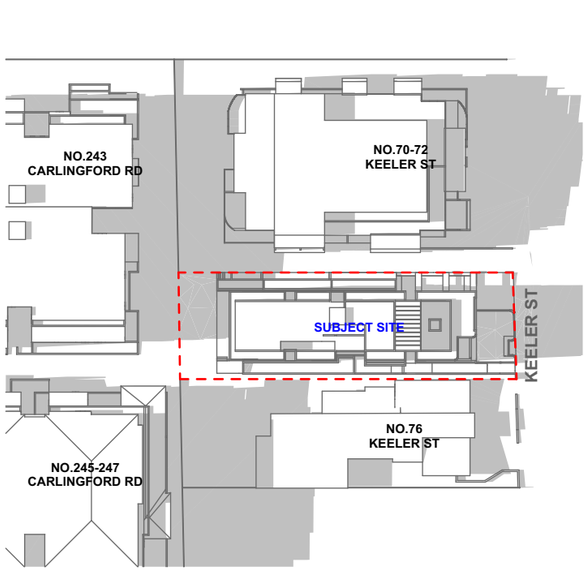

05 - SHADOW PLAN 21 JUNE at 1PM

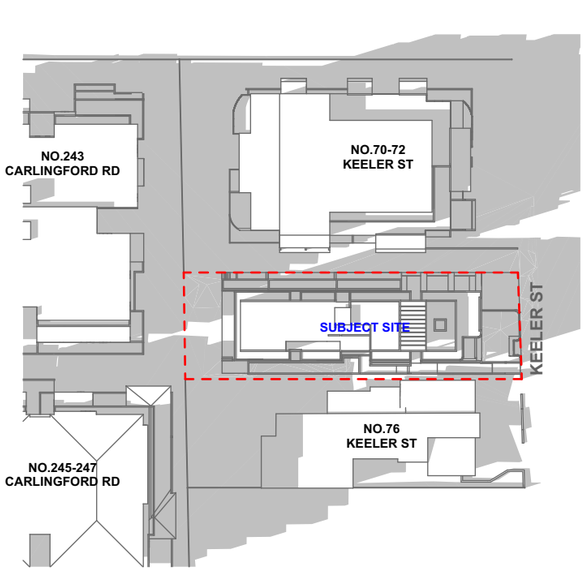

06 - SHADOW PLAN 21 JUNE at 2PM

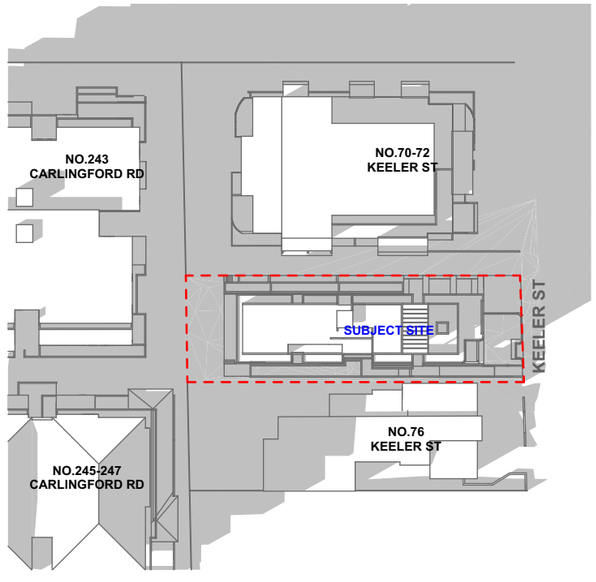

07 - SHADOW PLAN 21 JUNE at 3PM

NOTE

The Builder shall check all dimensions and levels on site prior to construction. Notify any errors, discrepancies or omissions to the architect. Refer to written dimensions only. Do not scale drawings. Drawings shall not be used for construction purposes until issued for construction. This drawing reflects a design by Texco Design Pty Ltd and is to be used only for work when authorised in writing by Texco Design Pty Ltd.

All boundaries and contours are subject to survey drawing. All levels to Australian Height Data. It is the contractors responsibility to confirm all measurements on site and locations of any services prior to work on site.

All documents here within are subject to Australian Copyright Laws.

Project Partners

Refer to consultant documentation when directed

- Planning Consultant	- Think Planners
- Ecologist	- SIA Ecological
- BCA & Access	- BIA
- Arborist Consultant	- NSW Trees
- QS Consultant	- Property & Building Assessment
- Section J Consultant	- AENEC
- Civil Engineer	- JCO Consultants
- Stormwater Engineer	- JCO Consultants
- Landscape Designer	- Concept
- Traffic Engineer	- Genesis Traffic
- Land Surveyor	- RGM
- Geotechnical Engineer	- STANTEC
- Flood Engineer	- HYDRACOR

RevID	Transmittal Set Date	Approved by	Rev. Note
A	27/03/2024	T.Z	ISSUE FOR DA
B	16/01/2025	T.Z	ISSUE FOR S34
C	11/02/2025	T.Z	ISSUE FOR S34
D	3/03/2025		ISSUE FOR S34
E	13/03/2025	T.Z	ISSUE FOR S34
F	20/03/2025	T.Z	ISSUE FOR S34

Project Designer

TEXCO DESIGN
Nom Arch: NSW ARB 11348
E: office@texcodesign.com.au
P: +61 449 984 889

N
TRUE NORTH

Drawn | Checked	A.W I J.C |
Revision Date:	20/03/2025
Project NO.	2335
Project Status	S34
Client	MR BILLY CHEN
Site:	74 KEELER ST CARLINGFORD
Climate Zone	5
Wind Region	A


PAPER
A3
1:1000


DRAWING TITLE :
GENERAL
SHADOW DIAGRAM - 21ST JUNE

PROJECT NAME :
74 KEELER ST CARLINGFORD

REVISION NO.
F

DRAWING NO.
A013

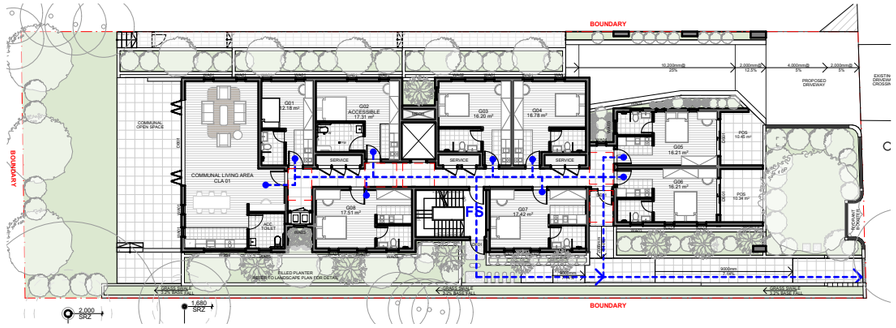
BOUNDARY
COMMUNAL OPEN SPACE
COMMUNAL LIVING AREA
CLA 01
G01
2.18 m²
G02
ACCESSIBLE
17.31 m²
G03
16.20 m²
G04
16.78 m²
G05
16.21 m²
G06
16.21 m²
G07
17.49 m²
G08
17.51 m²
POS
10.60 m²
POS
7.60 m²
POS
7.60 m²
POS
7.60 m²
POS
10.34 m²
POS
7.60 m²
POS
7.60 m²
POS
7.60

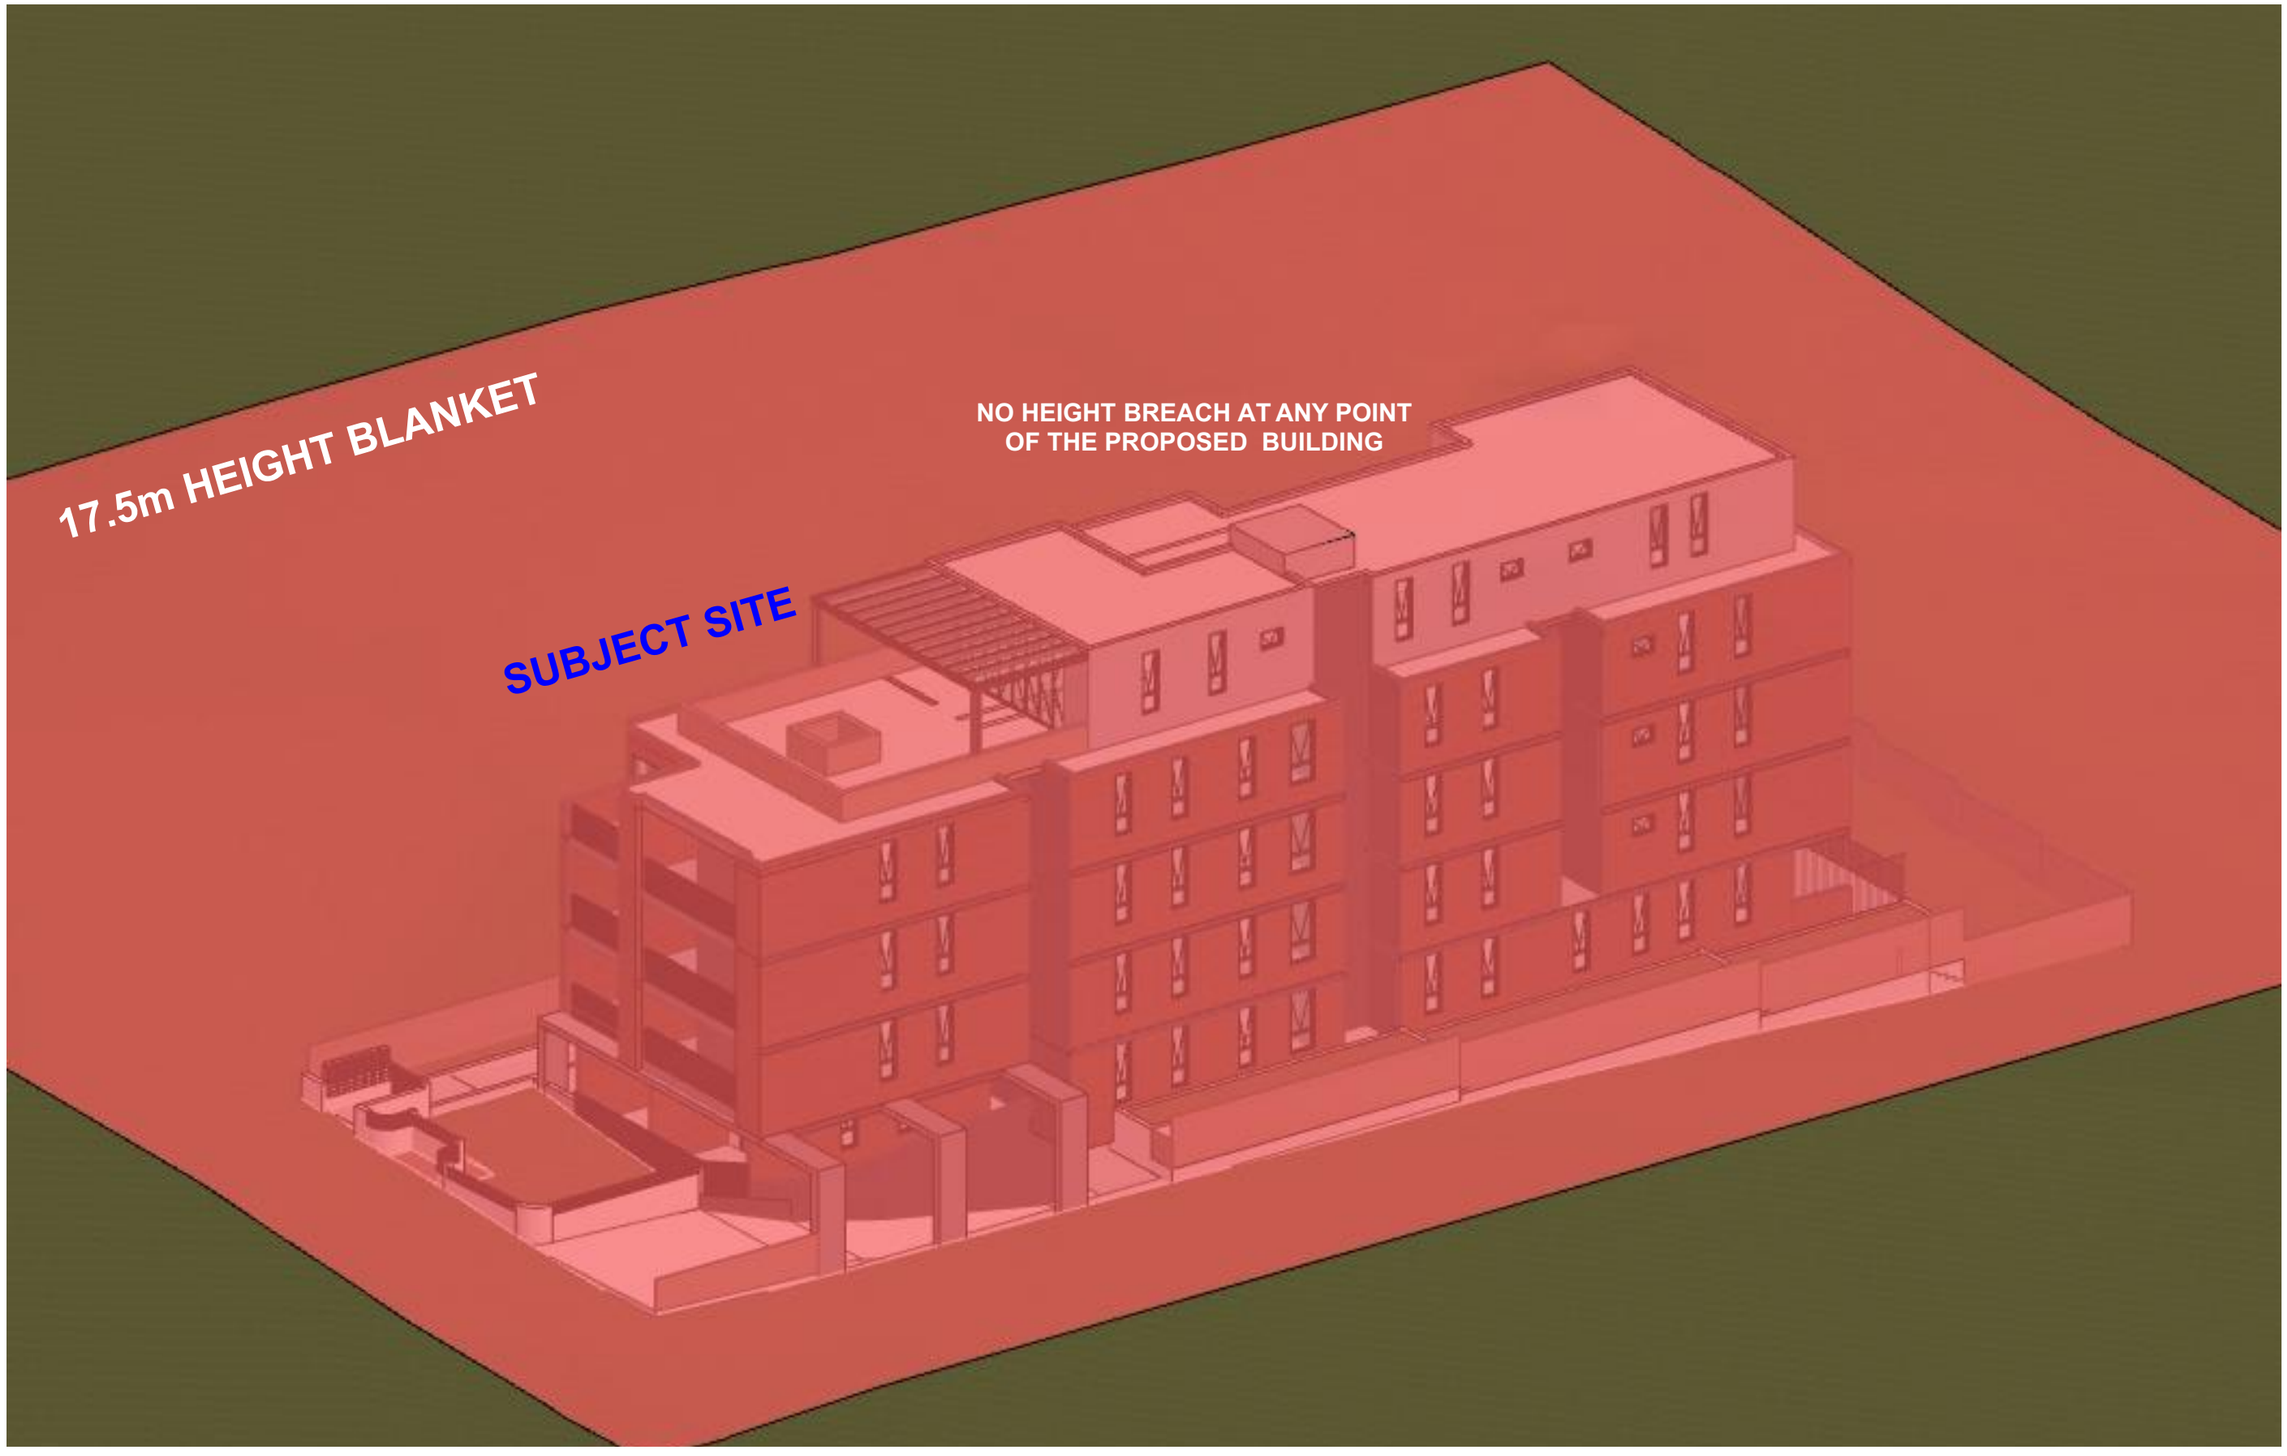

NOTE

The Builder shall check all dimensions and levels on site prior to construction. Notify any errors, discrepancies or omissions to the architect. Refer to written dimensions only. Do not scale drawings. Drawings shall not be used for construction purposes until issued for construction. This drawing reflects a design by Texco Design Pty Ltd and is to be used only for work when authorised in writing by Texco Design Pty Ltd.

All boundaries and contours are subject to survey drawing. All levels to Australian Height Data. It is the contractors responsibility to confirm all measurements on site and locations of any services prior to work on site.

All documents here within are subject to Australian Copyright Laws.

Project Partners

Refer to consultant documentation when directed

- Planning Consultant	- **Think Planners**
- Ecologist	- **SIA Ecological**
- BCA & Access	- **BIA**
- Arborist Consultant	- **NSW Trees**
- QS Consultant	- **Property & Building Assessment**
- Section J Consultant	- **JCDC**
- Civil Engineer	- **ADW Consultants**
- Stormwater Engineer	- **JCO Consultants**
- Landscape Designer	- **Concept**
- Traffic Engineer	- **Genesis Traffic**
- Land Surveyor	- **RGM**
- Geotechnical Engineer	- **STANTEC**
- Flood Engineer	- **HYDRACOR**

RevID	Transmittal Set Date	Approved by	Rev. Note
A	27/03/2024	T.Z	ISSUE FOR DA
B	16/01/2025	T.Z	ISSUE FOR S34
C	11/02/2025	T.Z	ISSUE FOR S34
D	3/03/2025		ISSUE FOR S34
E	13/03/2025	T.Z	ISSUE FOR S34
F	20/03/2025	T.Z	ISSUE FOR S34

Project Designer

TEXCO DESIGN

Nom Arch: NSW ARB 11348

E: office@texcodesign.com.au P: +61 449 984 889

TRUE NORTH

Drawn | Checked	A.W I J.C |
Revision Date:	20/03/2025
Project NO.	2335
Project Status	S34
Client	MR BILLY CHEN
Site:	74 KEELER ST CARLINGFORD
Climate Zone	5
Wind Region	A

PAPER A3 1:100

DRAWING TITLE :

GENERAL


HEIGHT LIMIT DIAGRAM

PROJECT NAME :

74 KEELER ST CARLINGFORD

REVISION NO. **F**

DRAWING NO. **A015**

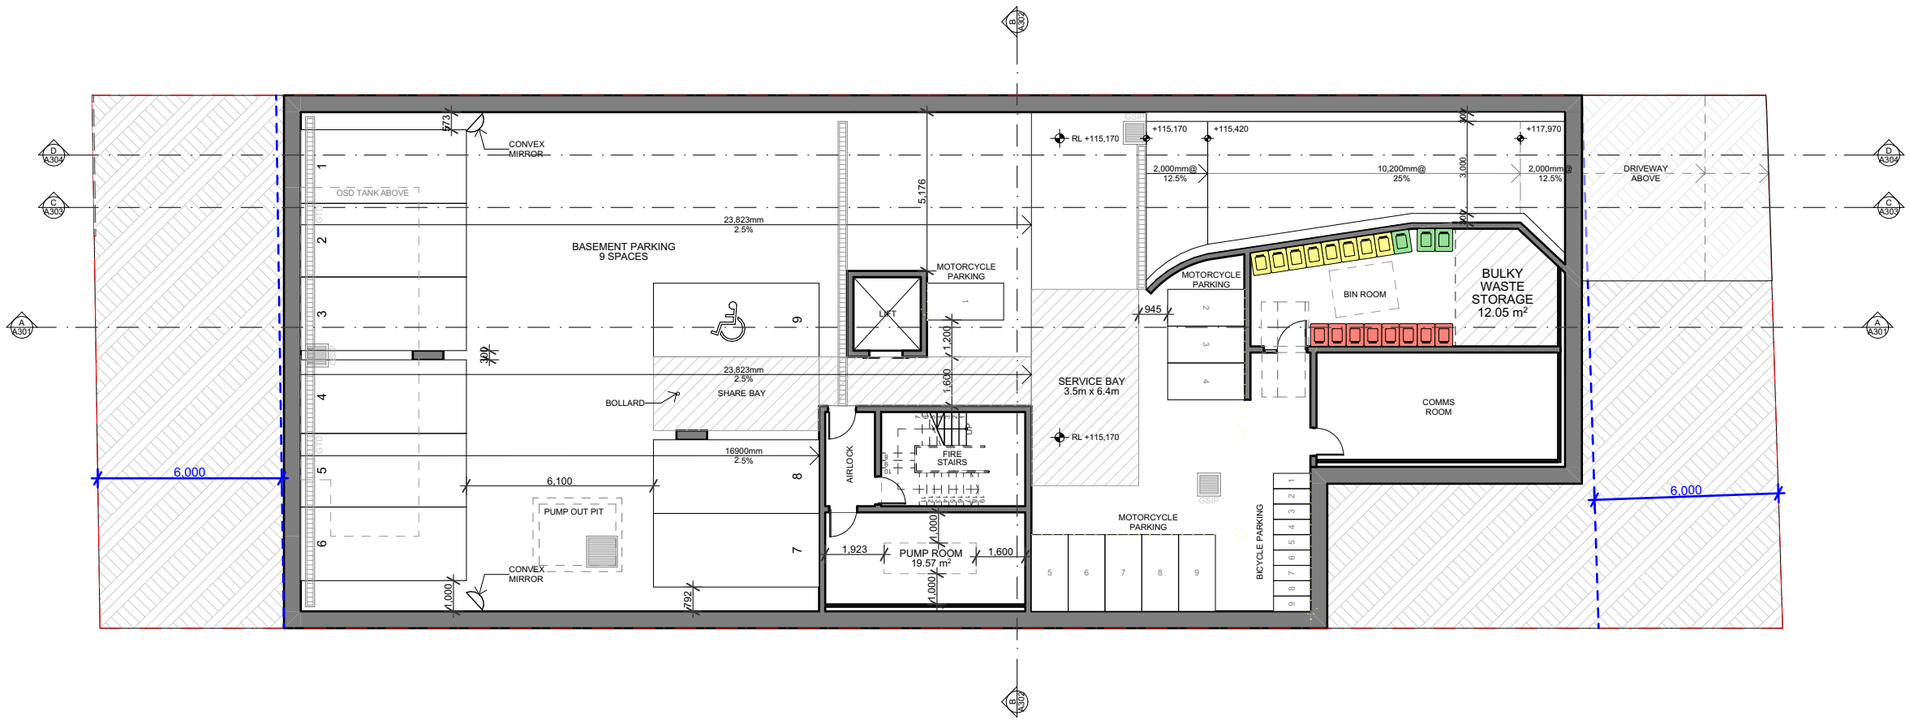

NOTE

The Builder shall check all dimensions and levels on site prior to construction. Notify any errors, discrepancies or omissions to the architect. Refer to written dimensions only. Do not scale drawings. Drawings shall not be used for construction purposes until issued for construction. This drawing reflects a design by Texco Design Pty Ltd and is to be used only for work when authorised in writing by Texco Design Pty Ltd.

All boundaries and contours are subject to survey drawing. All levels to Australian Height Data. It is the contractors responsibility to confirm all measurements on site and locations of any services prior to work on site.

All documents here within are subject to Australian Copyright Laws.

Project Partners

Refer to consultant documentation when directed

- Planning Consultant	- **Think Planners**
- Ecologist	- **SIA Ecological**
- BCA & Access	- **BIA**
- Arborist Consultant	- **NSW Trees**
- QS Consultant	- **Property & Building Assessment**
- Section J Consultant	- **AENEC**
- Civil Engineer	- **JCO Consultants**
- Stormwater Engineer	- **JCO Consultants**
- Landscape Designer	- **Concept**
- Traffic Engineer	- **Genesis Traffic**
- Land Surveyor	- **RGM**
- Geotechnical Engineer	- **STANTEC**
- Flood Engineer	- **HYDRACOR**

RevID	Transmittal Set Date	Approved by	Rev. Note
A	27/03/2024	T.Z	ISSUE FOR DA
B	16/01/2025	T.Z	ISSUE FOR S34
C	11/02/2025	T.Z	ISSUE FOR S34
D	03/03/2025		ISSUE FOR S34
E	13/03/2025	T.Z	ISSUE FOR S34
F	20/03/2025	T.Z	ISSUE FOR S34
G	19/09/2025		ISSUE FOR S34

Project Designer

TEXCO DESIGN

Nom Arch: NSW ARB 11348

E: office@texcodesign.com.au P: +61 449 984 889

TRUE NORTH

Drawn | Checked	A.W I J.C |
Revision Date:	19/09/2025
Project NO.	2335
Project Status	S34
Client	MR BILLY CHEN
Site:	74 KEELER ST CARLINGFORD
Climate Zone	5
Wind Region	A

PAPER

A3

1:200

DRAWING TITLE :

PLANS

BASEMENT PLAN

PROJECT NAME :


74 KEELER ST CARLINGFORD

REVISION NO.

G

DRAWING NO.

A101

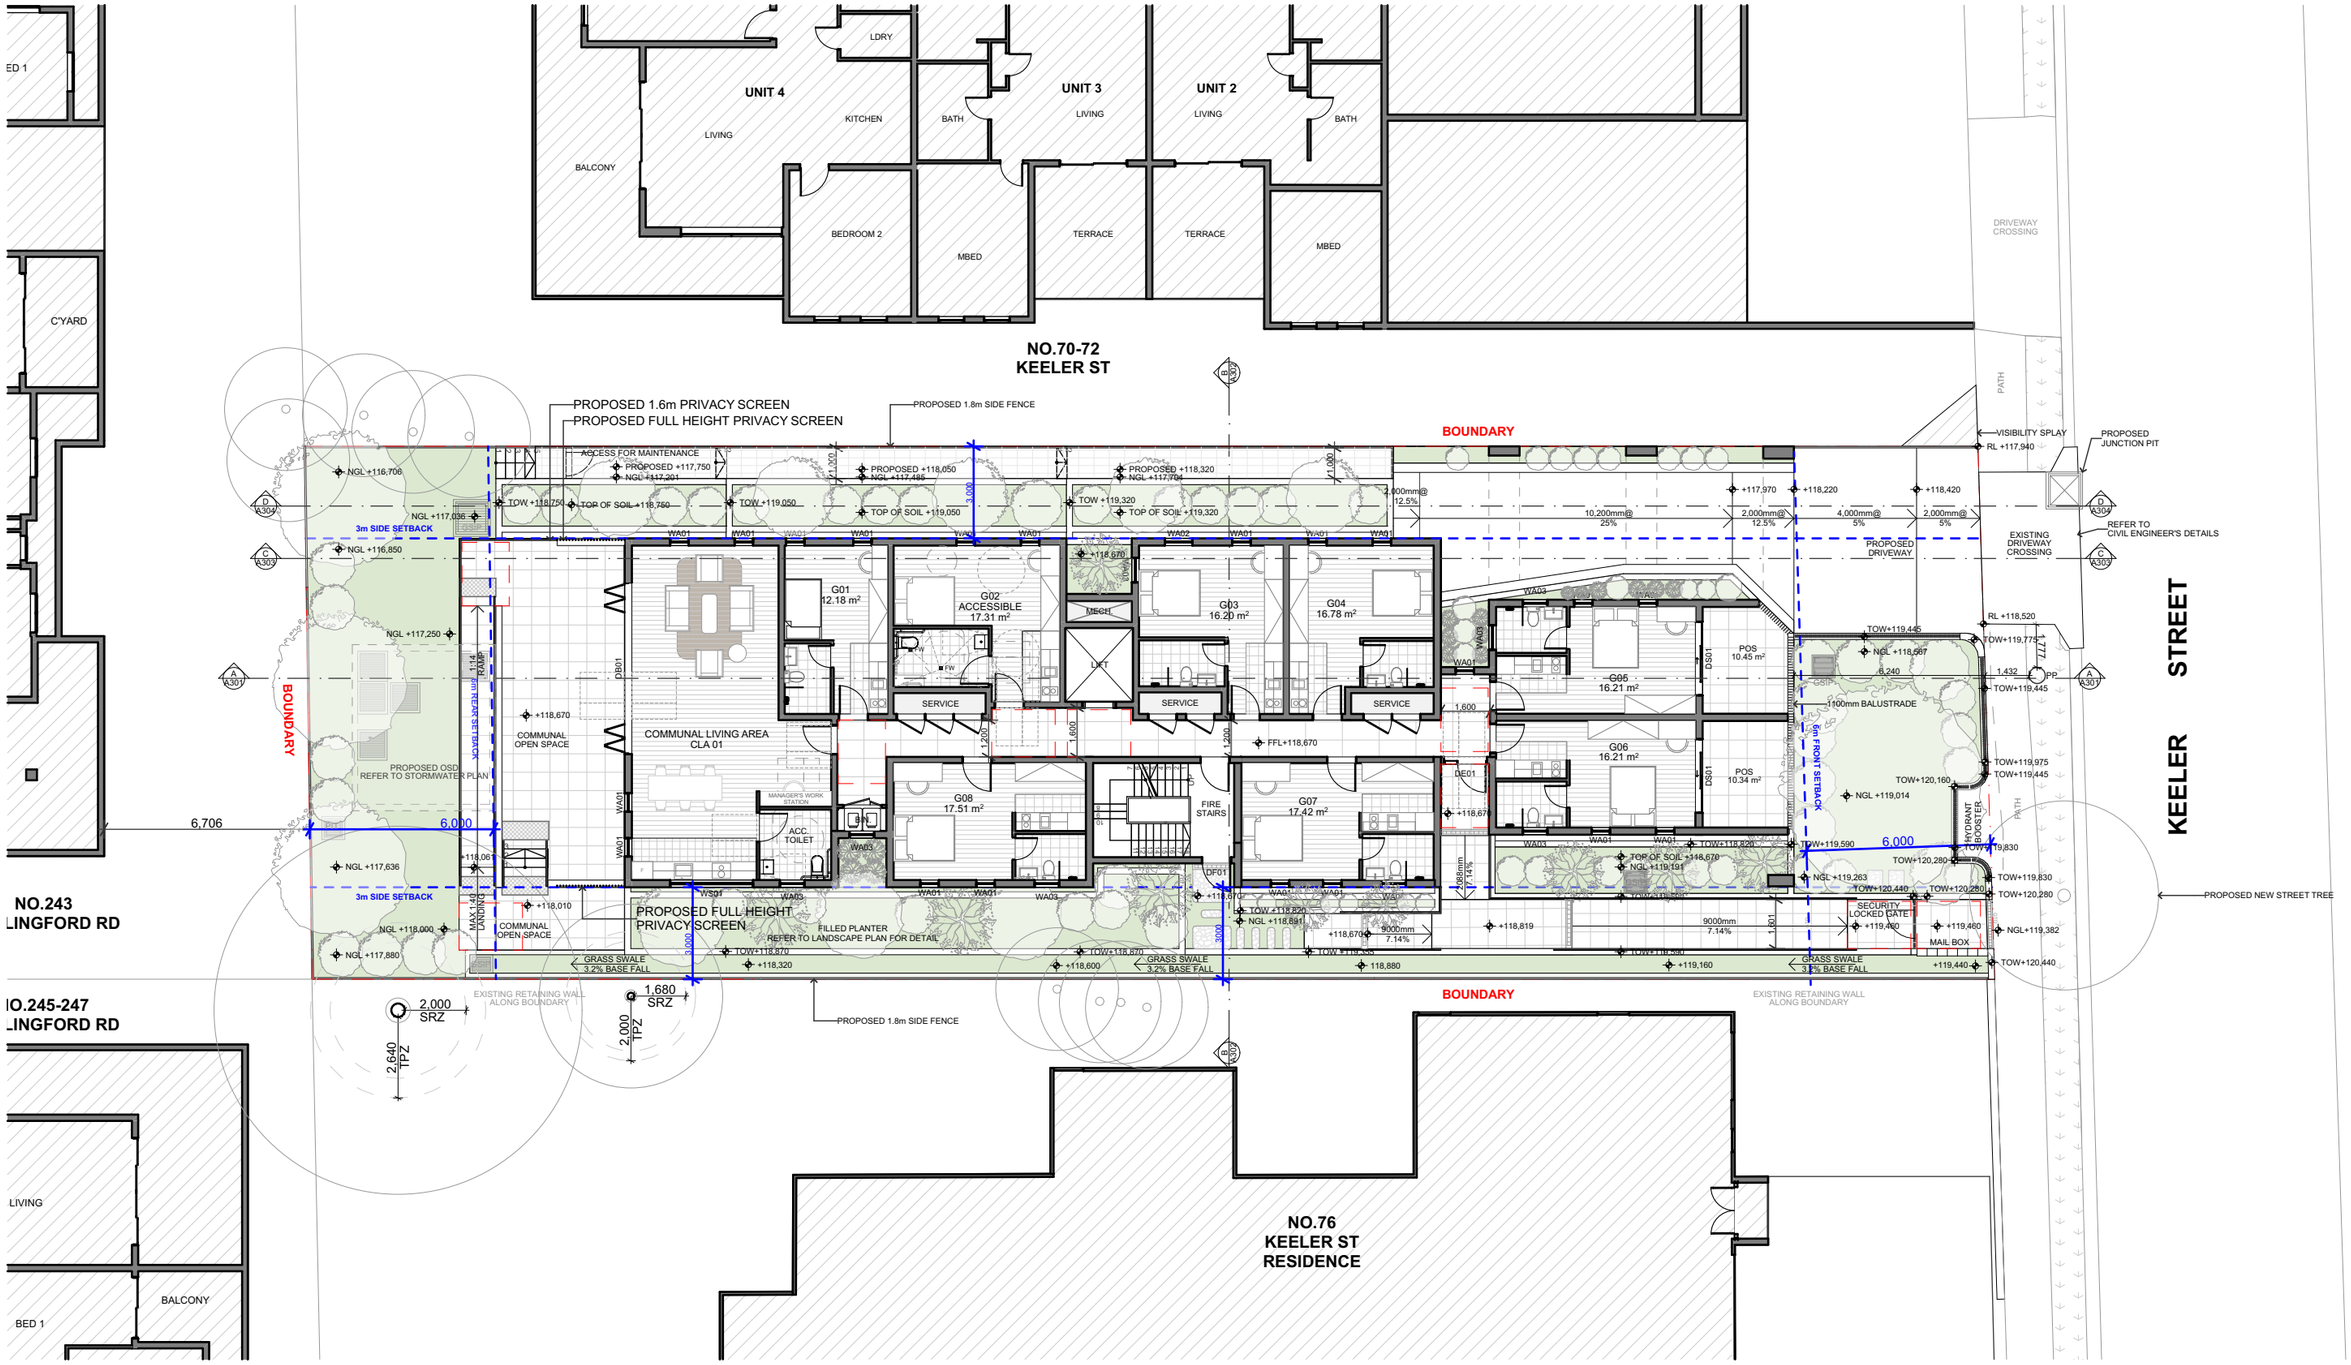

NOTE
The Builder shall check all dimensions and levels on site prior to construction. Notify any errors, discrepancies or omissions to the architect. Refer to written dimensions only. Do not scale drawings. Drawings shall not be used for construction purposes until issued for construction. This drawing reflects a design by Texco Design Pty Ltd and is to be used only for work when authorised in writing by Texco Design Pty Ltd.

All boundaries and contours are subject to survey drawing. All levels to Australian Height Data. It is the contractors responsibility to confirm all measurements on site and locations of any services prior to work on site.

All documents here within are subject to Australian Copyright Laws.

Project Partners
Refer to consultant documentation when directed

- Planning Consultant	- **Think Planners**
- Ecologist	- **SIA Ecological**
- BCA & Access	- **BIA**
- Arborist Consultant	- **NSW Trees**
- QS Consultant	- **Property & Building Assessment**
- Section J Consultant	- **AENEC**
- Civil Engineer	- **JCO Consultants**
- Stormwater Engineer	- **JCO Consultants**
- Landscape Designer	- **Conzept**
- Traffic Engineer	- **Genesis Traffic**
- Land Surveyor	- **RGM**
- Geotechnical Engineer	- **STANTEC**
- Flood Engineer	- **HYDRACOR**

RevID	Transmittal Set Date	Approved by	Rev. Note
A	27/03/2024	T.Z	ISSUE FOR DA
B	16/01/2025	T.Z	ISSUE FOR S34
C	11/02/2025	T.Z	ISSUE FOR S34
D	03/03/2025		ISSUE FOR S34
E	13/03/2025	T.Z	ISSUE FOR S34
F	20/03/2025	T.Z	ISSUE FOR S34
G	19/09/2025		ISSUE FOR S34

Project Designer
TEXCO DESIGN
Nom Arch: NSW ARB 11348
E: office@texcodesign.com.au P: +61 449 984 889

TRUE NORTH

Drawn | Checked A.W I J.C |
Revision Date: 19/09/2025
Project NO. 2335
Project Status S34

Client MR BILLY CHEN
Site: 74 KEELER ST CARLINGFORD
Climate Zone 5
Wind Region A


PAPER A3
1:200

DRAWING TITLE :
PLANS
GROUND FLOOR PLAN

PROJECT NAME :
74 KEELER ST
CARLINGFORD

REVISION NO. G

DRAWING NO. A102

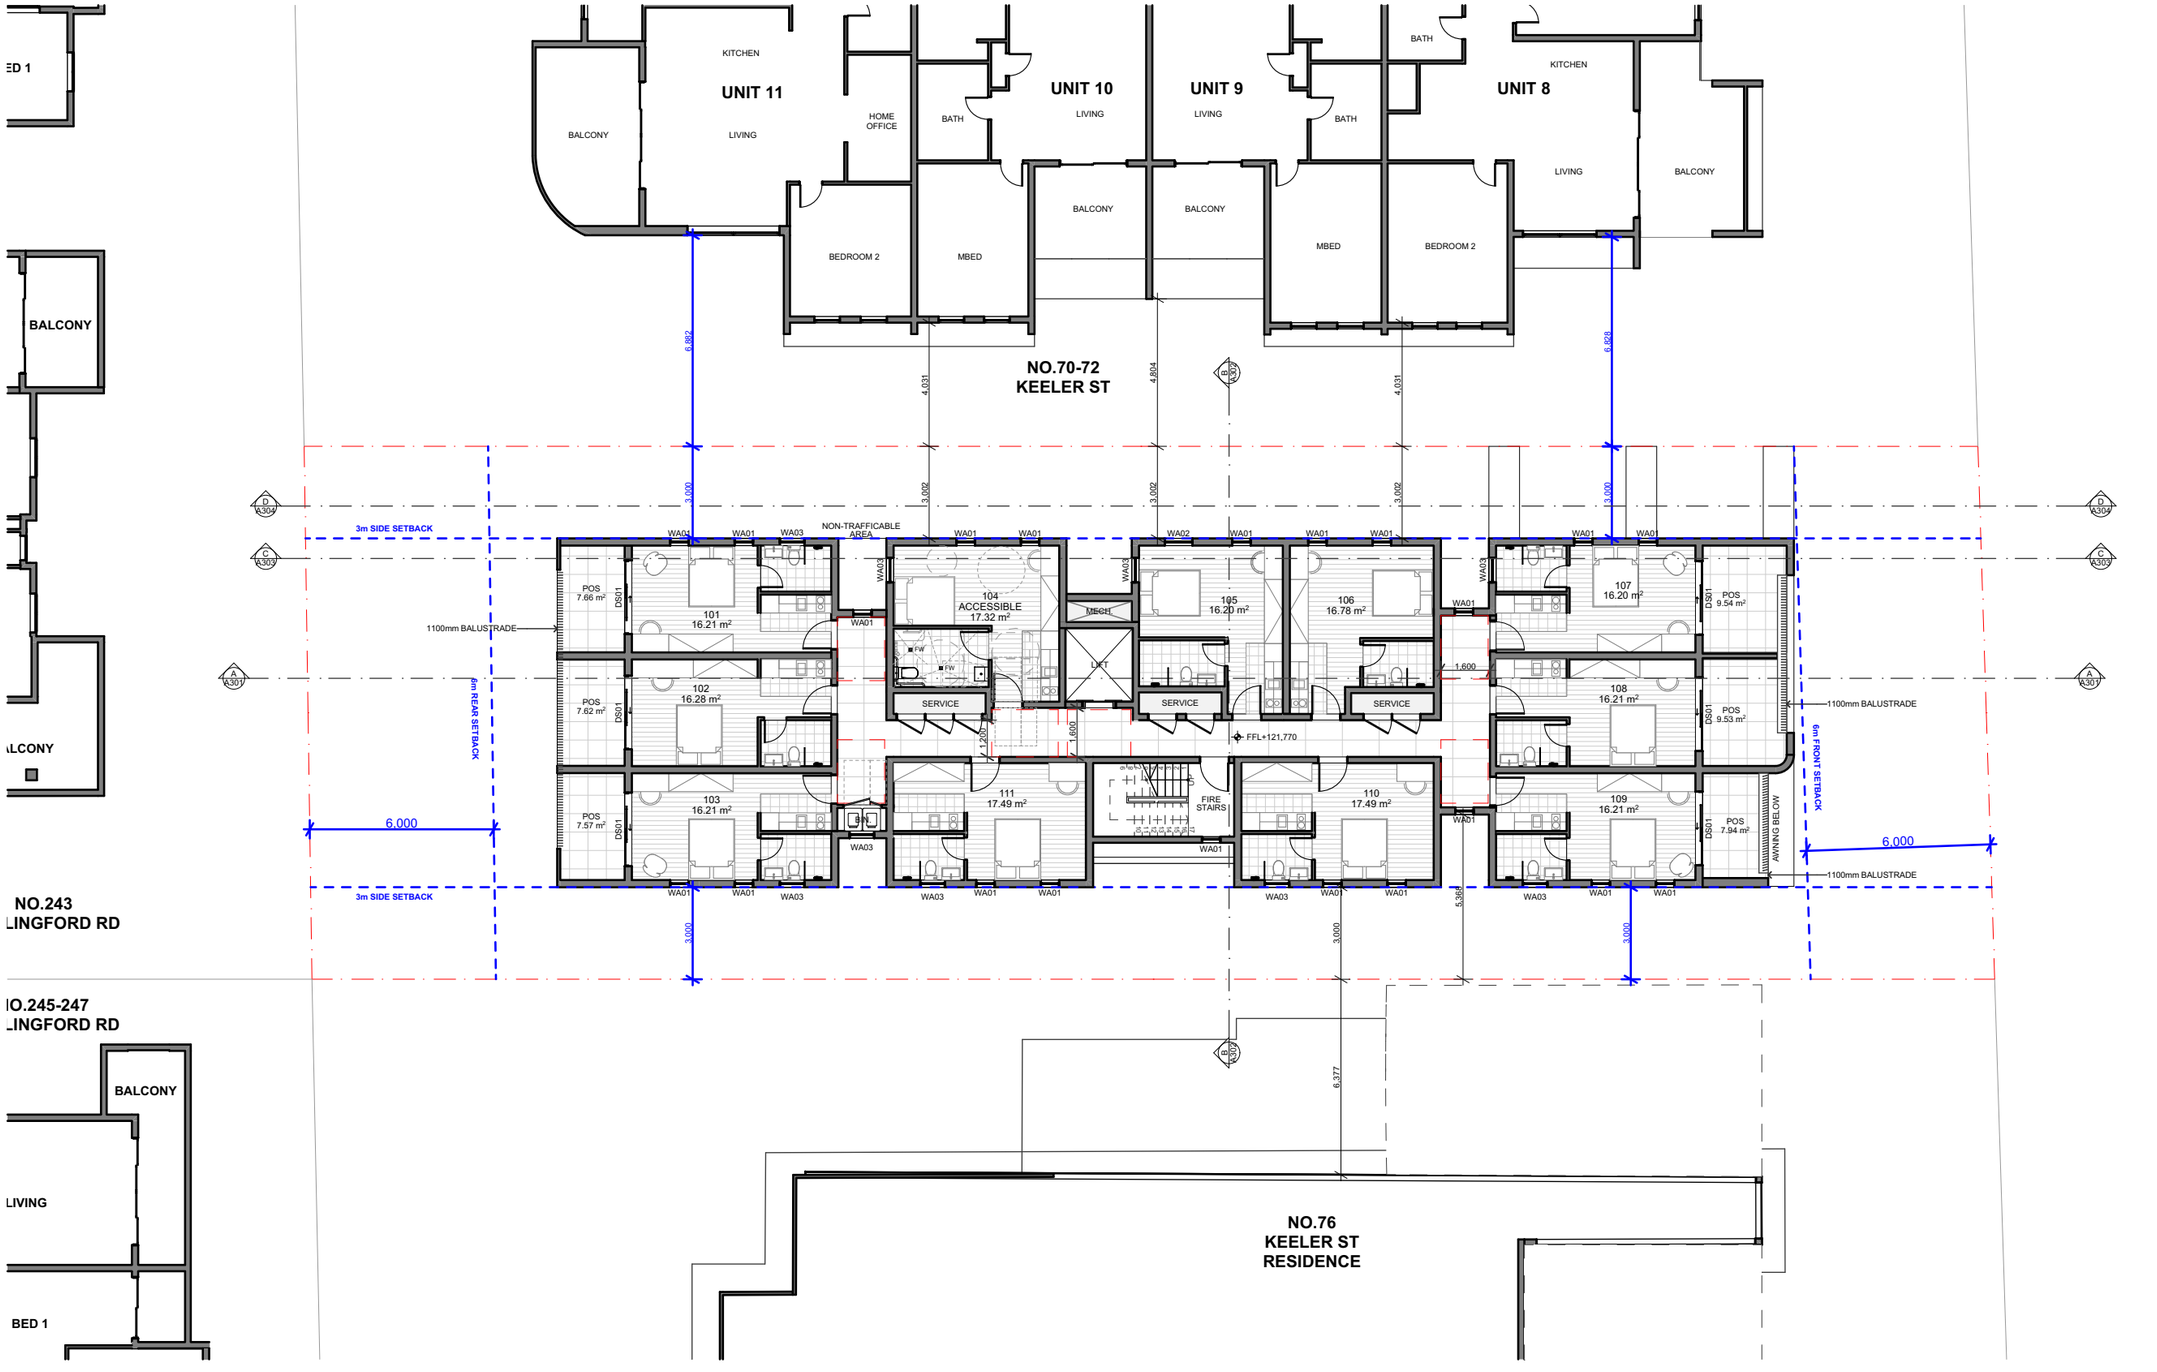

NOTE

The Builder shall check all dimensions and levels on site prior to construction. Notify any errors, discrepancies or omissions to the architect. Refer to written dimensions only. Do not scale drawings. Drawings shall not be used for construction purposes until issued for construction. This drawing reflects a design by Texco Design Pty Ltd and is to be used only for work when authorised in writing by Texco Design Pty Ltd.

All boundaries and contours are subject to survey drawing. All levels to Australian Height Data. It is the contractors responsibility to confirm all measurements on site and locations of any services prior to work on site.

All documents here within are subject to Australian Copyright Laws.

Project Partners

Refer to consultant documentation when directed

- Planning Consultant	- Think Planners
- Ecologist	- SIA Ecological
- BCA & Access	- BIA
- Arborist Consultant	- NSW Trees
- QS Consultant	- Property & Building Assessment
- Section J Consultant	- AENEC
- Civil Engineer	- JCO Consultants
- Stormwater Engineer	- JCO Consultants
- Landscape Designer	- Concept
- Traffic Engineer	- Genesis Traffic
- Land Surveyor	- RGM
- Geotechnical Engineer	- STANTEC
- Flood Engineer	- HYDRACOR

RevID	Transmittal Set Date	Approved by	Rev. Note
A	27/03/2024	T.Z	ISSUE FOR DA
B	16/01/2025	T.Z	ISSUE FOR S34
C	11/02/2025	T.Z	ISSUE FOR S34
D	03/03/2025		ISSUE FOR S34
E	13/03/2025	T.Z	ISSUE FOR S34
F	20/03/2025	T.Z	ISSUE FOR S34
G	19/09/2025		ISSUE FOR S34

Project Designer

TEXCO DESIGN
Nom Arch: NSW ARB 11348
E: office@texcodesign.com.au
P: +61 449 984 889

TRUE NORTH

Drawn | Checked	A.W I J.C |
Revision Date:	19/09/2025
Project NO.	2335
Project Status	S34
Client	MR BILLY CHEN
Site:	74 KEELER ST CARLINGFORD
Climate Zone	5
Wind Region	A


PAPER A3 1:200

DRAWING TITLE : PLANS LEVEL 1 PLAN

PROJECT NAME : 74 KEELER ST CARLINGFORD

REVISION NO. G

DRAWING NO. A103

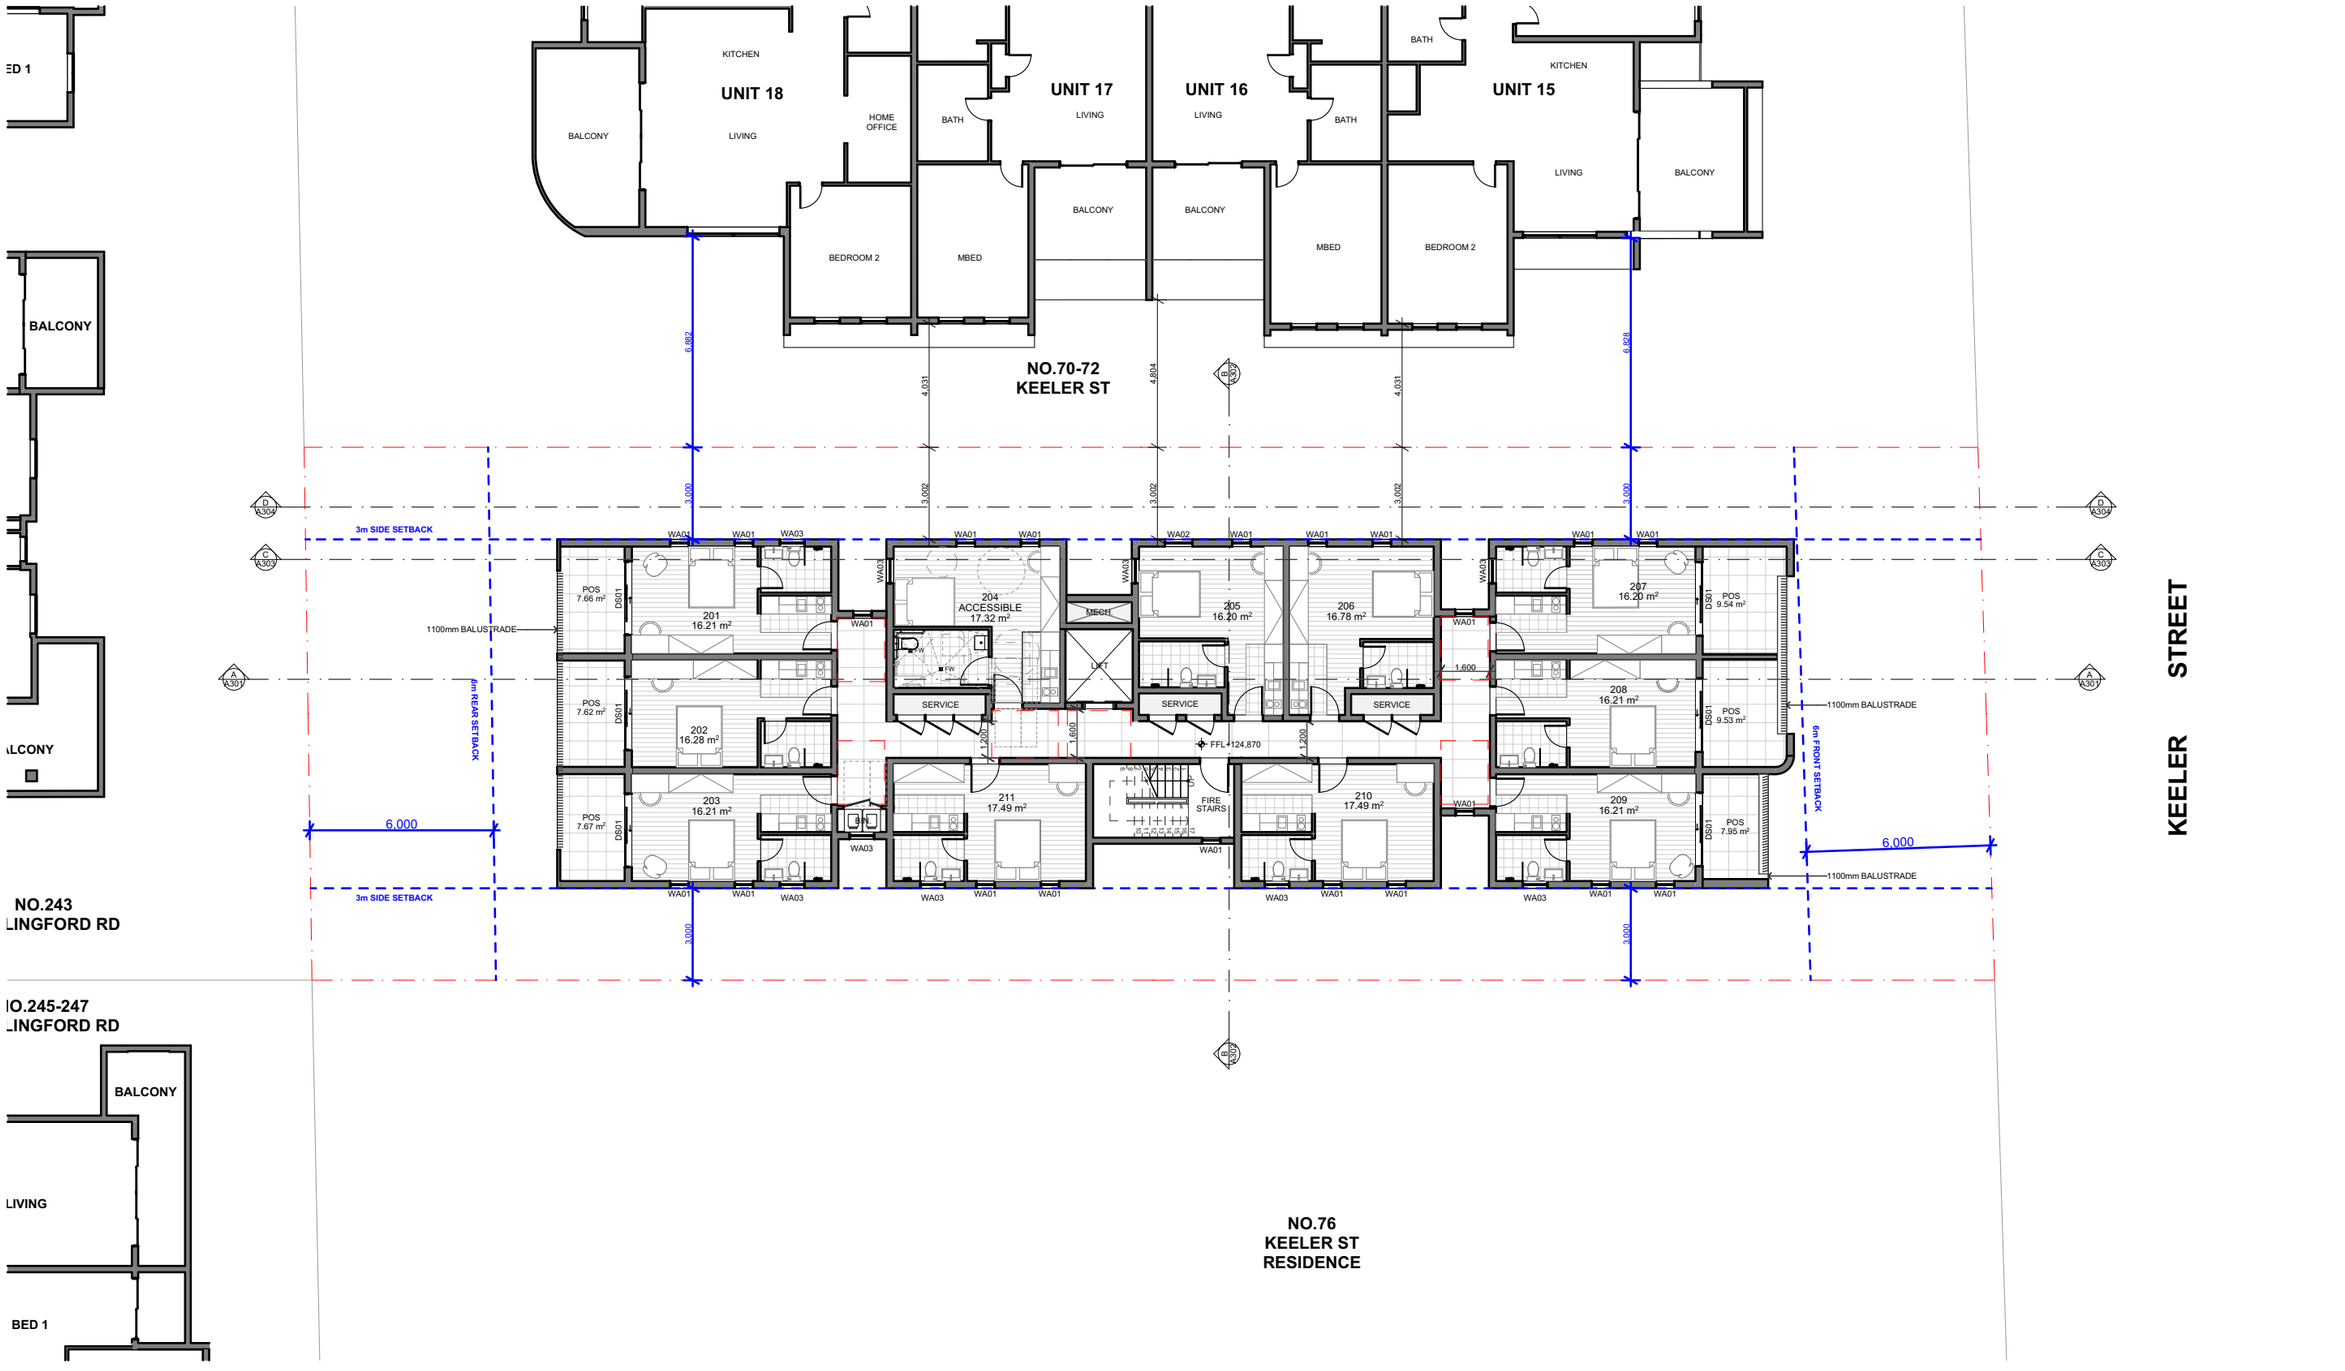

NOTE

The Builder shall check all dimensions and levels on site prior to construction. Notify any errors, discrepancies or omissions to the architect. Refer to written dimensions only. Do not scale drawings. Drawings shall not be used for construction purposes until issued for construction. This drawing reflects a design by Texco Design Pty Ltd and is to be used only for work when authorised in writing by Texco Design Pty Ltd.

All boundaries and contours are subject to survey drawing. All levels to Australian Height Data. It is the contractors responsibility to confirm all measurements on site and locations of any services prior to work on site.

All documents here within are subject to Australian Copyright Laws.

Project Partners

Refer to consultant documentation when directed

- Planning Consultant	- **Think Planners**
- Ecologist	- **SIA Ecological**
- BCA & Access	- **SIA**
- Arborist Consultant	- **NSW Trees**
- QS Consultant	- **Property & Building Assessment**
- Section J Consultant	- **AENEC**
- Civil Engineer	- **JCO Consultants**
- Stormwater Engineer	- **JCO Consultants**
- Landscape Designer	- **Concept**
- Traffic Engineer	- **Genesis Traffic**
- Land Surveyor	- **RDM**
- Geotechnical Engineer	- **STANTEC**
- Flood Engineer	- **HYDRACOR**

RevID	Transmittal Set Date	Approved by	Rev. Note
A	27/03/2024	T.Z	ISSUE FOR DA
B	16/01/2025	T.Z	ISSUE FOR S34
C	11/02/2025	T.Z	ISSUE FOR S34
D	03/03/2025		ISSUE FOR S34
E	13/03/2025	T.Z	ISSUE FOR S34
F	20/03/2025	T.Z	ISSUE FOR S34
G	19/09/2025		ISSUE FOR S34

Project Designer

TEXCO DESIGN

Nom Arch: NSW ARB 11348

E: office@texcodesign.com.au P: +61 449 984 889

TRUE NORTH

Drawn | Checked	A.W I J.C |
Revision Date:	19/09/2025
Project NO.	2335
Project Status	S34
Client	MR BILLY CHEN
Site:	74 KEELER ST CARLINGFORD
Climate Zone	5
Wind Region	A

PAPER A3

1:200

DRAWING TITLE :

PLANS

LEVEL 2 PLAN

PROJECT NAME :

74 KEELER ST CARLINGFORD

REVISION NO. **G**

DRAWING NO. **A104**